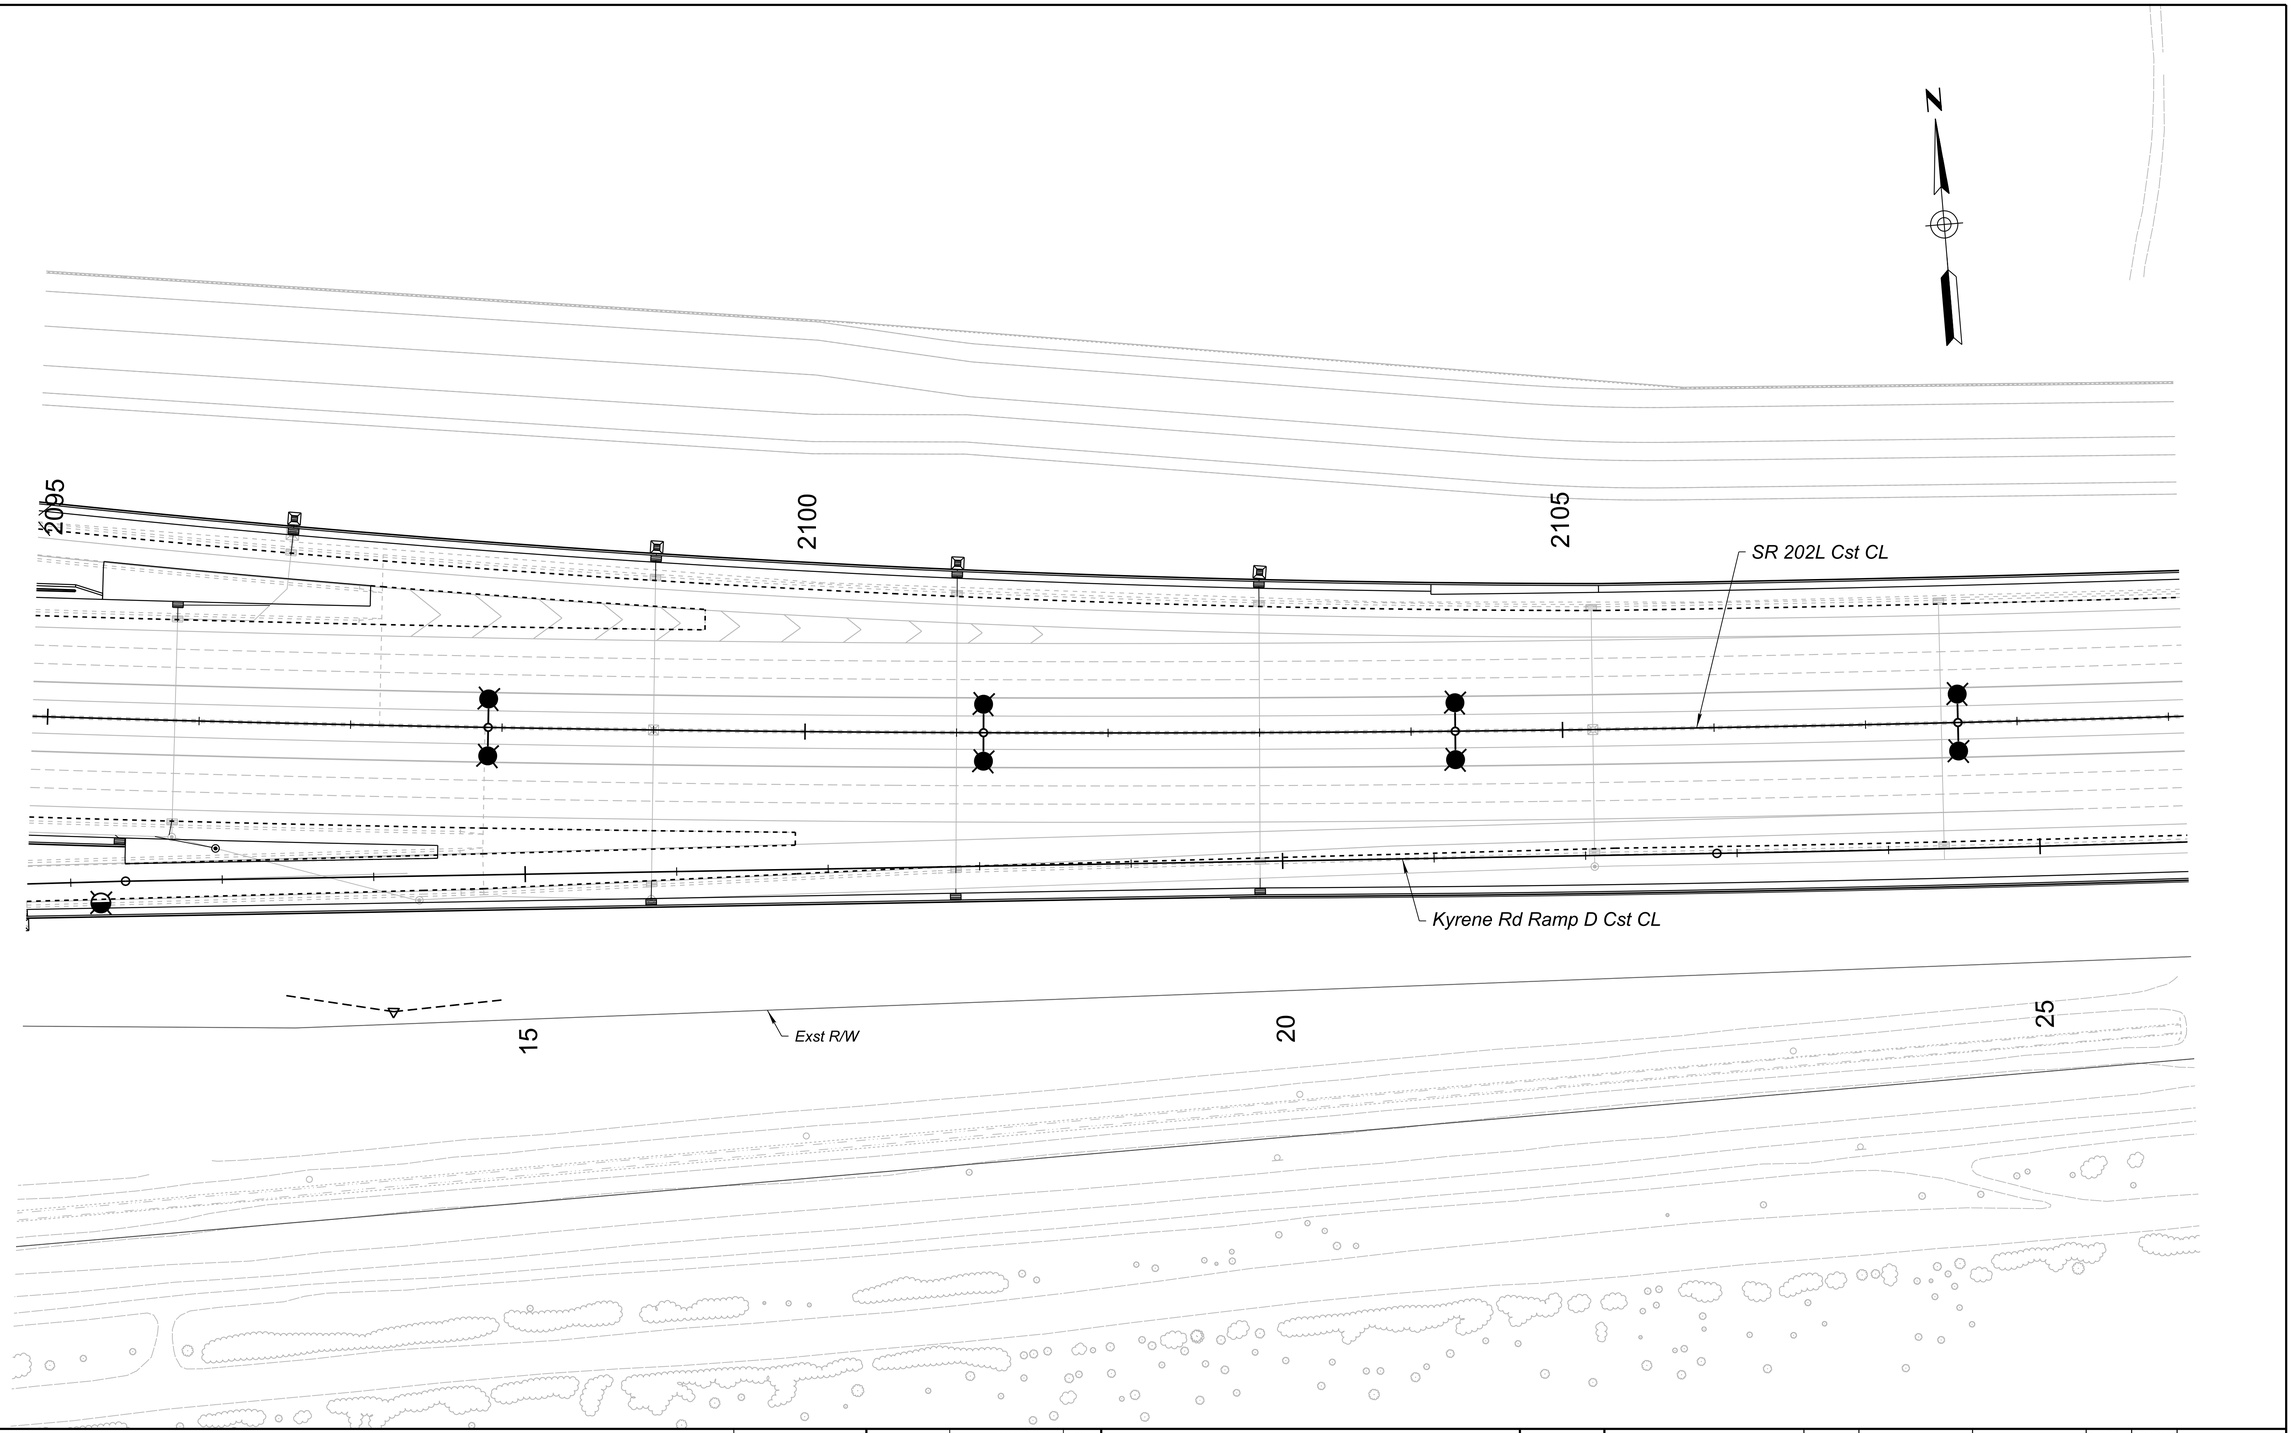


| | | | | | | | | | | |
|---|---|---|---|---|---|---|---|---|---|---|
| PRELIMINARY<br>**STAGE III**<br>**Review**<br>NOT FOR CONSTRUCTION OR RECORDING | | NAME | DATE | ARIZONA DEPARTMENT OF TRANSPORTATION<br>PROJECT DELIVERY AND OPERATIONS DIVISION<br>DRAINAGE DESIGN SECTION | ROUTE<br>SR 202L | F.H.W.A. Arizona Division | STATE<br>ARIZ. | PROJECT NO. | FEDERAL ID NO. | SHEET NO. / TOTAL SHEETS / RECORD DRAWING |
| | DESIGN | | | | MILEPOST | | | | | |
| | DRAWN | | | | | | | | | |
| | CHECKED | | | | | | | | | |
| | TYPSA | 501 N 44th St, Suite 300<br>Phoenix, AZ 85008-4505<br>Tel (602) 454-0402<br>www.typsa.us | | SR 202L<br>DRAINAGE PLAN SHEET<br>STA 2095+00 TO 2109+00 | STRUCTURE NO. | LOCATION SR 202L SANTAN FREEWAY - I-10 TO SR 101L | | | | DWG No. D-02.10 |
| | | | | | | TRACS NO. F0847 01D | | | | ____ OF____ |