NO.	DESCRIPTION OF REVISIONS	MADE BY	DATE
R00	RFC RELEASE	TM	08/18/25

SURVEY NO. | FINISHED PLANS - | REVISIONS - | LOCATION - | DATE -

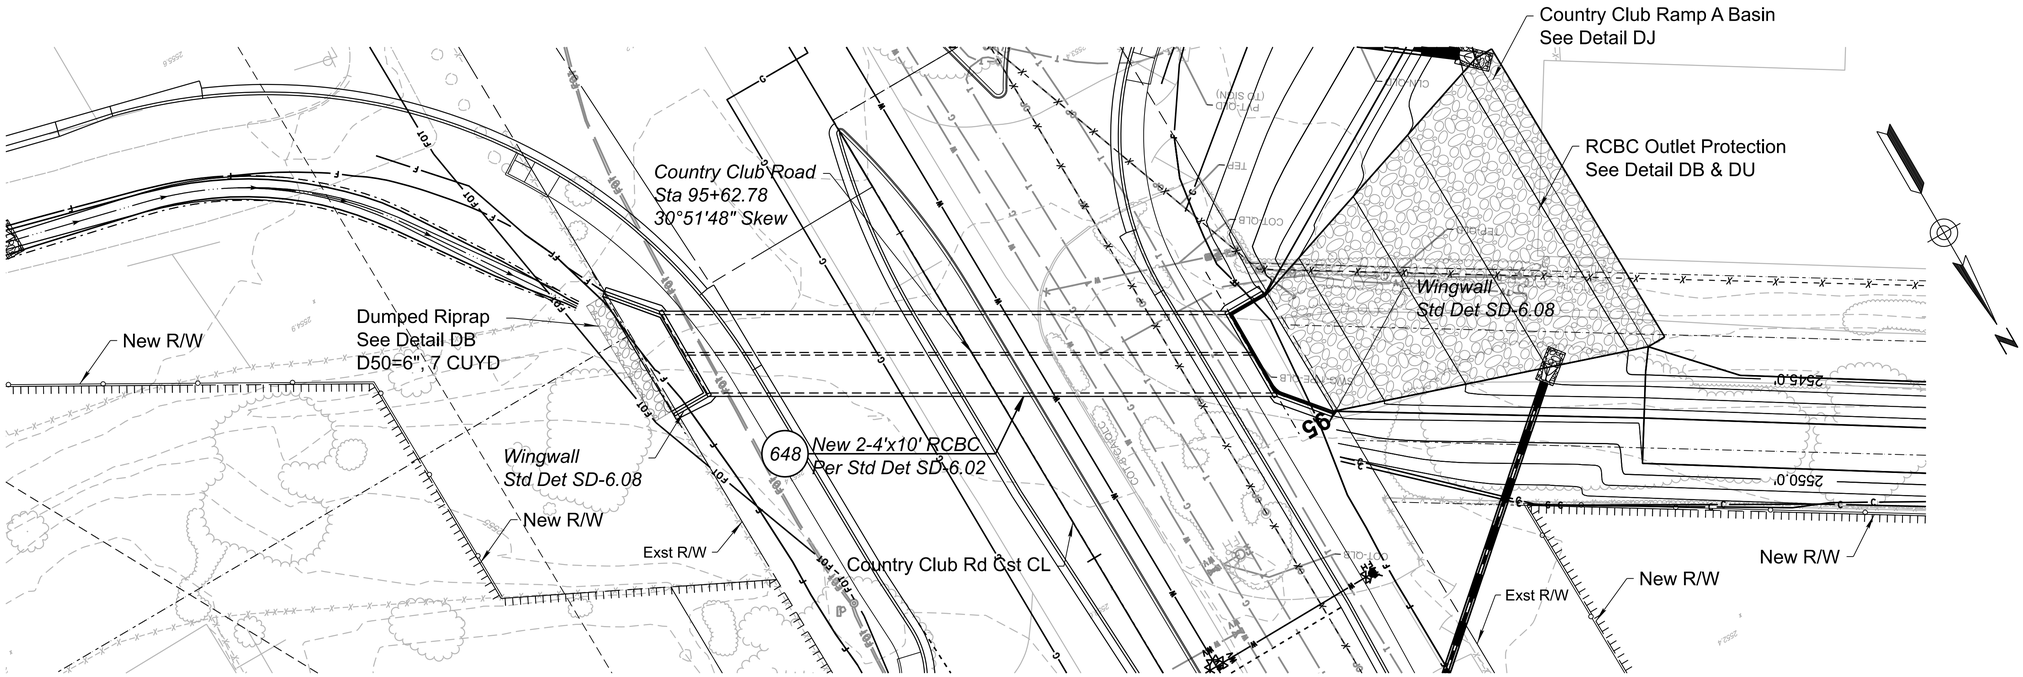

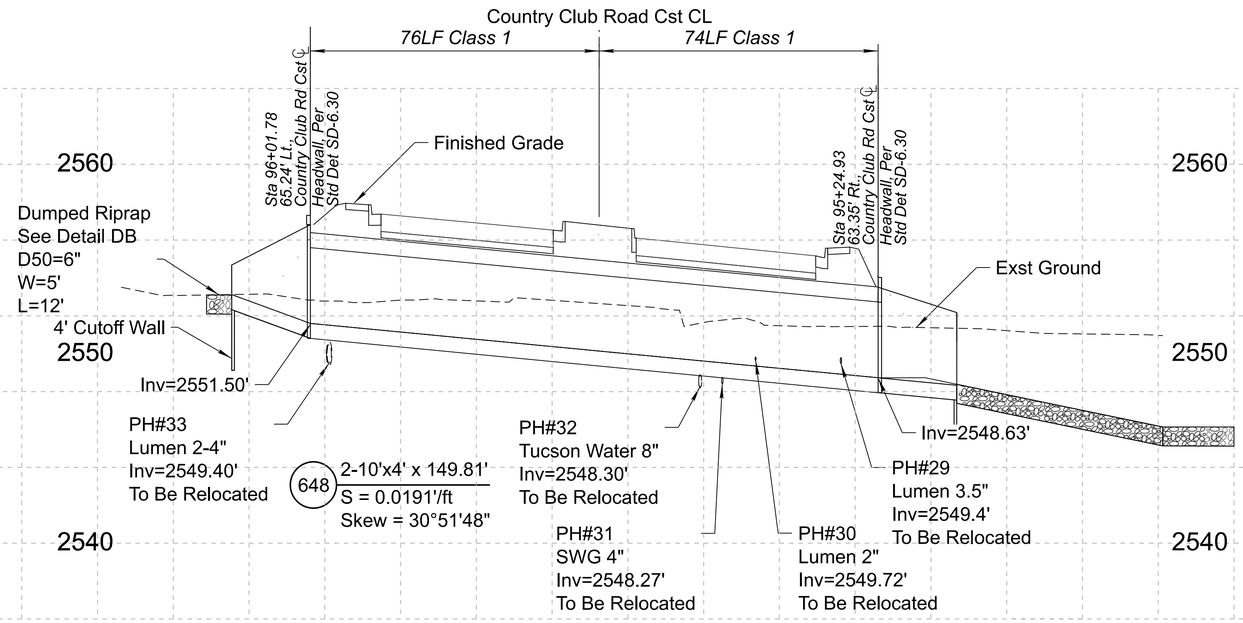

Registered Professional Engineer (Civil) CERTIFICATE NO. 65939 TIMOTHY MAHON Date Signed ARIZONA, U.S.A.

	NAME	DATE
DESIGN	J. FLINT	8/25
DRAWN	L. BREINING	8/25
CHECKED	T. MAHON	8/25

SUNDT AZTEC TYPSA

ARIZONA DEPARTMENT OF TRANSPORTATION
INFRASTRUCTURE DELIVERY AND OPERATIONS DIVISION
ROADWAY DESIGN SECTION
COUNTRY CLUB ROAD STA 95+62.78
NEW BOX CULVERT
PLAN AND PROFILE SHEET

ROUTE I-10 | MILEPOST | STRUCTURE NO.

F.H.W.A. Arizona Division	STATE	PROJECT NO.	FEDERAL ID NO.	SHEET NO.	TOTAL SHEETS	RECORD DRAWING
	ARIZ.	010 PM 262	010-E(232)S			

LOCATION: I-10 COUNTRY CLUB RD AND KINO PKWY TIS

DWG NO. D-02.28

TRACS NO. F0548 01C

ADOT

____ OF ____