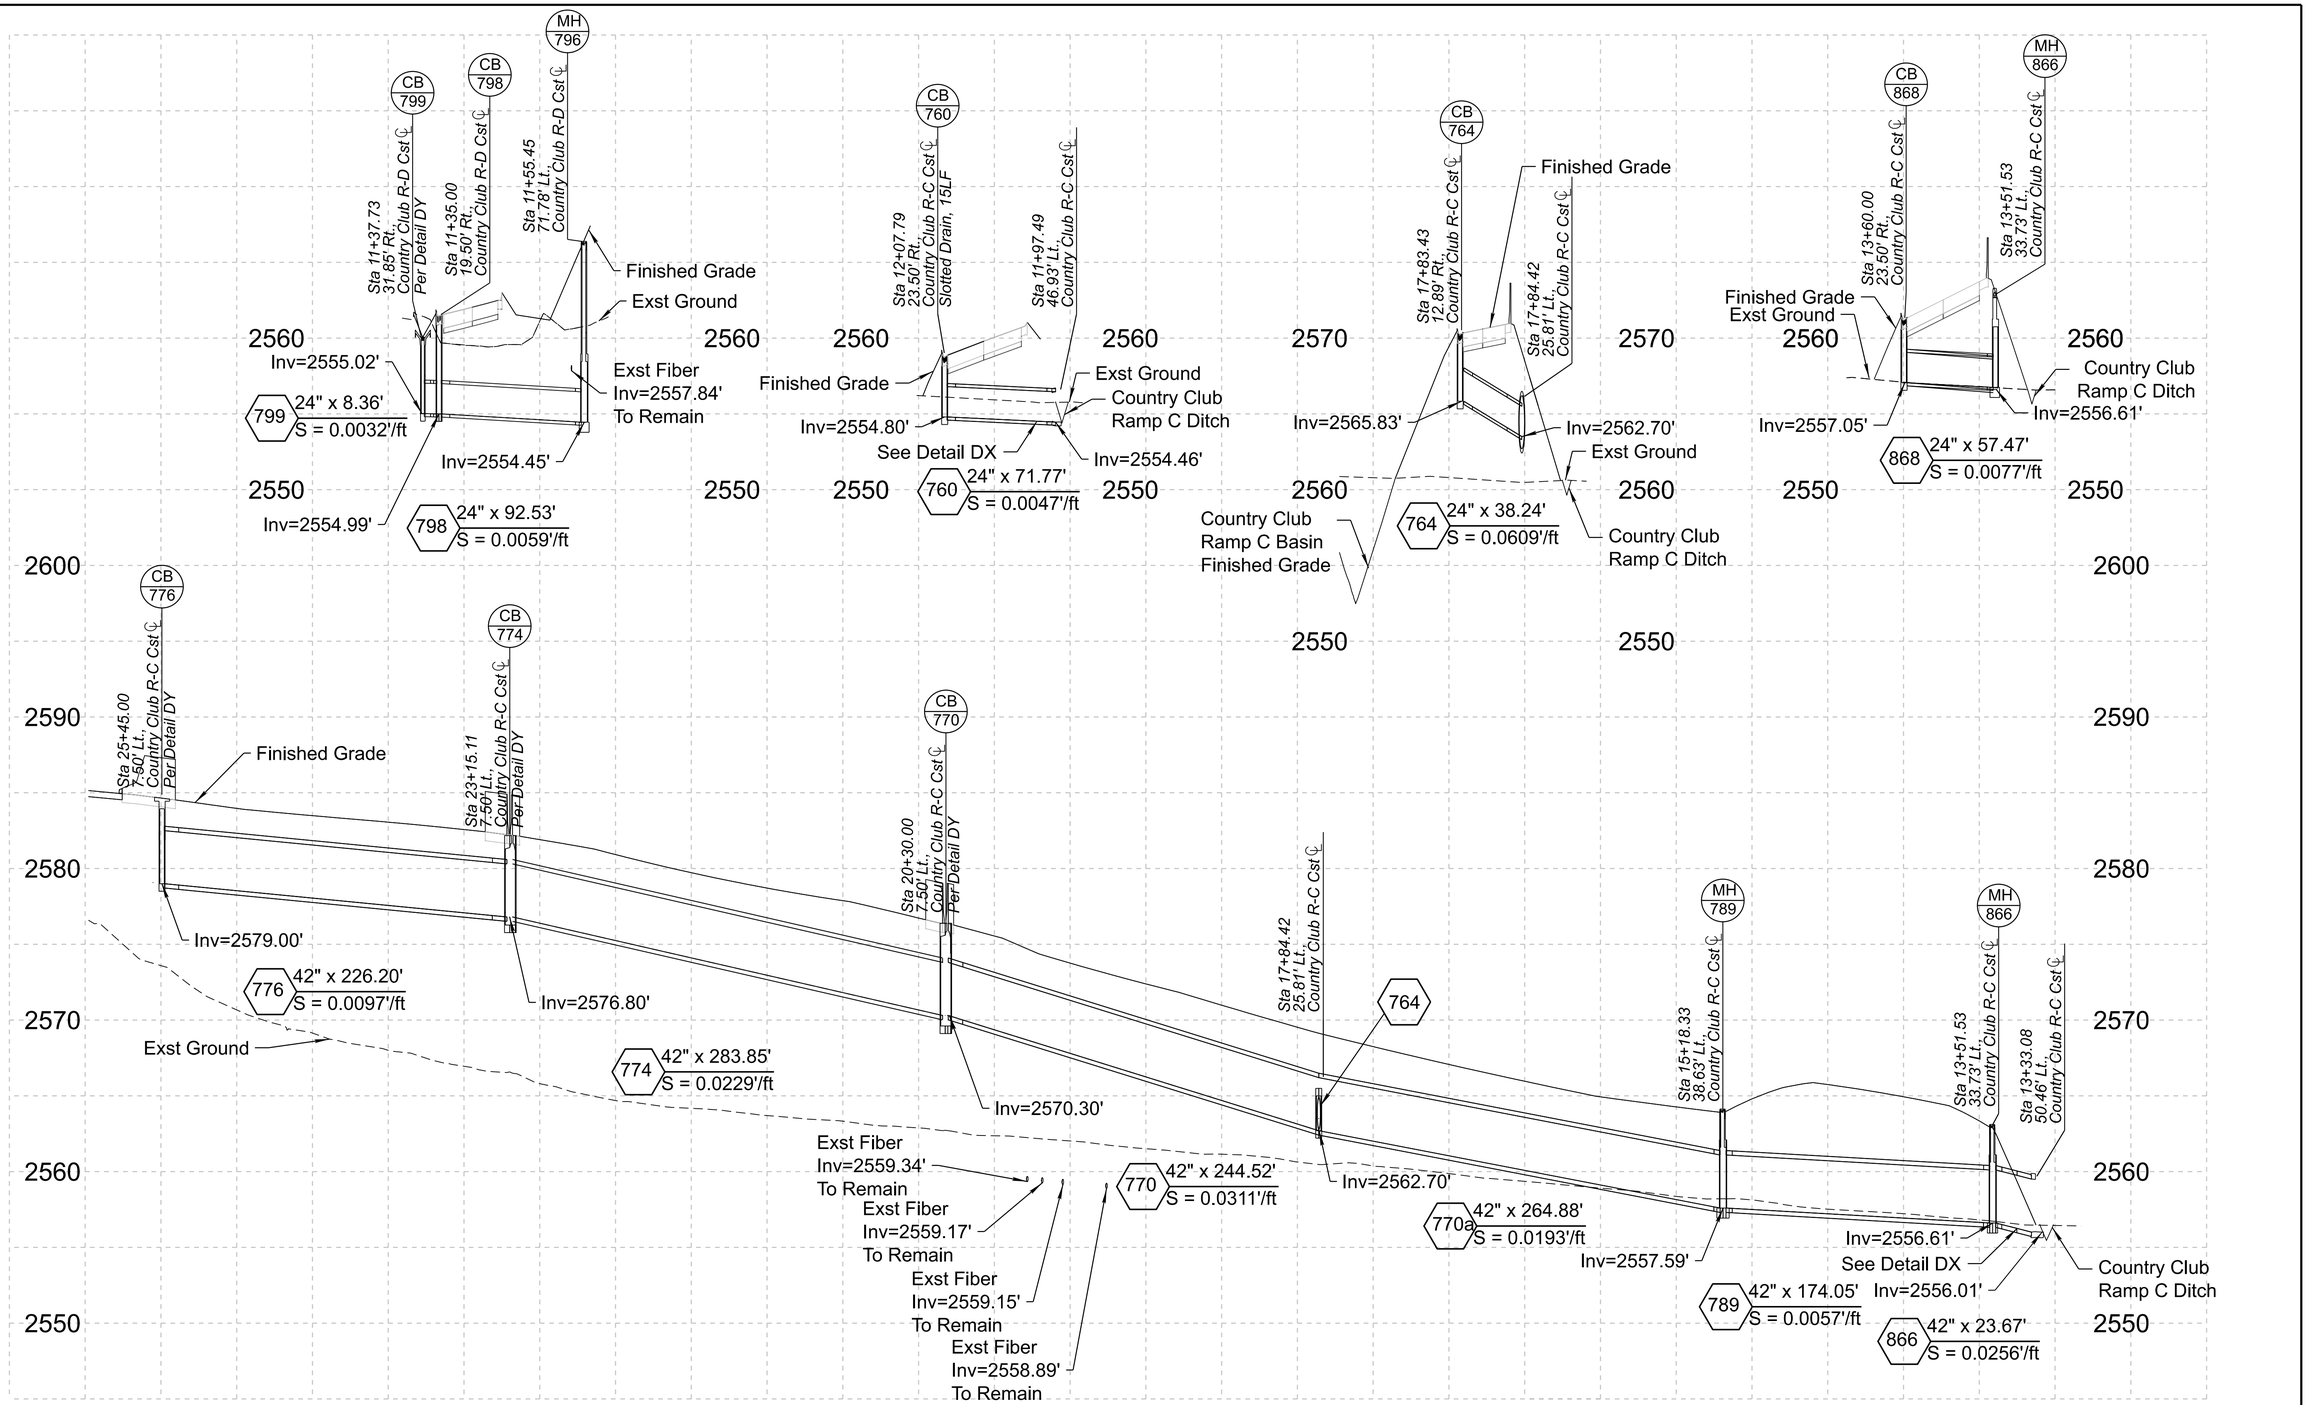


| NO. | DESCRIPTION OF REVISIONS | BY | DATE |
|---|---|---|---|
| 0 | RFC RELEASE | TM | 08/18/25 |

Registered Professional Engineer (Civil) CERTIFICATE NO. 65939 TIMOTHY MAHON Date Signed ARIZONA, U.S.A.

| | NAME | DATE |
|---|---|---|
| DESIGN | J. FLINT | 9/25 |
| DRAWN | L. BREINING | 9/25 |
| CHECKED | T. MAHON | 9/25 |

SUNDT AZTEC TYPSA

ARIZONA DEPARTMENT OF TRANSPORTATION
INFRASTRUCTURE DELIVERY AND OPERATIONS DIVISION
ROADWAY DESIGN SECTION

DRAINAGE PROFILE SHEET

ROUTE I-10
MILEPOST
STRUCTURE NO.

F.H.W.A. Arizona Division

| STATE | PROJECT NO. | FEDERAL ID NO. | SHEET NO. | TOTAL SHEETS | RECORD DRAWING |
|---|---|---|---|---|---|
| ARIZ. | 010 PM 262 | 010-E(232)S | | | |

LOCATION I-10 COUNTRY CLUB RD AND KINO PKWY TIS

DWG NO. D-02.24

TRACS NO. F0548 01C

ADOT

____ OF ____