


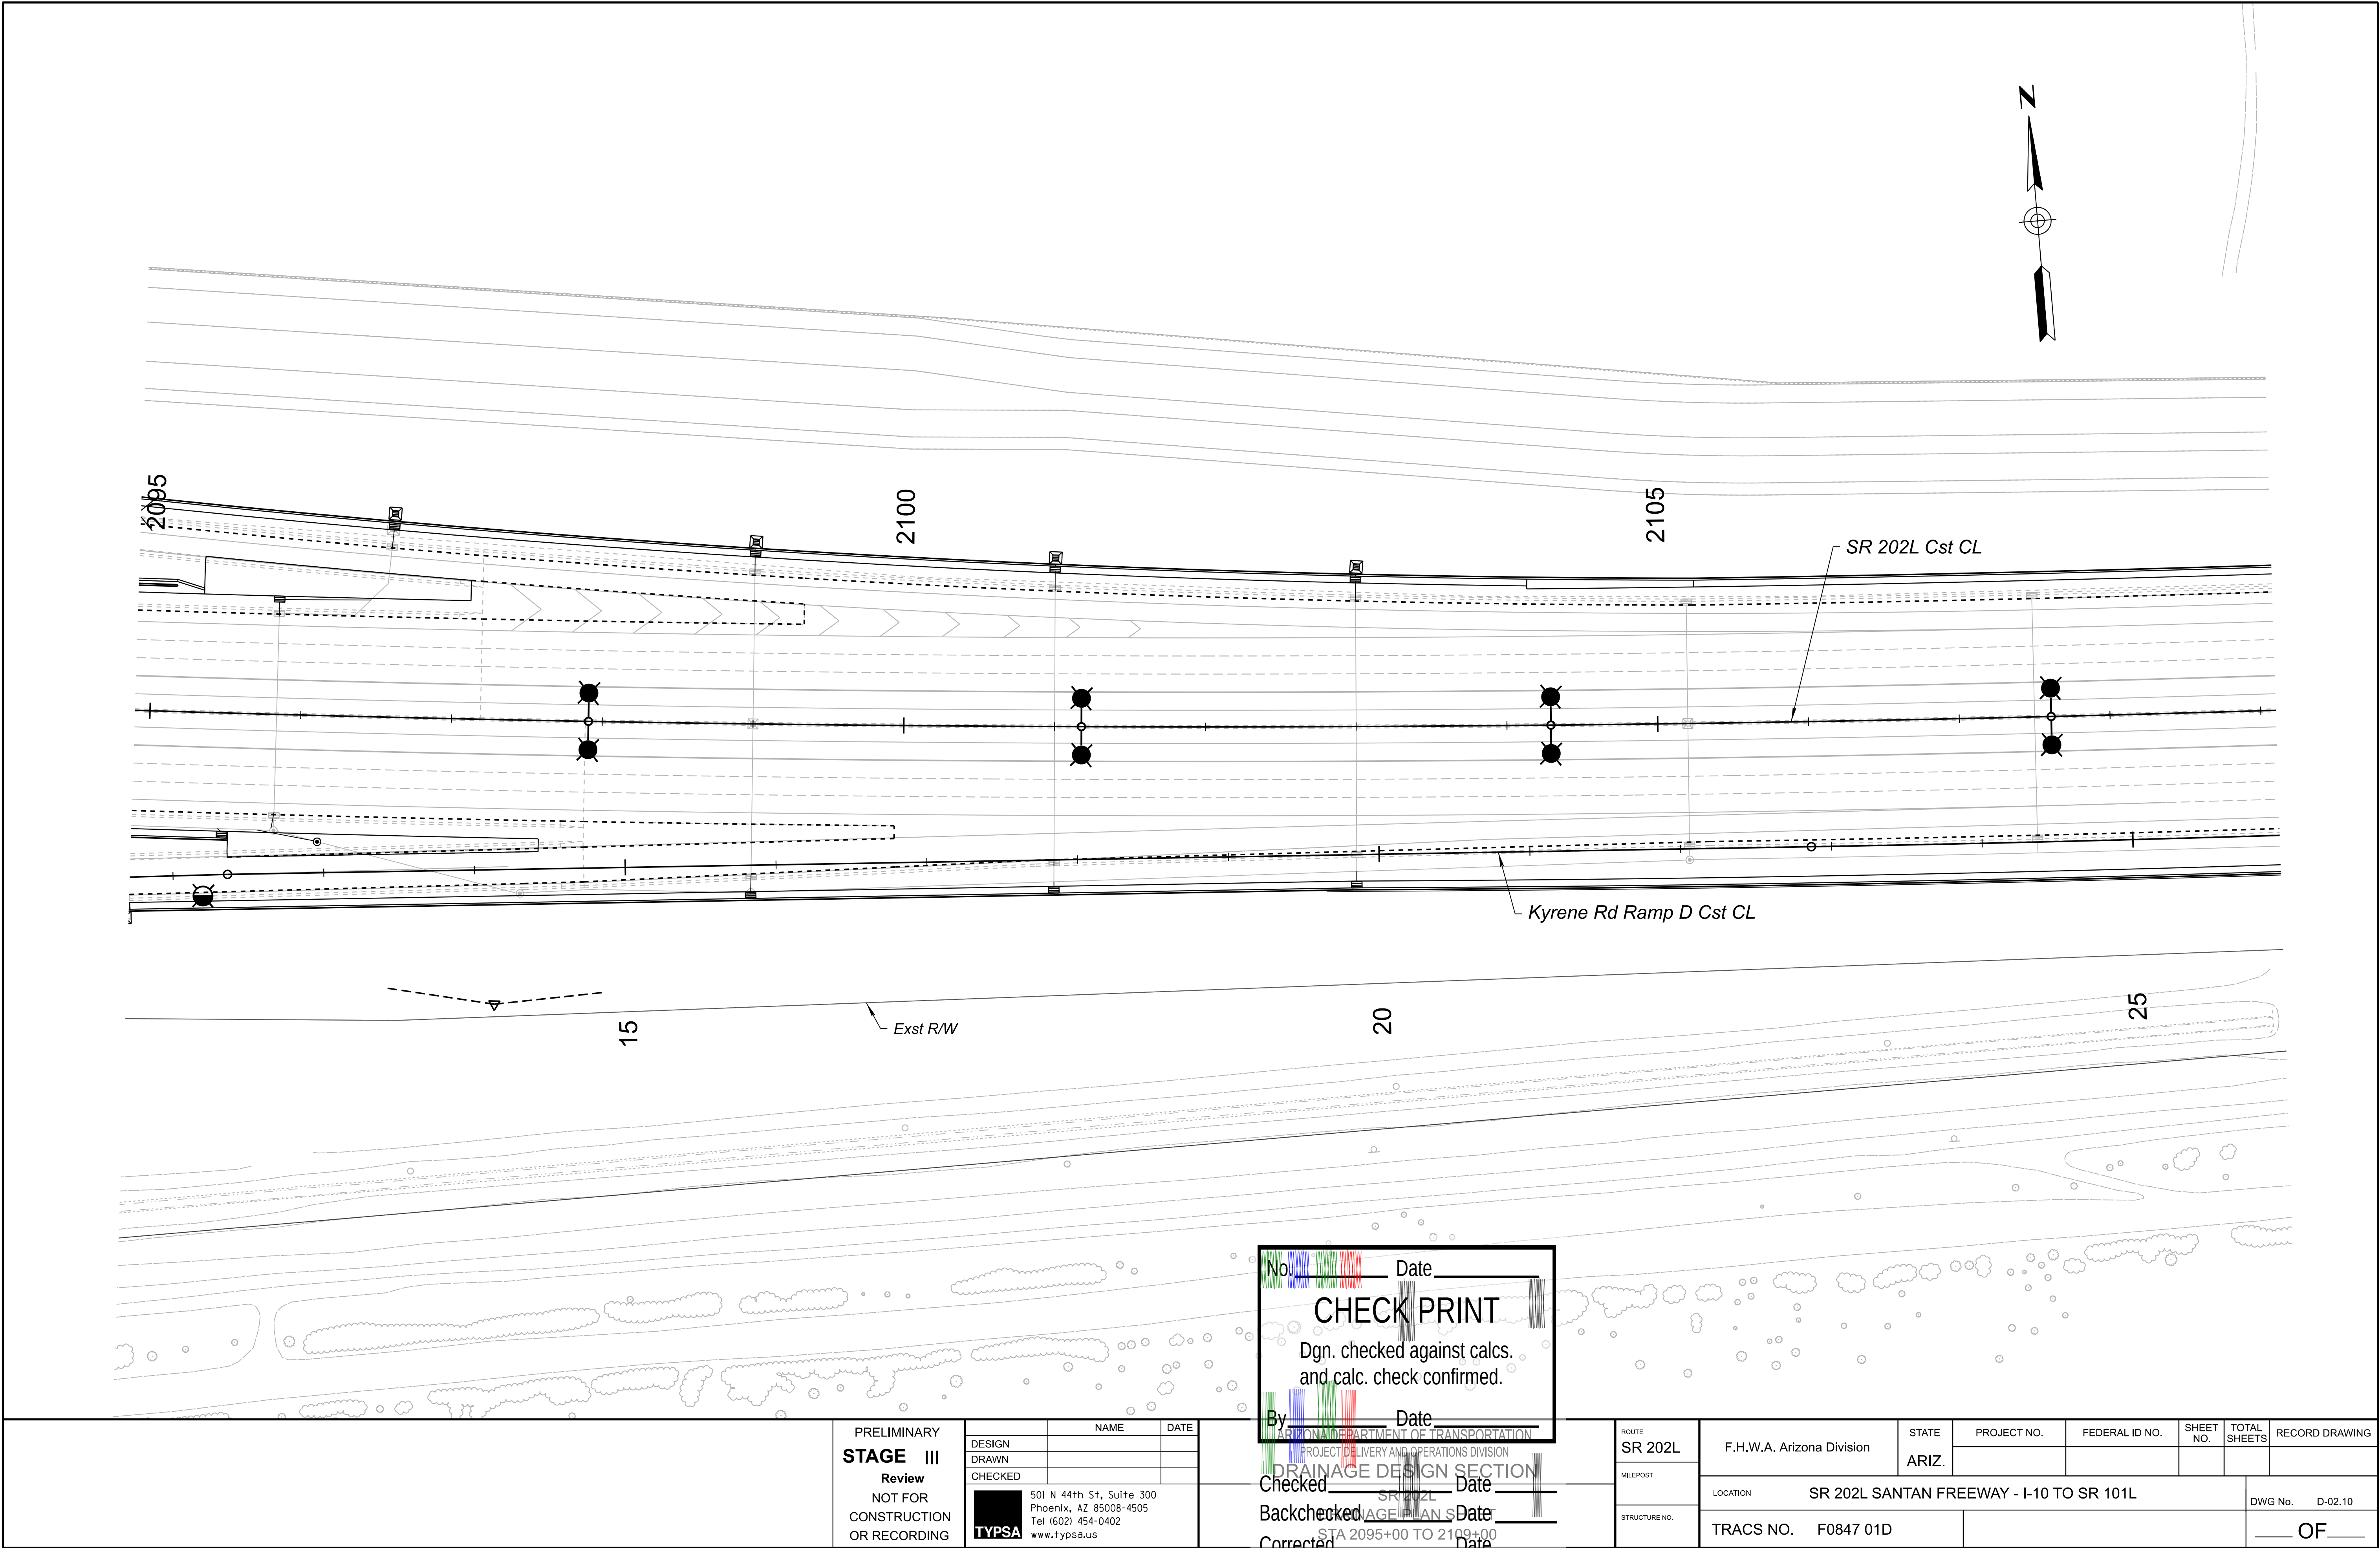

PRELIMINARY STAGE III Review NOT FOR CONSTRUCTION OR RECORDING	DESIGN	NAME	DATE	ARIZONA DEPARTMENT OF TRANSPORTATION PROJECT DELIVERY AND OPERATIONS DIVISION DRAINAGE DESIGN SECTION By _____ Date _____ Checked _____ Date _____ Backchecked _____ Date _____ Corrected _____ Date _____ Verified _____ Date _____	ROUTE	SR 202L	F.H.W.A. Arizona Division	STATE	ARIZ.	PROJECT NO.		FEDERAL ID NO.		SHEET NO.		TOTAL SHEETS		RECORD DRAWING	
	DRAWN				MILEPOST		LOCATION SR 202L SANTAN FREEWAY - I-10 TO SR 101L										DWG No.	D-02.10	
	CHECKED				STRUCTURE NO.		TRACS NO. F0847 01D										OF		

501 N 44th St, Suite 300
Phoenix, AZ 85008-4505
Tel (602) 454-0402
www.typpsa.us

TYPPSA