


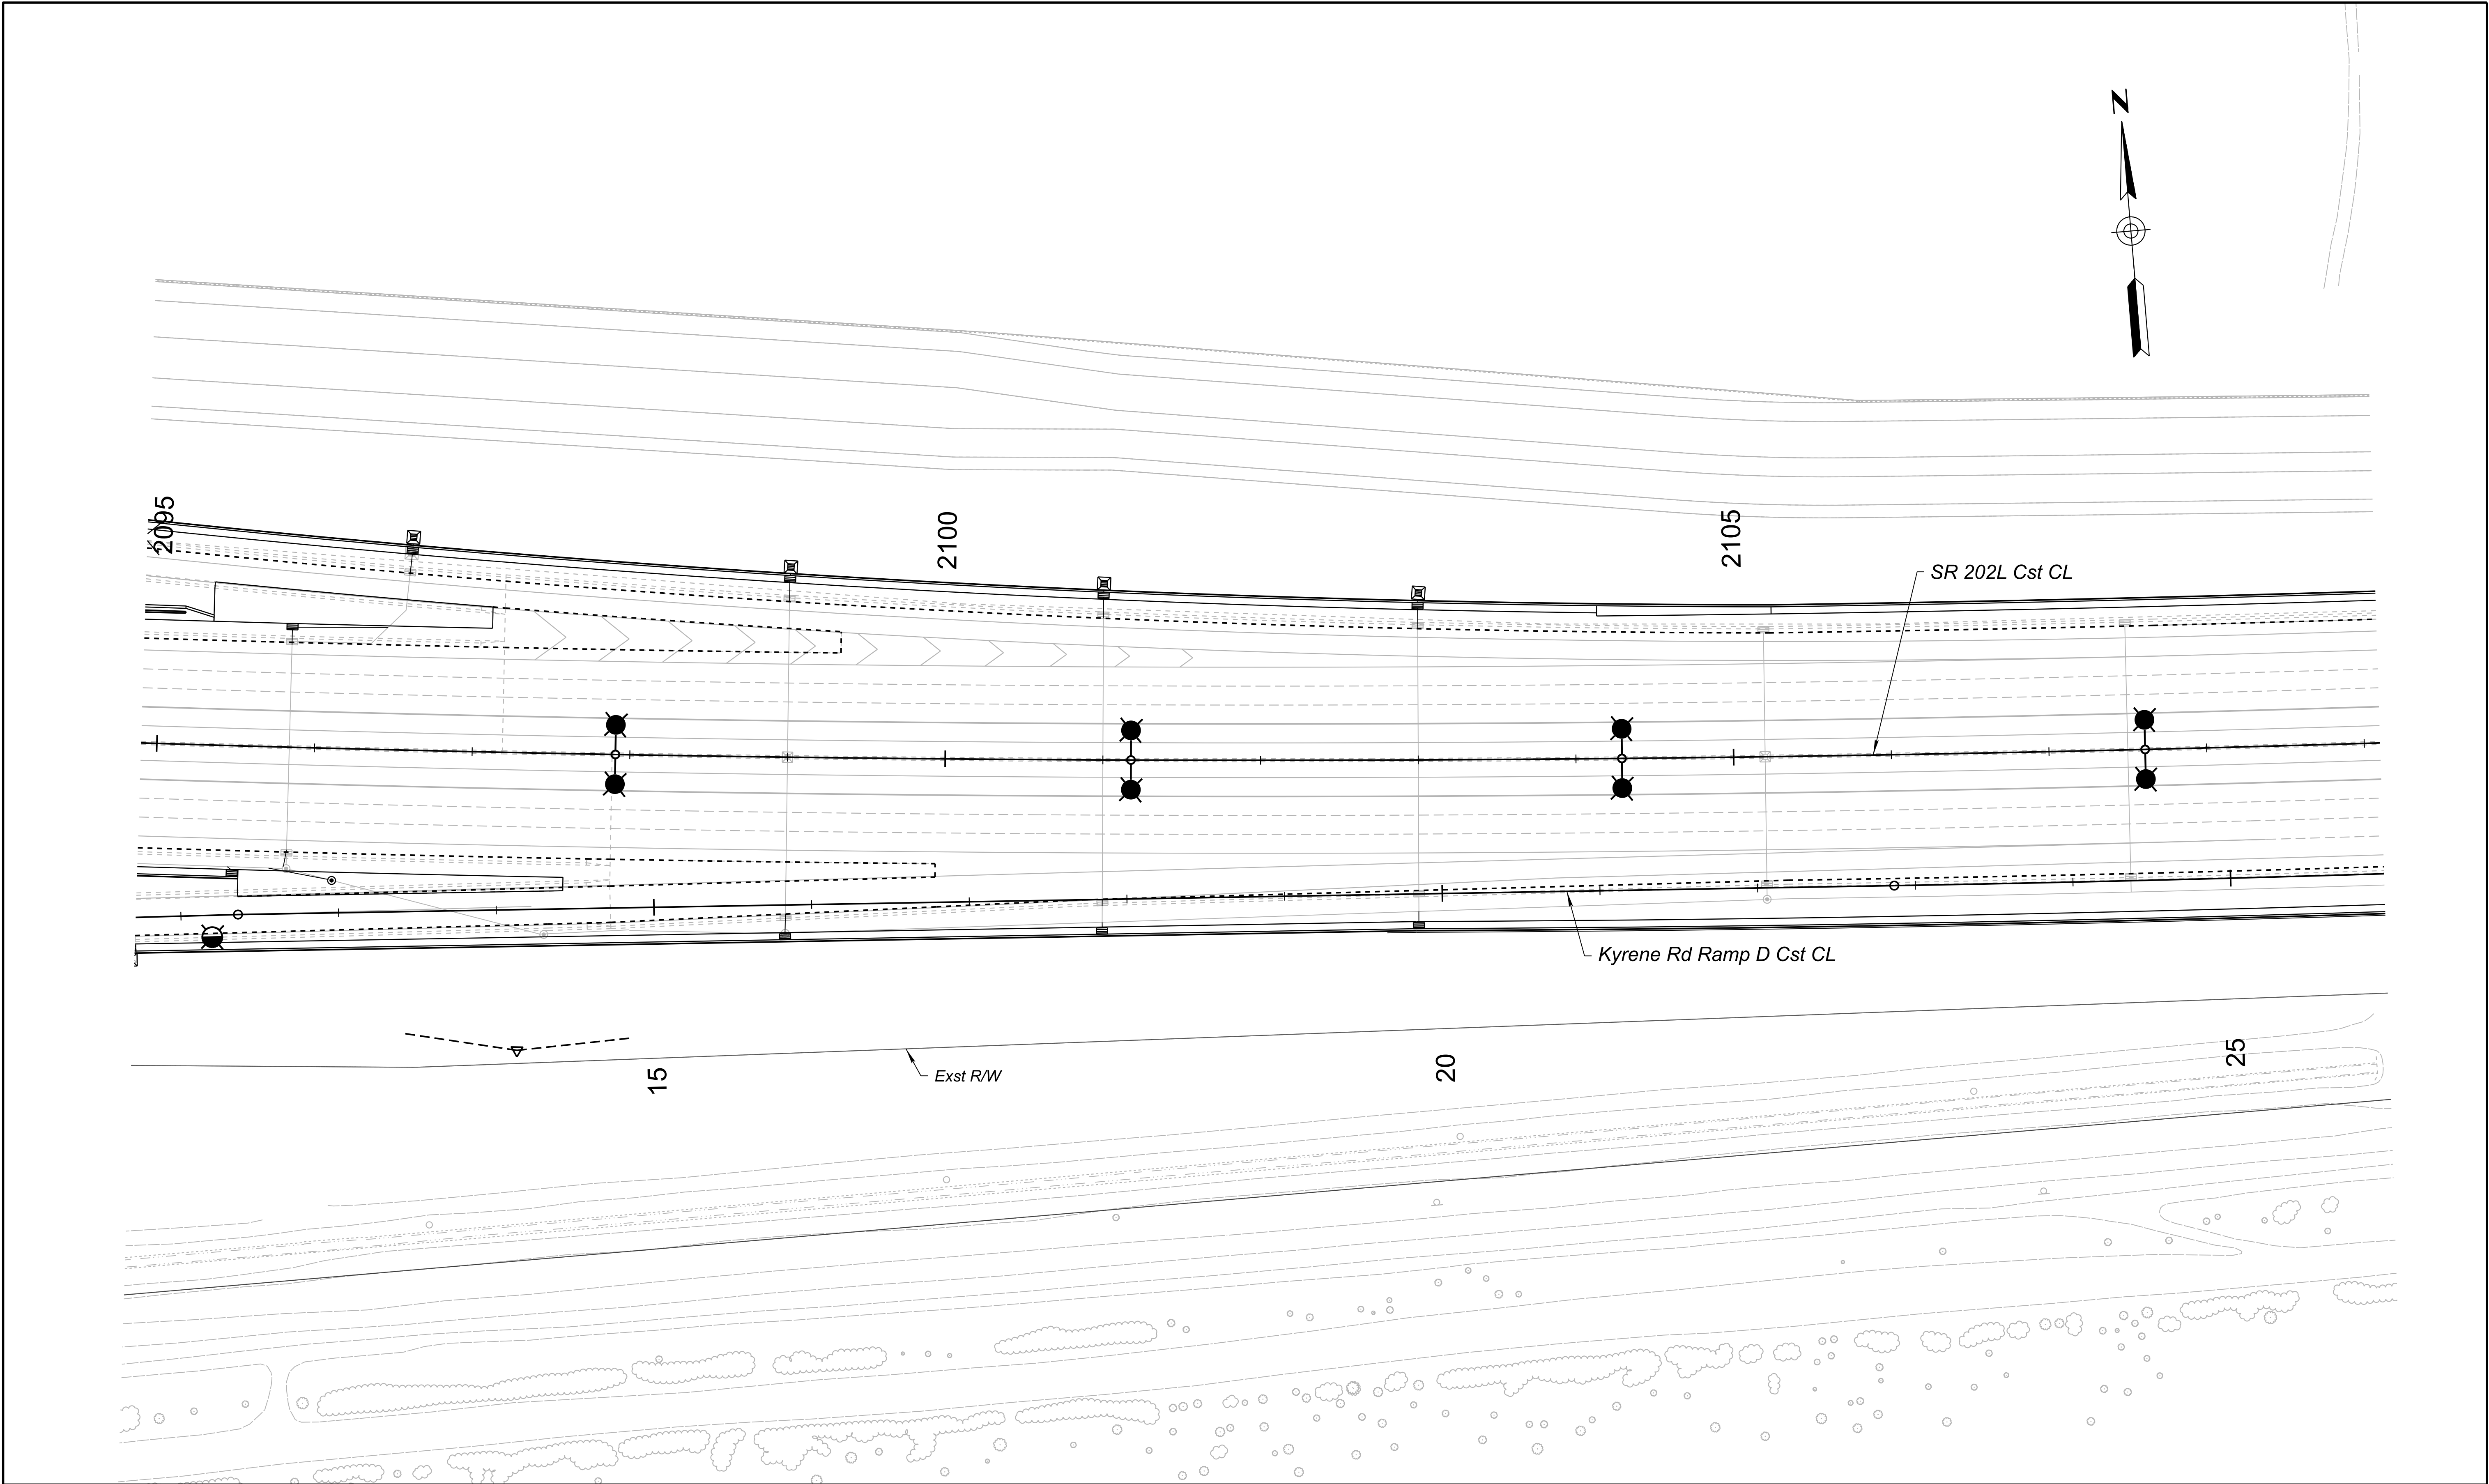

	PRELIMINARY STAGE III Review NOT FOR CONSTRUCTION OR RECORDING		NAME	DATE	ARIZONA DEPARTMENT OF TRANSPORTATION PROJECT DELIVERY AND OPERATIONS DIVISION DRAINAGE DESIGN SECTION	ROUTE	F.H.W.A. Arizona Division	STATE ARIZ.	PROJECT NO.	FEDERAL ID NO.	SHEET NO.	TOTAL SHEETS	RECORD DRAWING	
		DESIGN				SR 202L								
		DRAWN												
		CHECKED												
			501 N 44th St, Suite 300 Phoenix, AZ 85008-4505 Tel (602) 454-0402 TYP SA www.typsa.us	SR 202L DRAINAGE PLAN SHEET STA 2095+00 TO 2109+00					MILEPOST	LOCATION SR 202L SANTAN FREEWAY - I-10 TO SR 101L				DWG No. D-02.10
						STRUCTURE NO.	TRACS NO. F0847 01D				___ OF ___			