


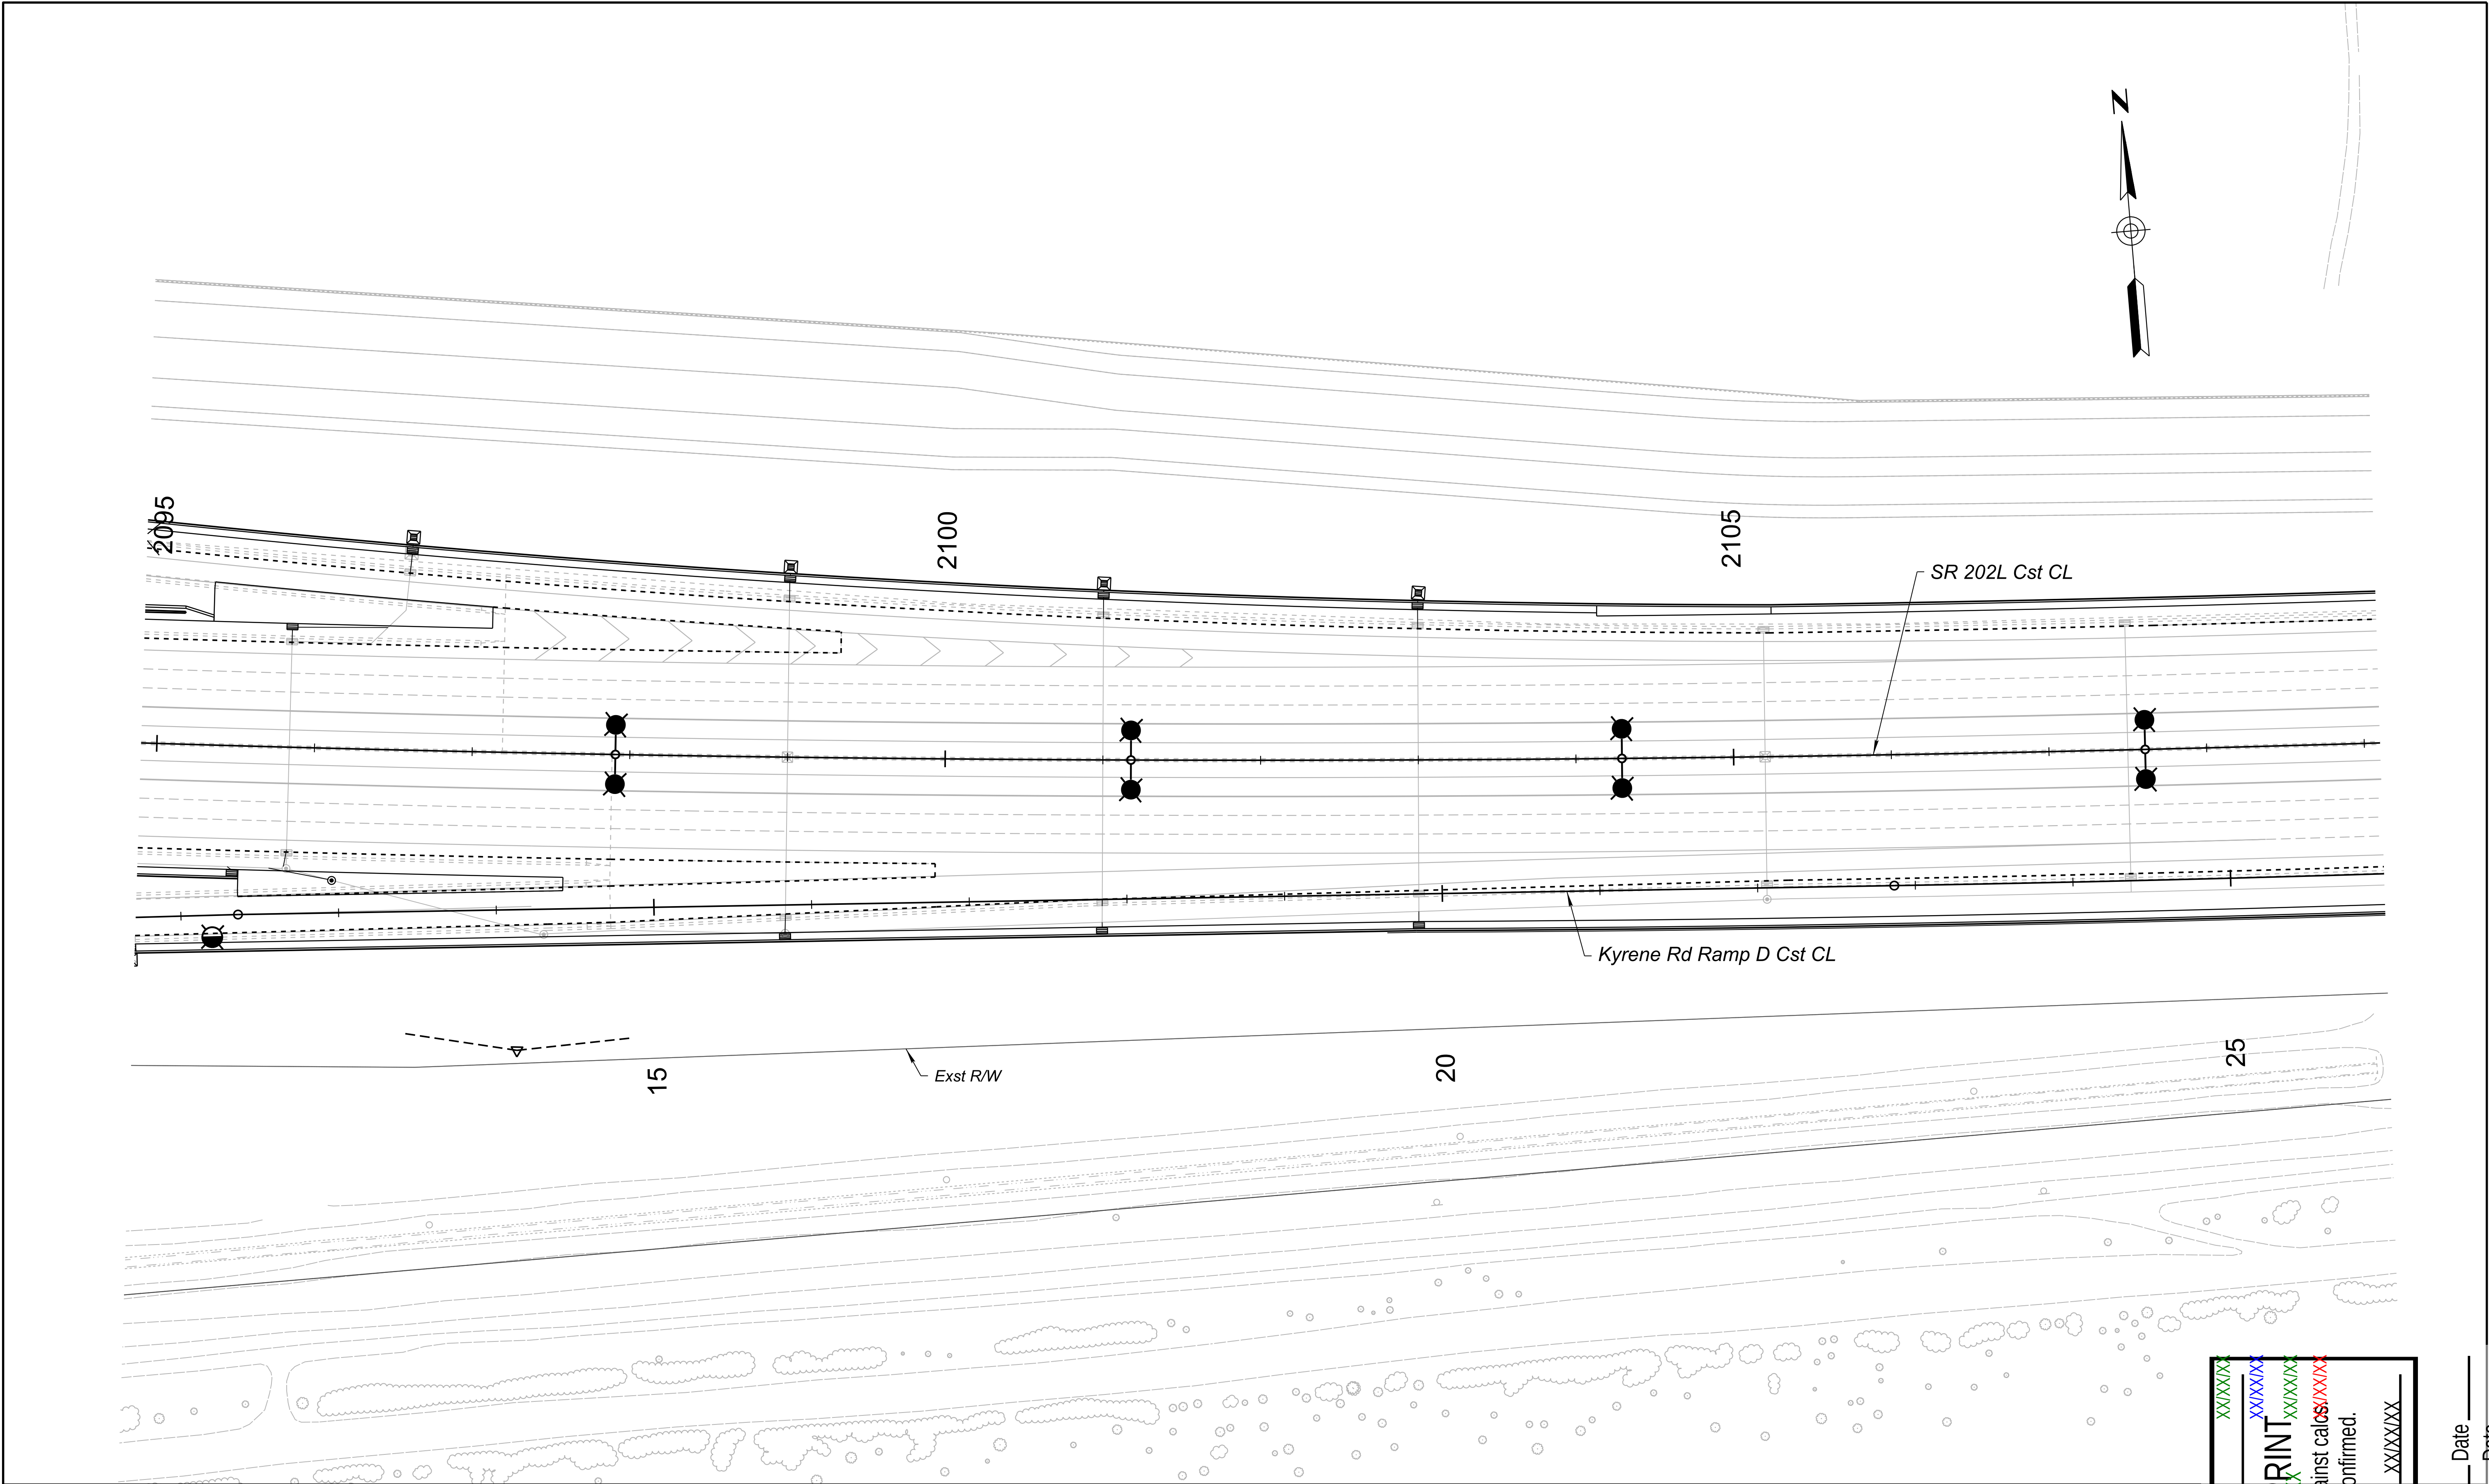

PRELIMINARY STAGE III Review NOT FOR CONSTRUCTION OR RECORDING	DESIGN	NAME	DATE	ARIZONA DEPARTMENT OF TRANSPORTATION PROJECT DELIVERY AND OPERATIONS DIVISION DRAINAGE DESIGN SECTION SR 202L DRAINAGE PLAN SHEET STA 2095+00 TO 2109+00	ROUTE	F.H.W.A. Arizona Division	STATE	PROJECT NO.	FEDERAL AID NO.
	DRAWN				MILEPOST	LOCATION	ARIZ.		
	CHECKED				STRUCTURE NO.	TRACS NO.			
	501 N 44th St, Suite 300 Phoenix, AZ 85008-4505 Tel (602) 454-0402 www.typpsa.us				SR 202L SANTAN FREEWAY - I-10 TO SR 101				

No. X XXXXX Date X XXXXX

CHECKPRINT
Dgn checked against calcs and calc. check confirmed.
By X XXXXX Date X XXXXX

Checked X XXXXX Date X XXXXX
Backchecked X XXXXX Date X XXXXX
Corrected X XXXXX Date X XXXXX
Verified X XXXXX Date X XXXXX