
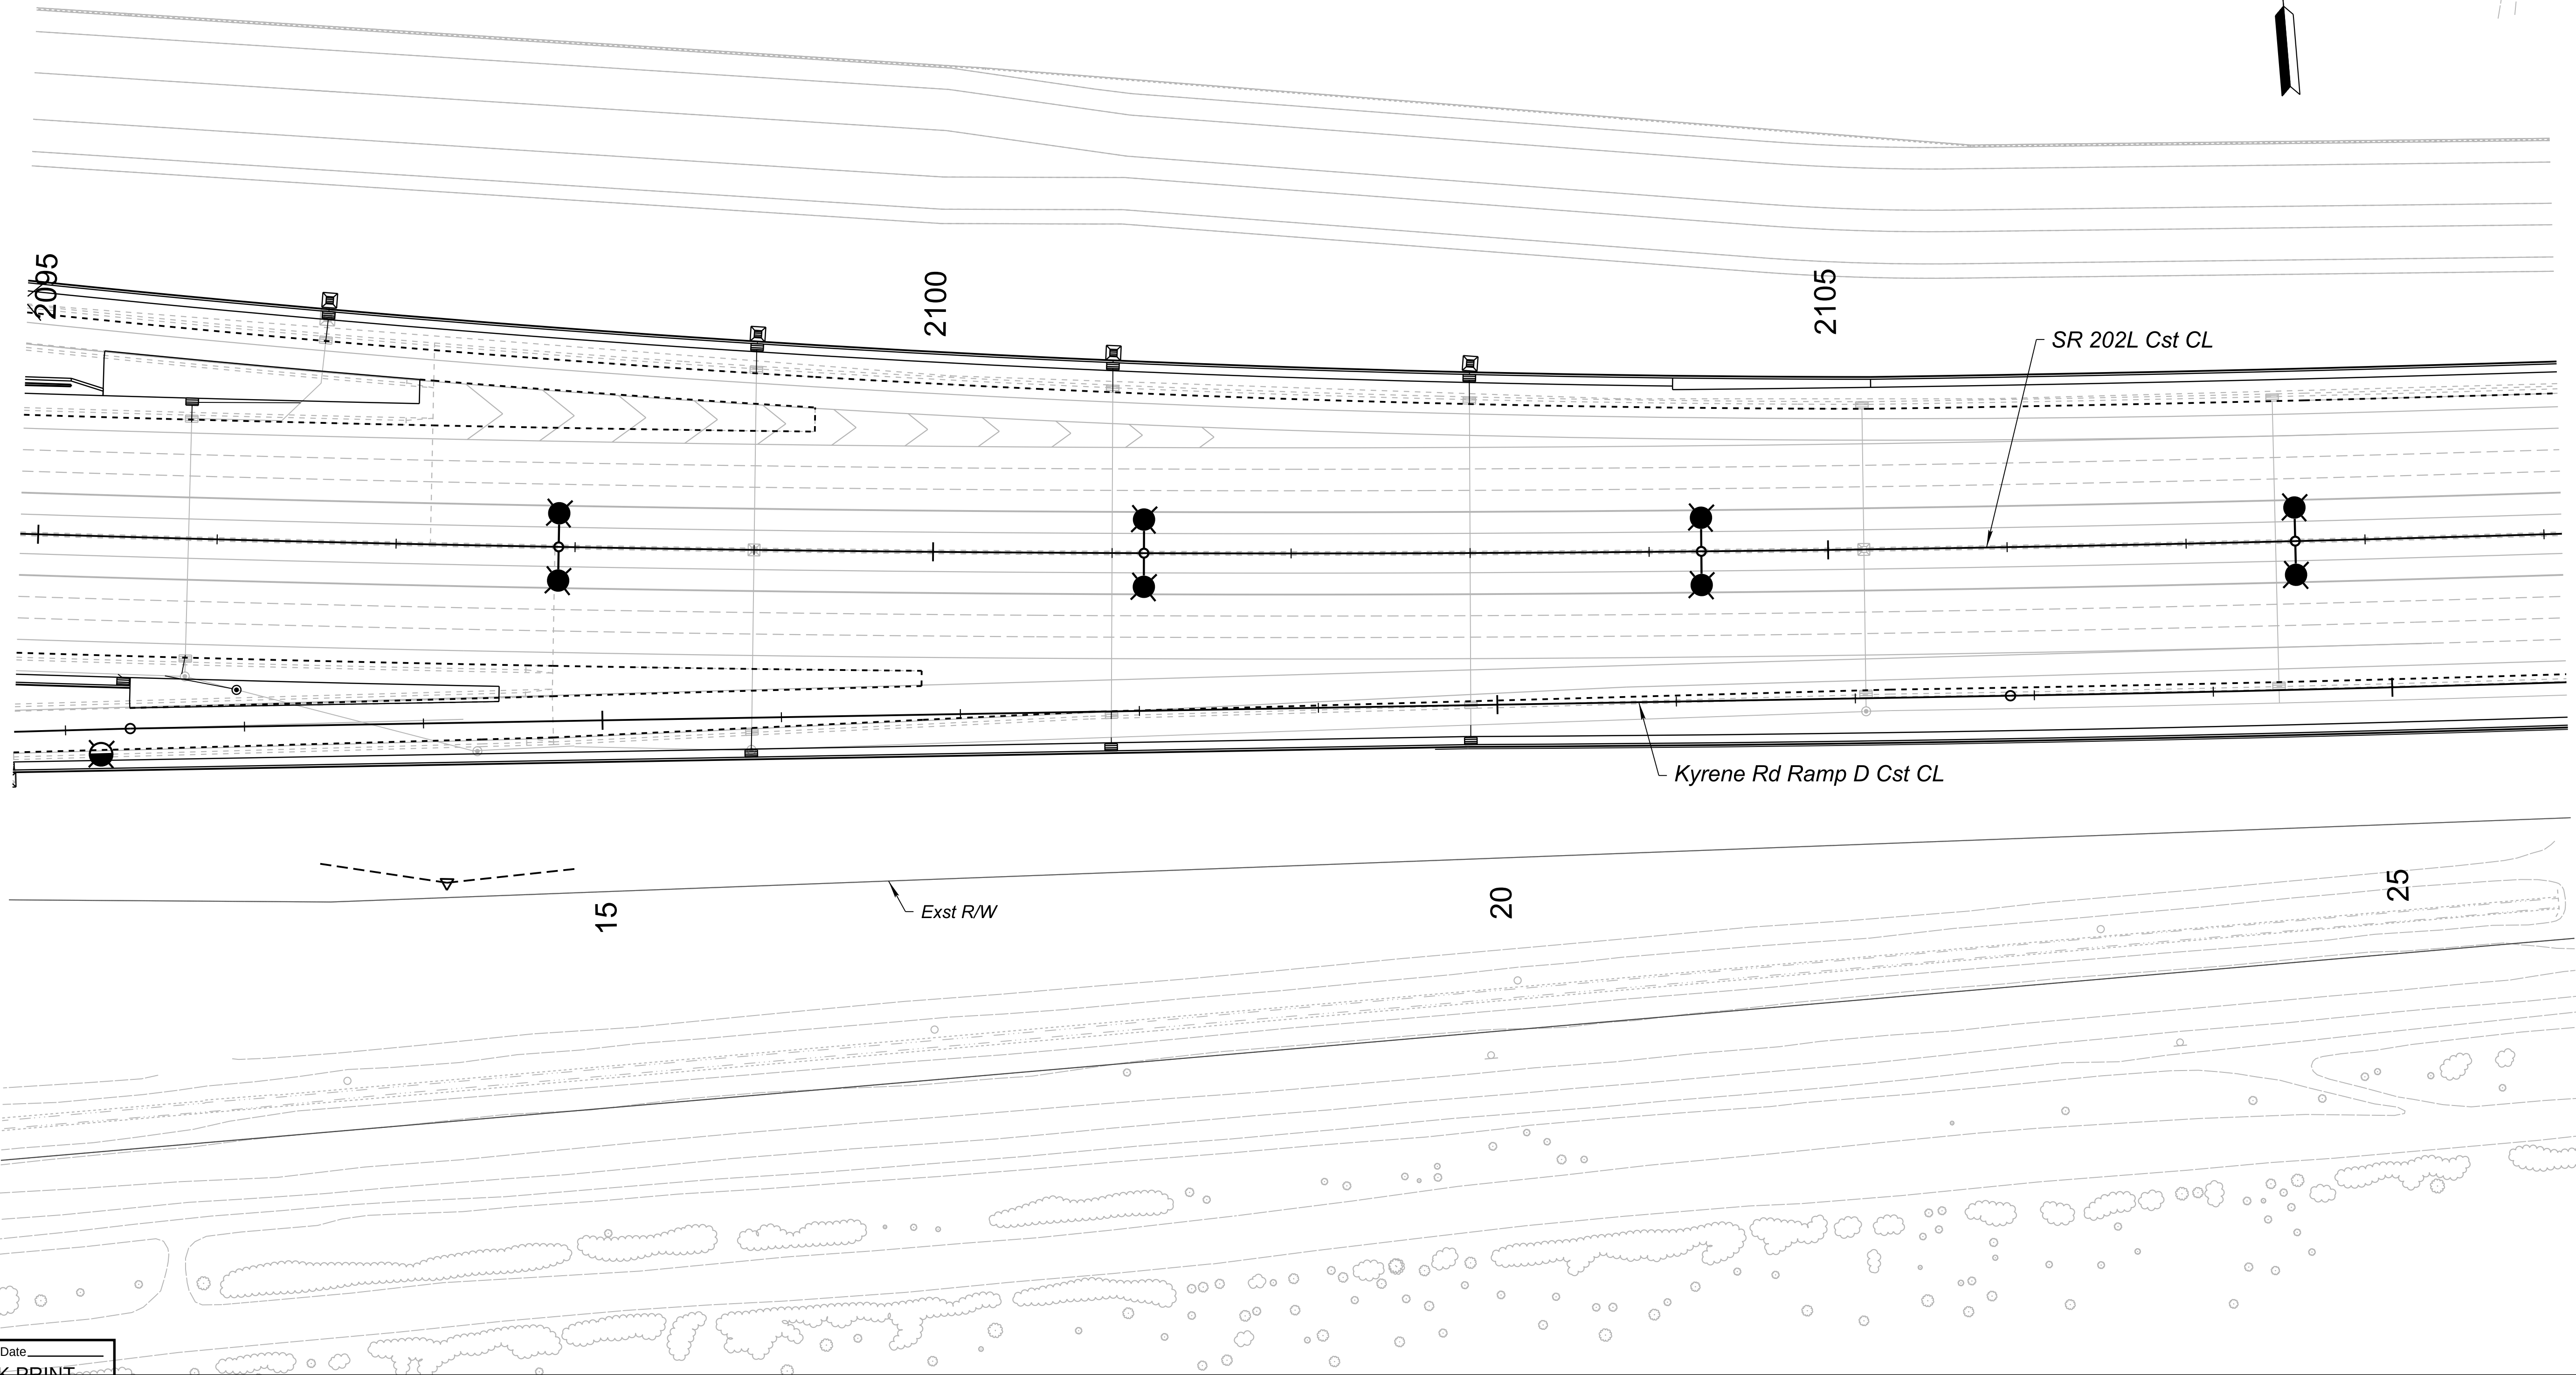


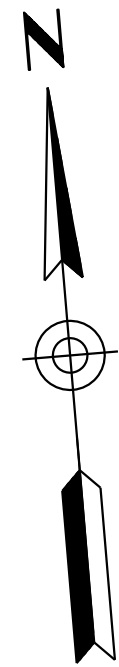

No. _____	Date _____
CHECK PRINT	
Dgn. checked against calcs. and calc. check confirmed.	
By _____	Date _____

Checked _____	Date _____
Backchecked _____	Date _____
Corrected _____	Date _____
Verified _____	Date _____

PRELIMINARY
STAGE III
Review
NOT FOR
CONSTRUCTION
OR RECORDING

DESIGN	NAME	DATE
DRAWN		
CHECKED		
	501 N 44th St, Suite 300 Phoenix, AZ 85008-4505 Tel (602) 454-0402 www.typsas.us	

ARIZONA DEPARTMENT OF TRANSPORTATION
PROJECT DELIVERY AND OPERATIONS DIVISION
DRAINAGE DESIGN SECTION
SR 202L
DRAINAGE PLAN SHEET
STA 2095+00 TO 2109+00

ROUTE
SR 202L
MILEPOST
STRUCTURE NO.

F.H.W.A. Arizona Division

STATE
ARIZ.

PROJECT NO.

FEDERAL ID NO.

SHEET NO.

TOTAL SHEETS

RECORD DRAWING

LOCATION SR 202L SANTAN FREEWAY - I-10 TO SR 101L

TRACS NO. F0847 01D

DWG No. D-02.10

OF