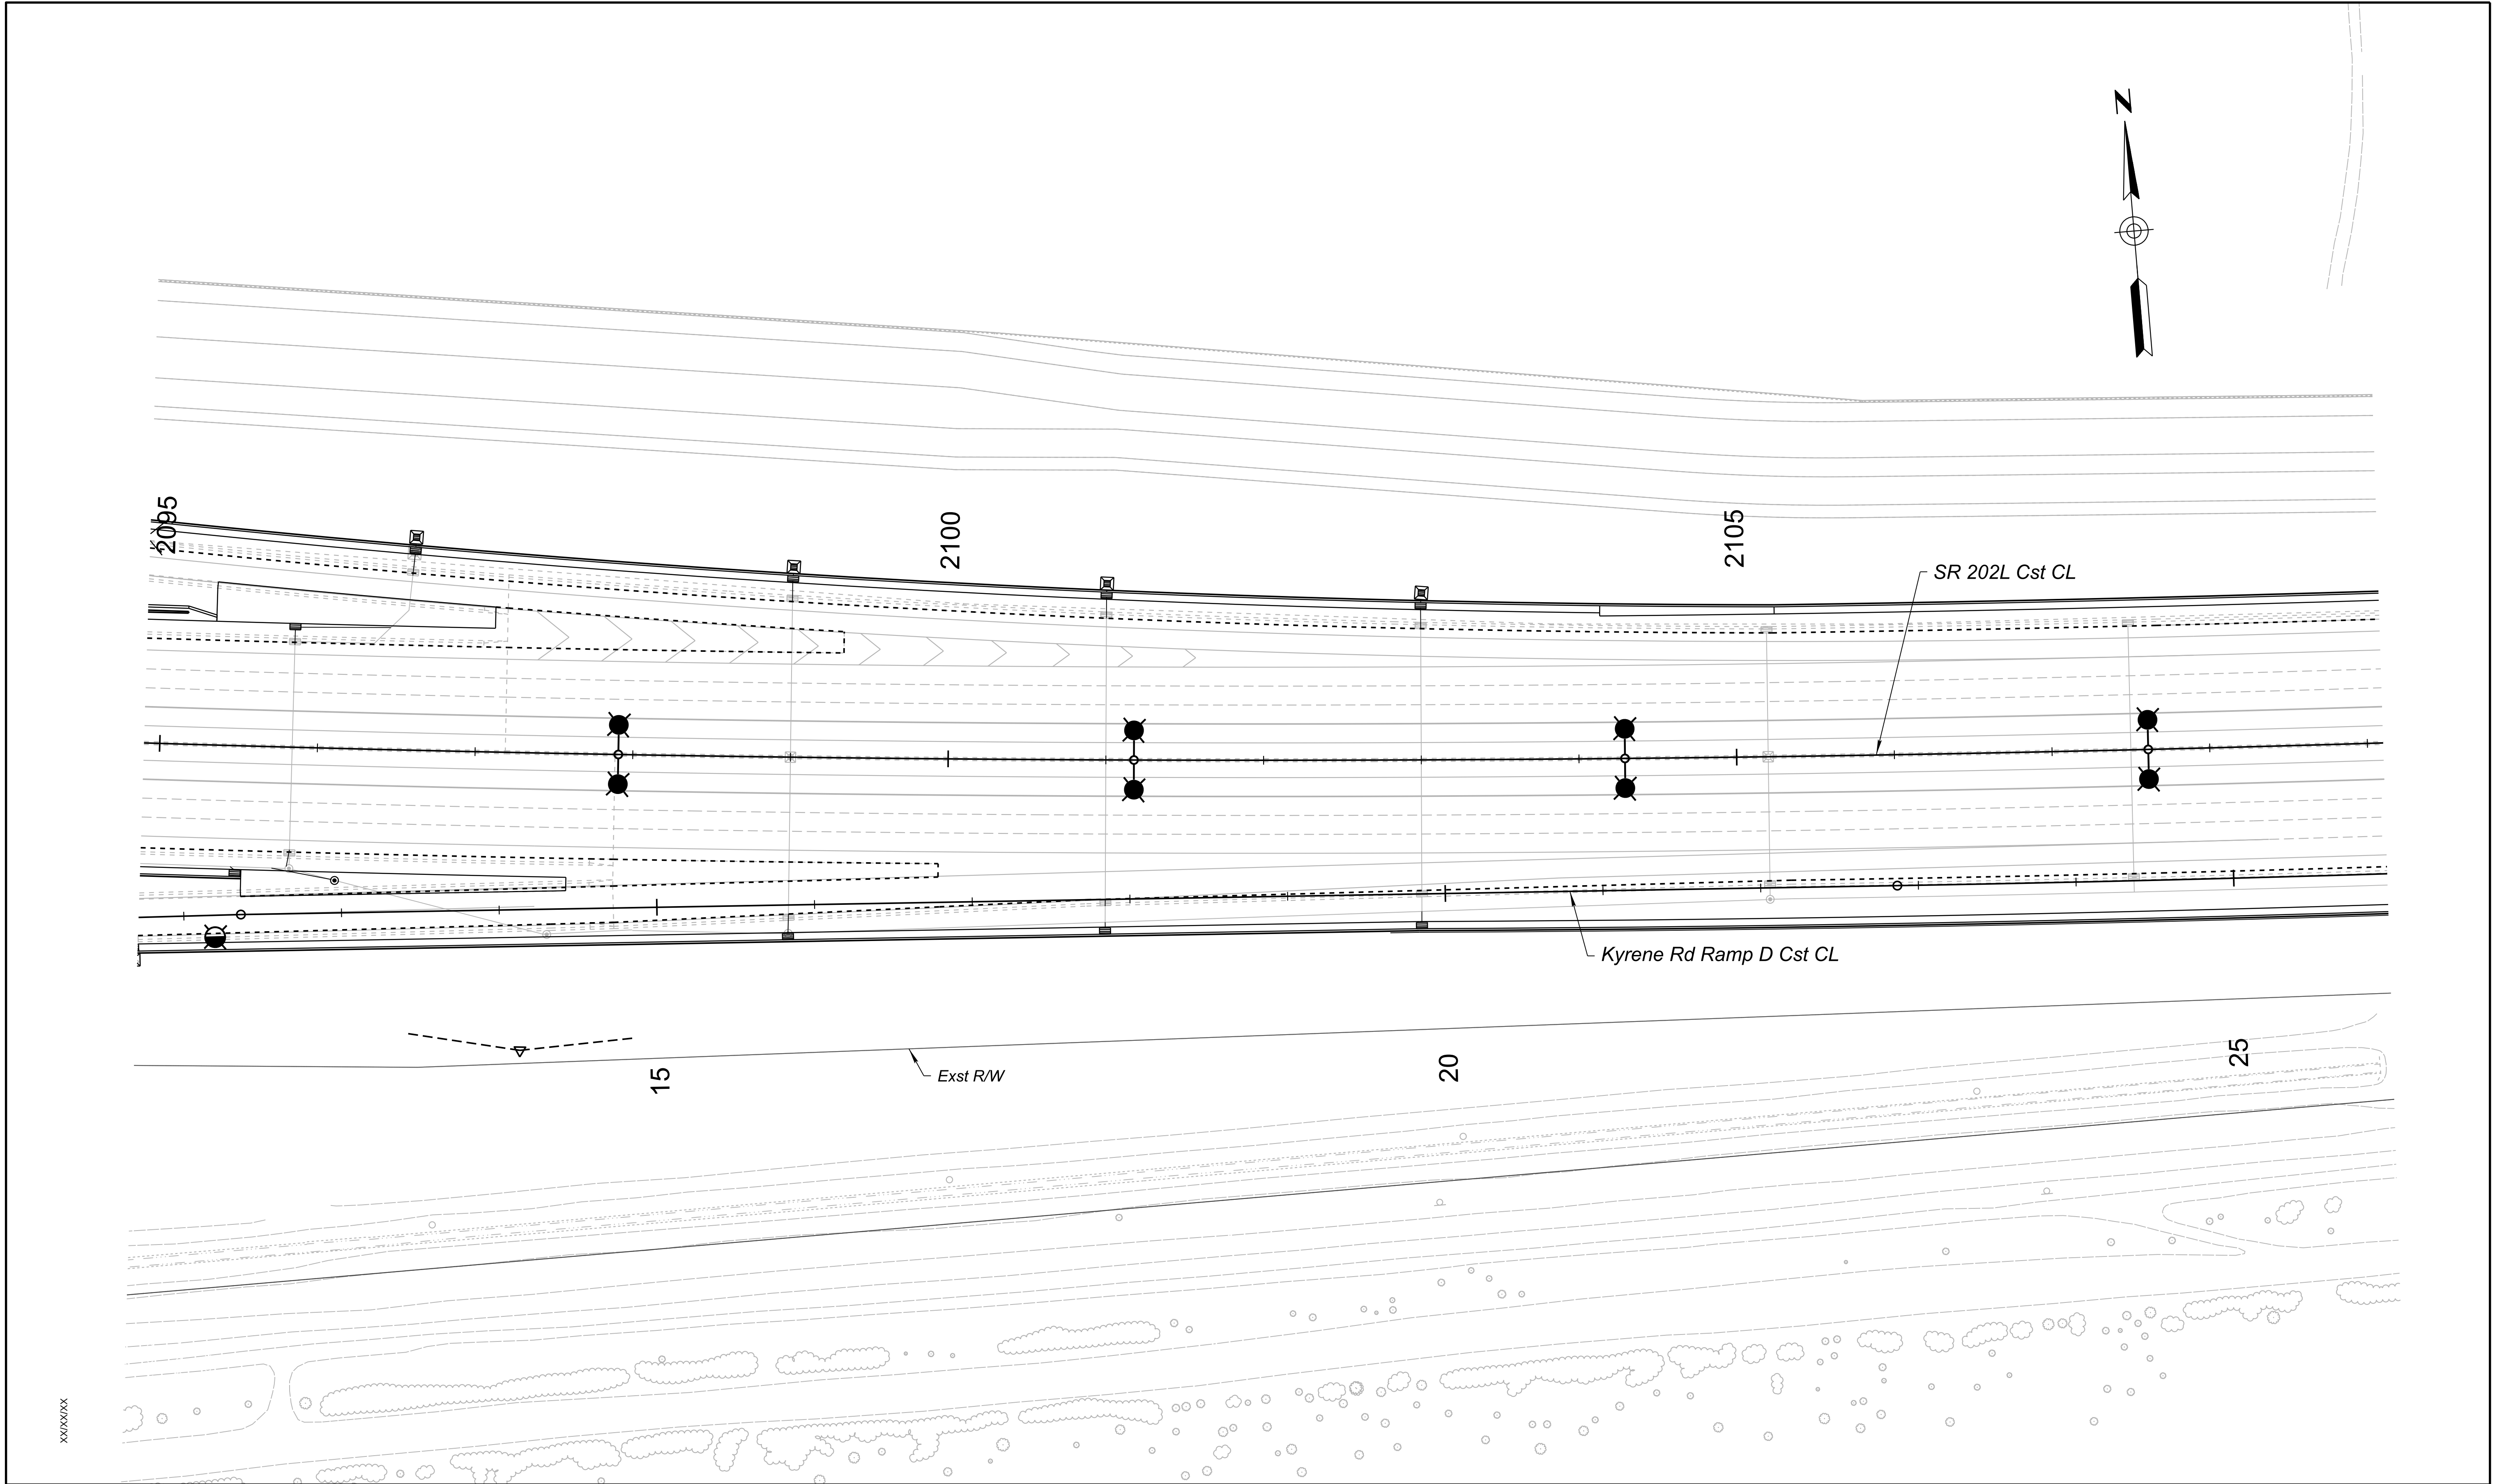


XXXXXXXXXXXX	PRELIMINARY STAGE III Review NOT FOR CONSTRUCTION OR RECORDING	501 N 44th St, Suite 300 Phoenix, AZ 85008-4505 Tel (602) 454-0402 www.typsa.us  TYP SA	DESIGN	NAME	DATE	ARIZONA DEPARTMENT OF TRANSPORTATION PROJECT DELIVERY AND OPERATIONS DIVISION DRAINAGE DESIGN SECTION	ROUTE	F.H.W.A. Arizona Division	STATE	PROJECT NO.	FEDERAL ID NO.	SHEET NO.	TOTAL SHEETS	RECORD DRAWING			
			DRAWN														
			CHECKED														
								MILEPOST									
								STRUCTURE NO.									
						SR 202L DRAINAGE PLAN SHEET STA 2095+00 TO 2109+00	SR 202L SANTAN FREEWAY - I-10 TO SR 101L DWG No. D-02.10										
						TRACS NO. F0847 01D								___ OF ___			