


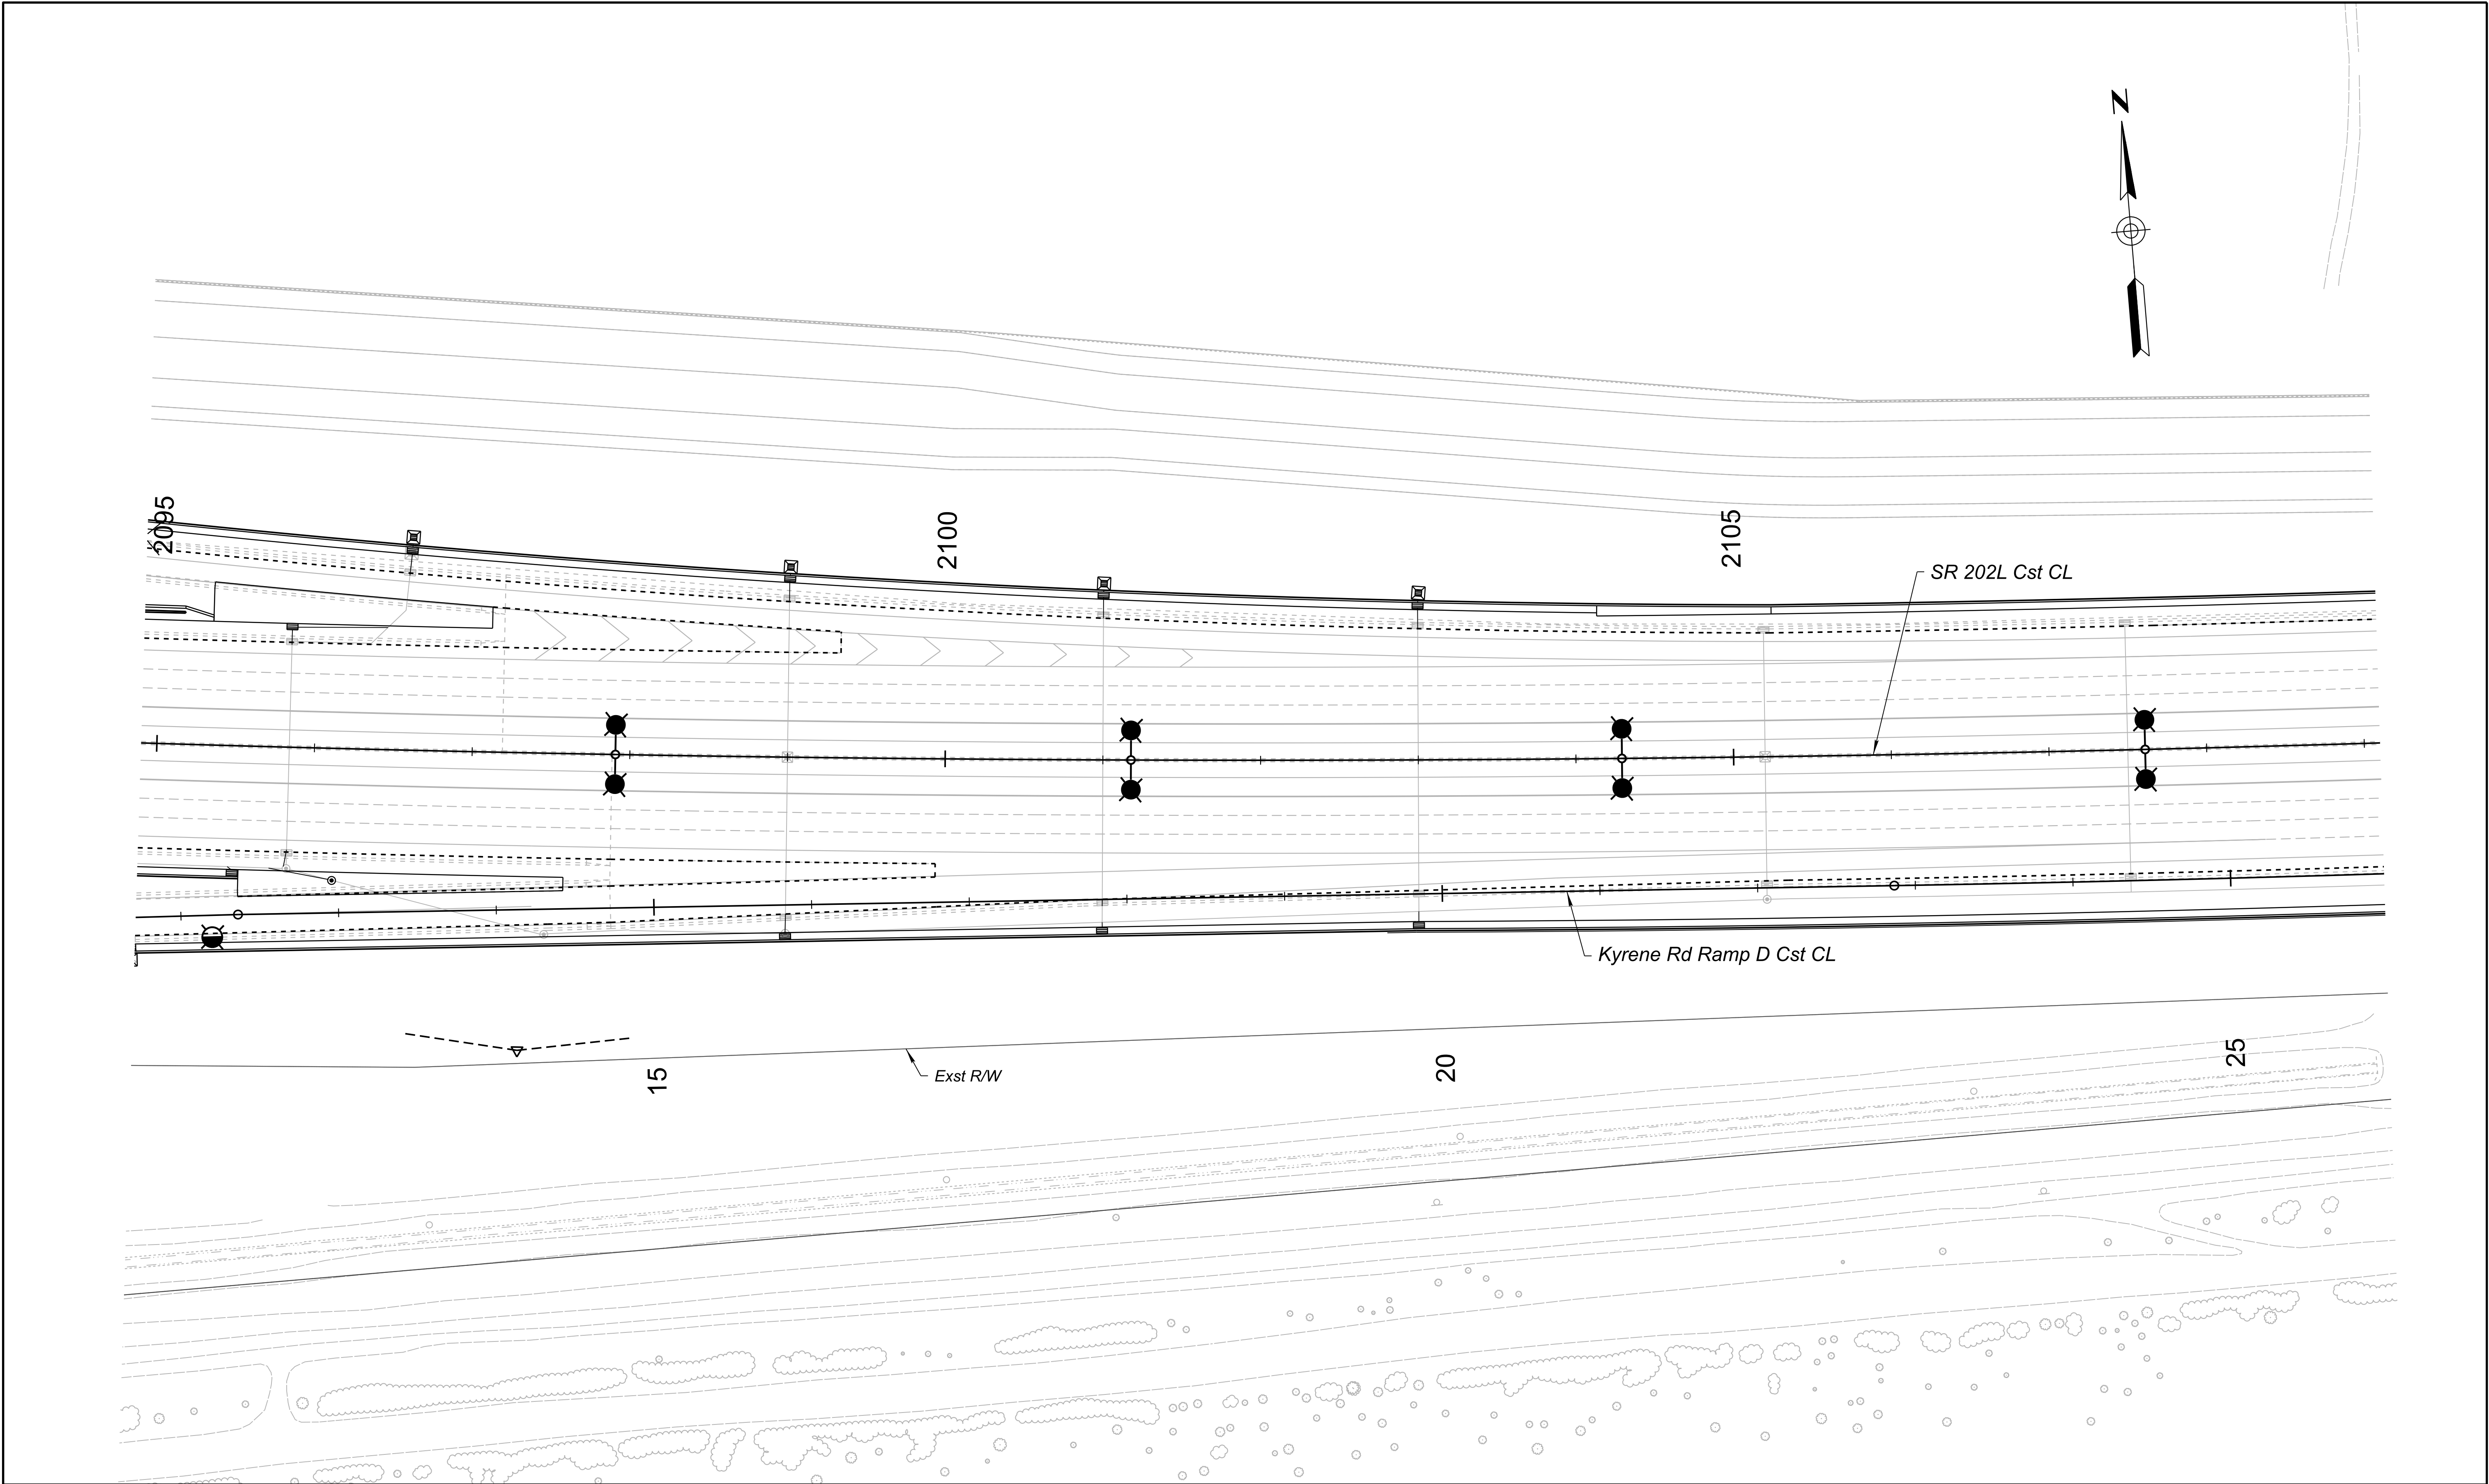

PRELIMINARY STAGE III Review NOT FOR CONSTRUCTION OR RECORDING		NAME	DATE	ARIZONA DEPARTMENT OF TRANSPORTATION PROJECT DELIVERY AND OPERATIONS DIVISION DRAINAGE DESIGN SECTION	ROUTE	F.H.W.A. Arizona Division	STATE ARIZ.	PROJECT NO.	FEDERAL ID NO.	SHEET NO.	TOTAL SHEETS	RECORD DRAWING
	DESIGN				SR 202L							
	DRAWN				MILEPOST			LOCATION SR 202L SANTAN FREEWAY - I-10 TO SR 101L				
	CHECKED			STRUCTURE NO.	TRACS NO. F0847 01D					___ OF ___		
	 501 N 44th St, Suite 300 Phoenix, AZ 85008-4505 Tel (602) 454-0402 www.typsas.us	SR 202L DRAINAGE PLAN SHEET STA 2095+00 TO 2109+00										