


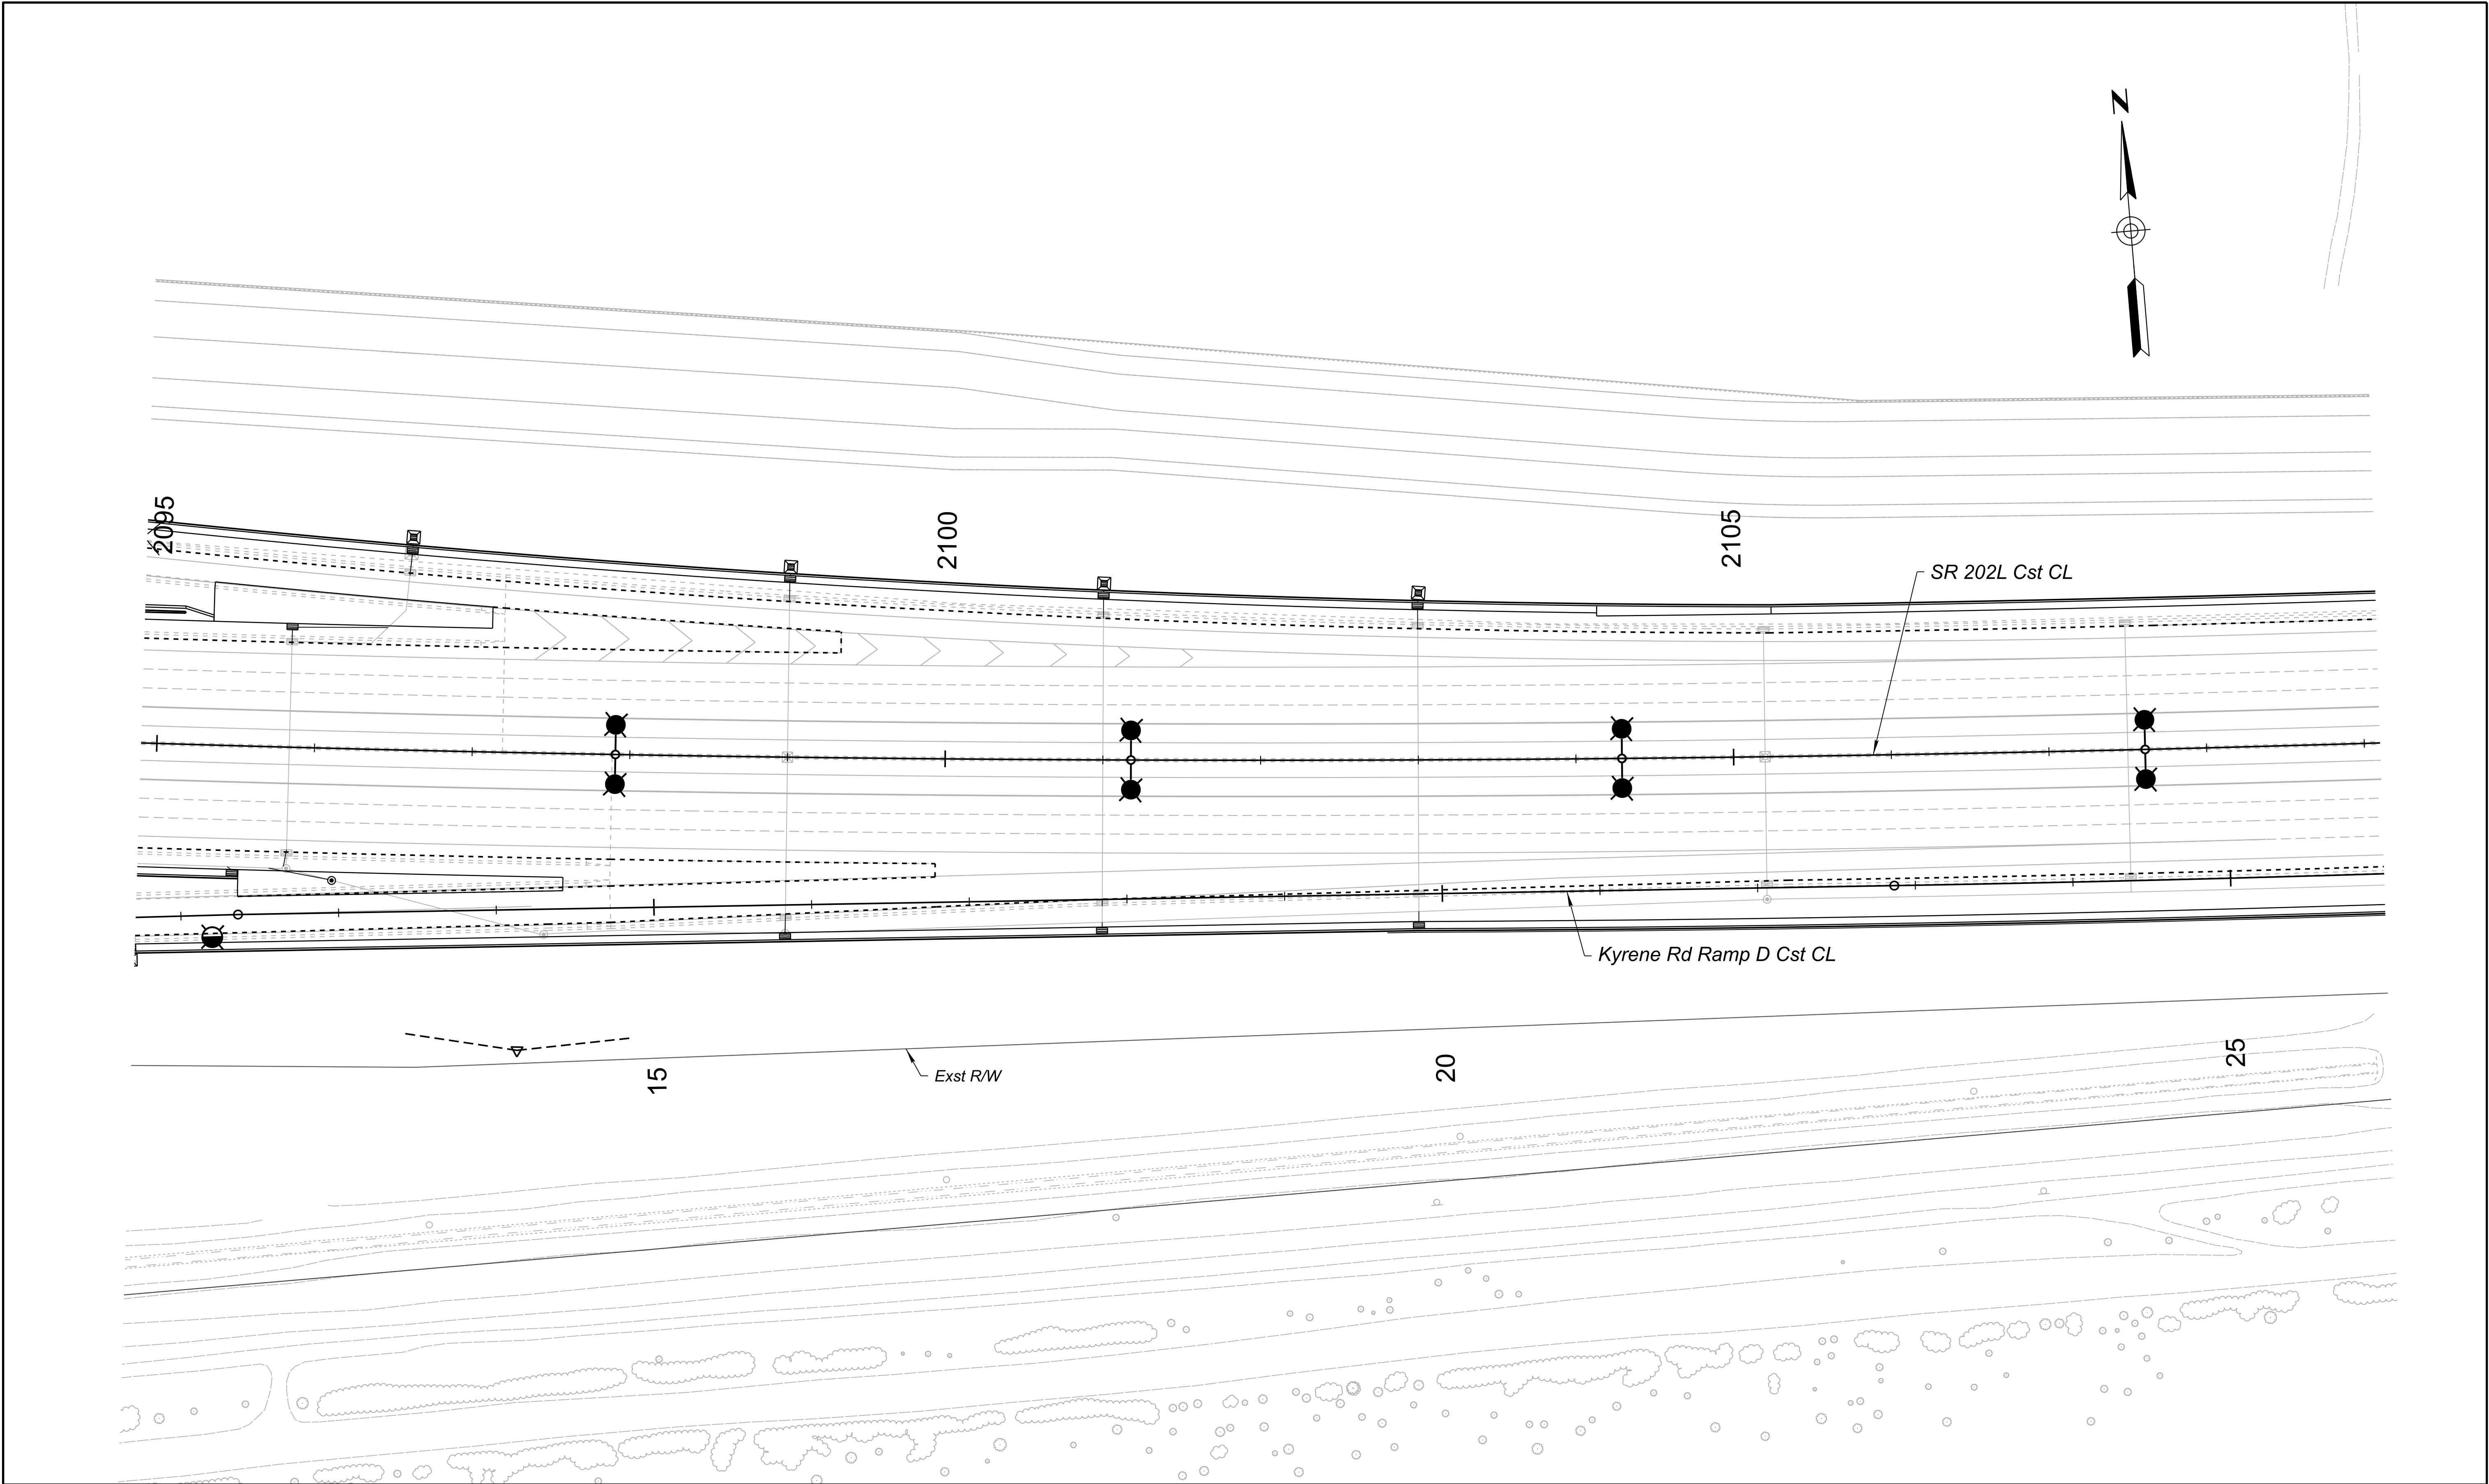

PRELIMINARY STAGE III Review NOT FOR CONSTRUCTION OR RECORDING			NAME	DATE	ARIZONA DEPARTMENT OF TRANSPORTATION PROJECT DELIVERY AND OPERATIONS DIVISION DRAINAGE DESIGN SECTION	ROUTE	F.H.W.A. Arizona Division	STATE ARIZ.	PROJECT NO.	FEDERAL ID NO.	SHEET NO.	TOTAL SHEETS	RECORD DRAWING					
	DESIGN					MILEPOST			LOCATION SR 202L SANTAN FREEWAY - I-10 TO SR 101L	DWG No. D-02.10								
	DRAWN																	
	CHECKED																	
		501 N 44th St, Suite 300 Phoenix, AZ 85008-4505 Tel (602) 454-0402 www.typsas.us			SR 202L DRAINAGE PLAN SHEET STA 2095+00 TO 2109+00						STRUCTURE NO.	SR 202L SANTAN FREEWAY - I-10 TO SR 101L					DWG No. D-02.10	
		TRACS NO. F0847 01D										___ OF ___						