
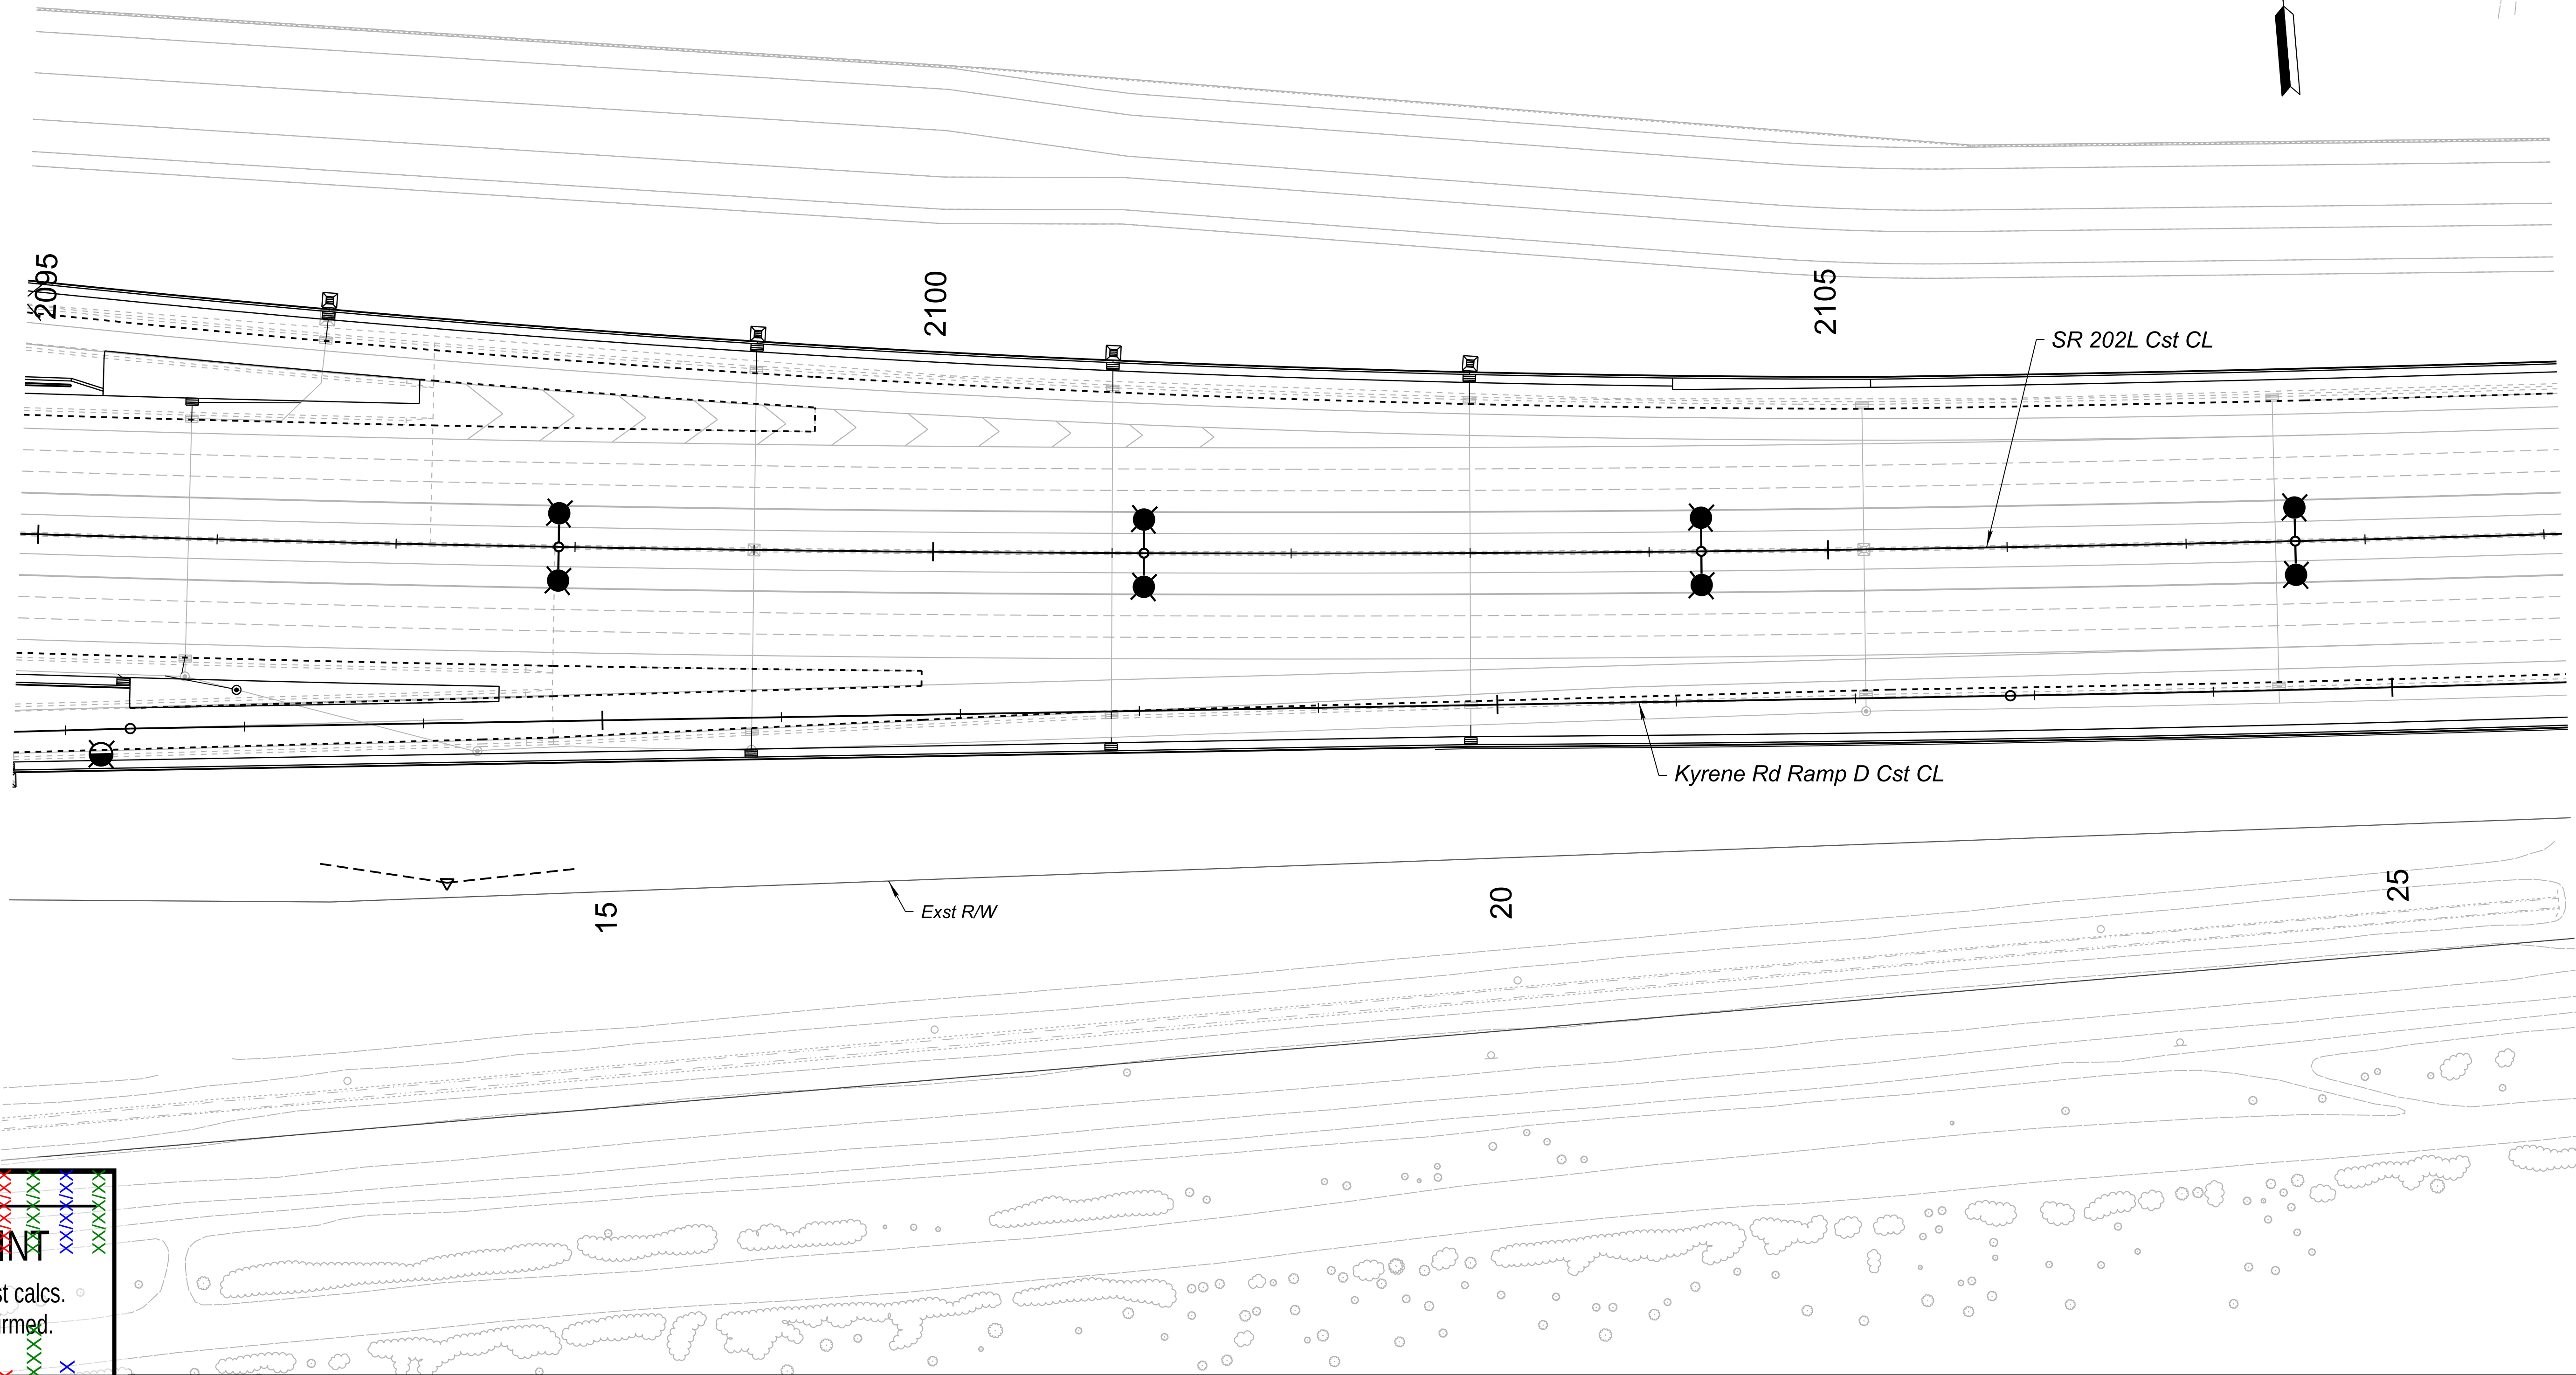


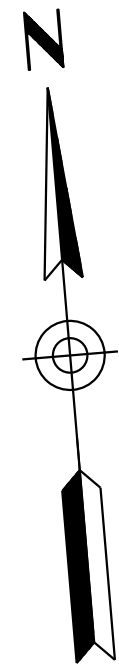

No. _____ Date _____

XXXXXXXX

CHECK PRINT

Dgn. checked against calcs.
and calc. check confirmed.

By _____ Date _____

Checked _____ Date _____

Backchecked _____ Date _____

Corrected _____ Date _____

Verified _____ Date _____

Jake Flint

2/11/2026 3:00:52 PM AZDOT 2024\AZFWY1704-FD02-SR202 - I-10 to SR101\CADD\Sheets\050_D-02.10_d0847dm.dgn

PRELIMINARY STAGE III Review NOT FOR CONSTRUCTION OR RECORDING	NAME		DATE	ARIZONA DEPARTMENT OF TRANSPORTATION PROJECT DELIVERY AND OPERATIONS DIVISION DRAINAGE DESIGN SECTION	ROUTE	F.H.W.A. Arizona Division	STATE ARIZ.	PROJECT NO.	FEDERAL ID NO.	SHEET NO.	TOTAL SHEETS	RECORD DRAWING	
	DESIGN				SR 202L								
	DRAWN				SR 202L DRAINAGE PLAN SHEET STA 2095+00 TO 2109+00	MILEPOST	LOCATION SR 202L SANTAN FREEWAY - I-10 TO SR 101L						DWG No. D-02.10
	CHECKED					STRUCTURE NO.	TRACS NO. F0847 01D		OF				
	501 N 44th St, Suite 300 Phoenix, AZ 85008-4505 Tel (602) 454-0402 www.typpsa.us TYPSA												