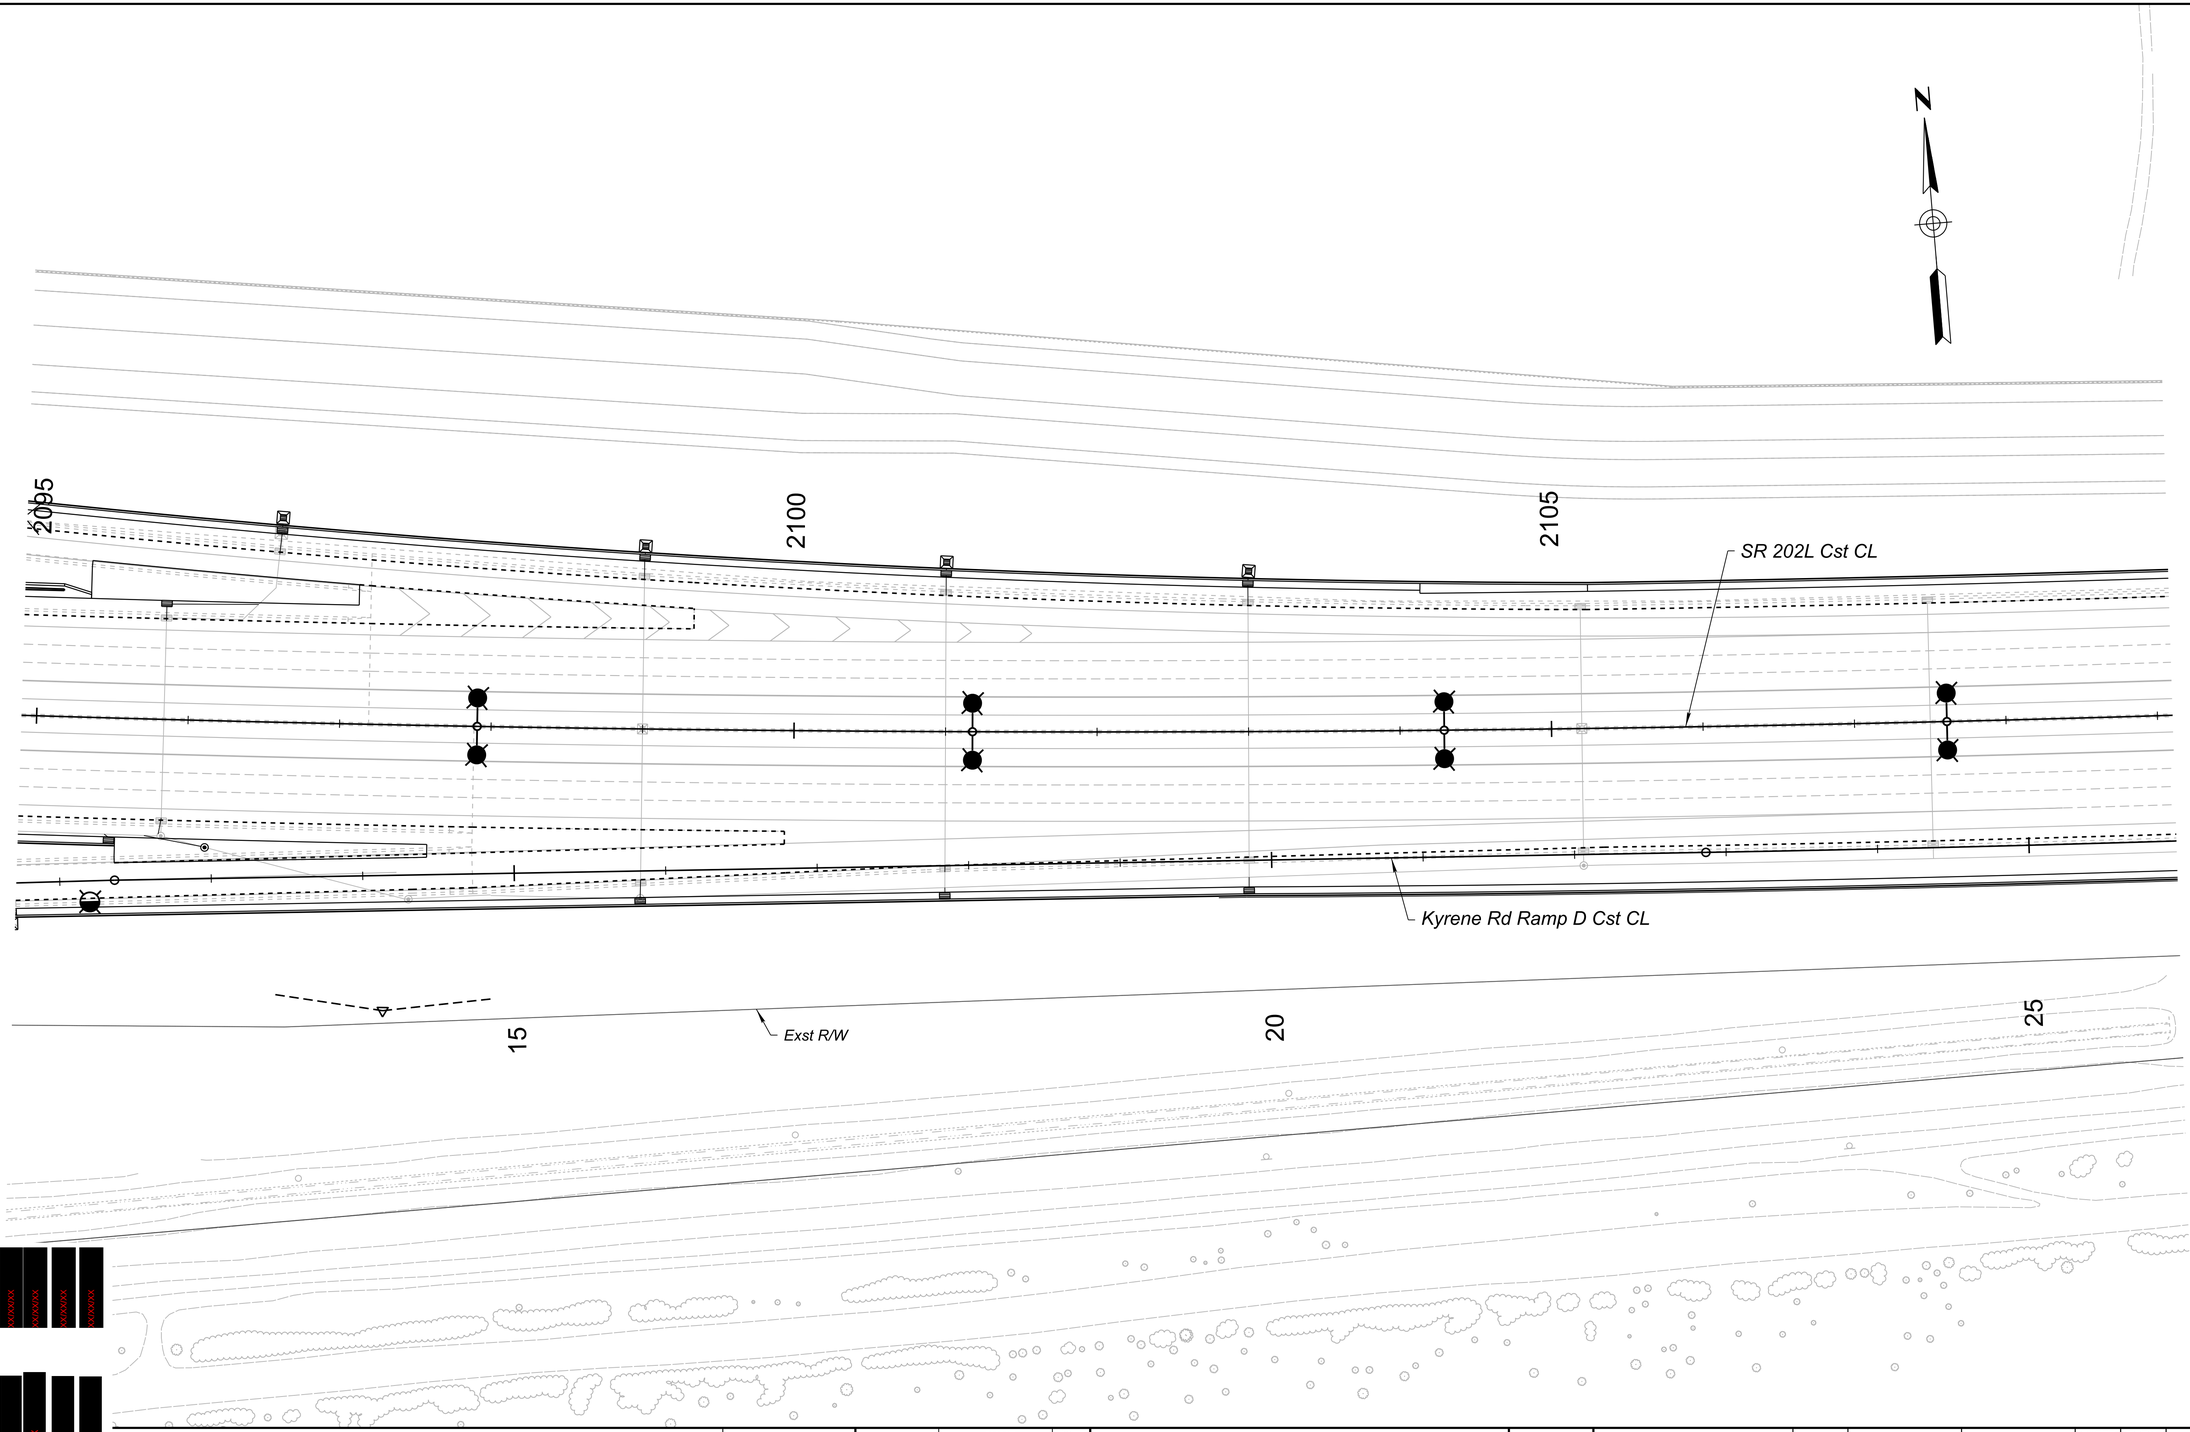

PRELIMINARY

STAGE III

Review

NOT FOR CONSTRUCTION OR RECORDING

	NAME	DATE
DESIGN		
DRAWN		
CHECKED		

TYPSA
501 N 44th St, Suite 300
Phoenix, AZ 85008-4505
Tel (602) 454-0402
www.typsa.us

ARIZONA DEPARTMENT OF TRANSPORTATION
PROJECT DELIVERY AND OPERATIONS DIVISION

DRAINAGE DESIGN SECTION

SR 202L
DRAINAGE PLAN SHEET
STA 2095+00 TO 2109+00

ROUTE SR 202L
MILEPOST
STRUCTURE NO.

F.H.W.A. Arizona Division	STATE	PROJECT NO.	FEDERAL ID NO.	SHEET NO.	TOTAL SHEETS	RECORD DRAWING
	ARIZ.					

LOCATION SR 202L SANTAN FREEWAY - I-10 TO SR 101L

DWG No. D-02.10

TRACS NO. F0847 01D

____ OF ____