
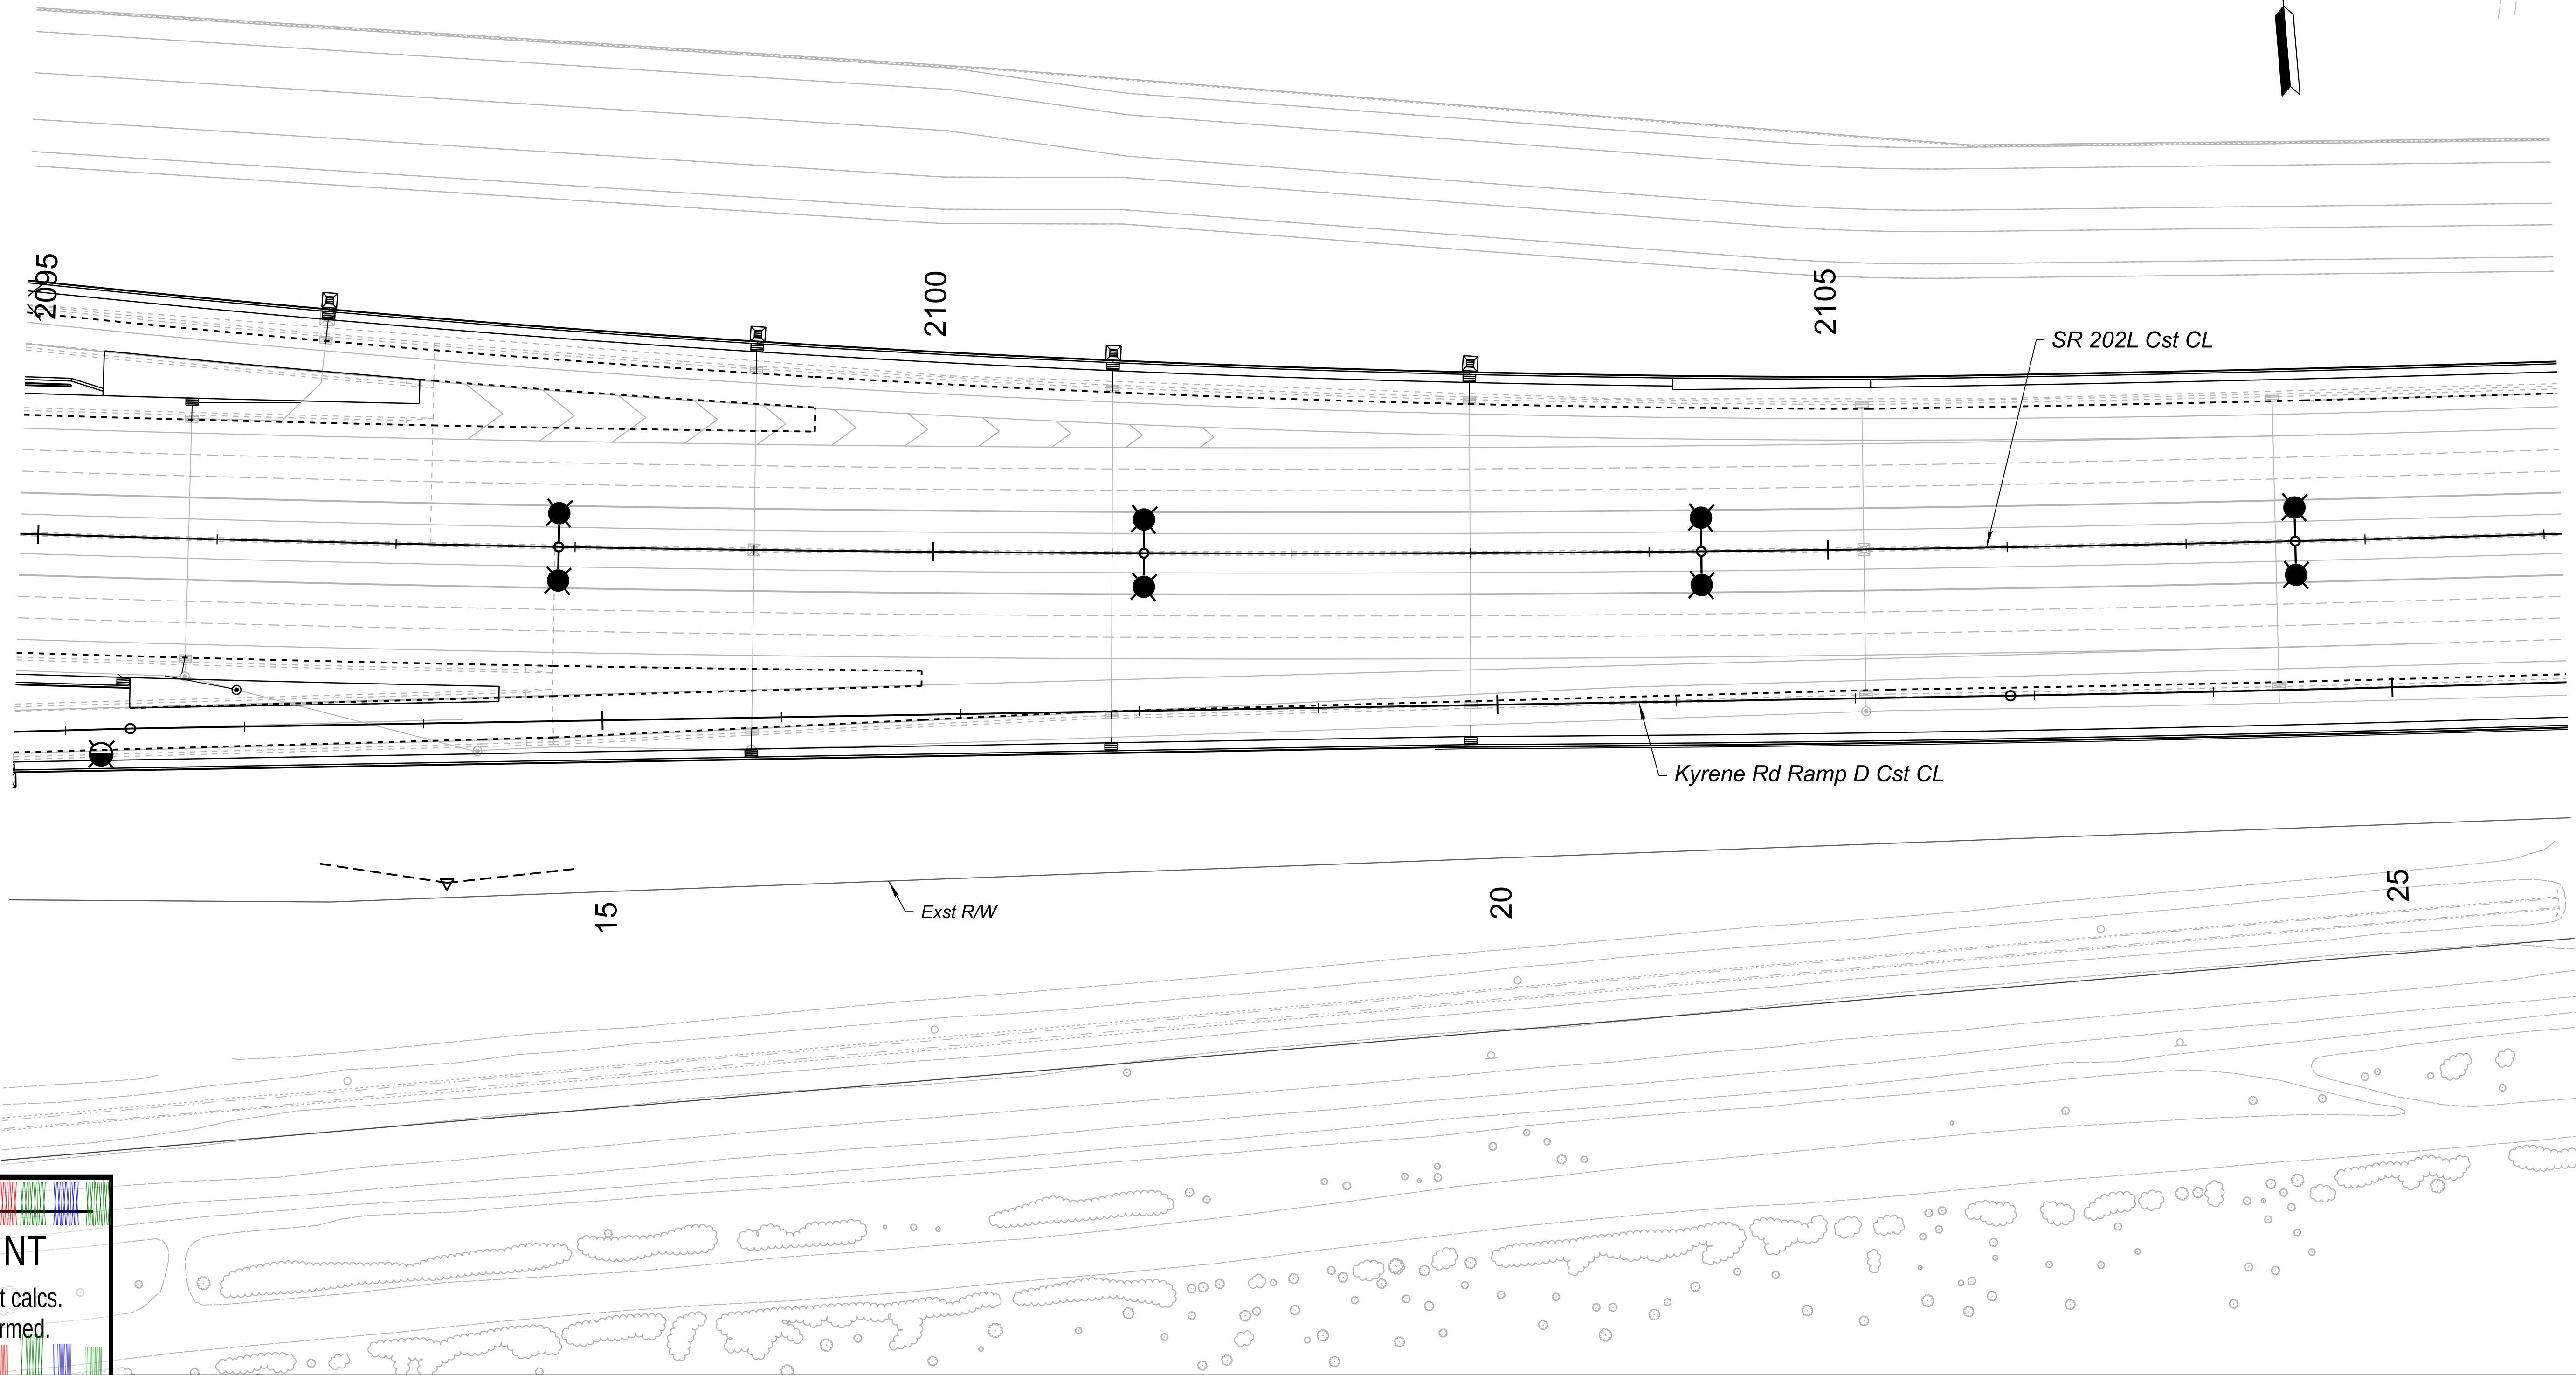


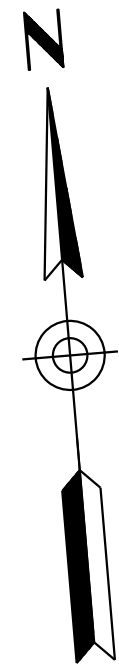

No.	_____	Date	____/____/____
CHECK PRINT			
Dgn. checked against calcs. and calc. check confirmed.			
By	_____	Date	____/____/____

Checked	_____	Date	____/____/____
Backchecked	_____	Date	____/____/____
Corrected	_____	Date	____/____/____
Verified	_____	Date	____/____/____

PRELIMINARY STAGE III Review NOT FOR CONSTRUCTION OR RECORDING	NAME		DATE	ARIZONA DEPARTMENT OF TRANSPORTATION PROJECT DELIVERY AND OPERATIONS DIVISION DRAINAGE DESIGN SECTION	ROUTE	F.H.W.A. Arizona Division	STATE ARIZ.	PROJECT NO.	FEDERAL ID NO.	SHEET NO.	TOTAL SHEETS	RECORD DRAWING
	DESIGN				SR 202L							
	DRAWN											
	CHECKED											
	 501 N 44th St, Suite 300 Phoenix, AZ 85008-4505 Tel (602) 454-0402 www.typsa.us							SR 202L DRAINAGE PLAN SHEET STA 2095+00 TO 2109+00			MILEPOST	LOCATION SR 202L SANTAN FREEWAY - I-10 TO SR 101L DWG No. D-02.10
				STRUCTURE NO.	TRACS NO. F0847 01D		____ OF ____					