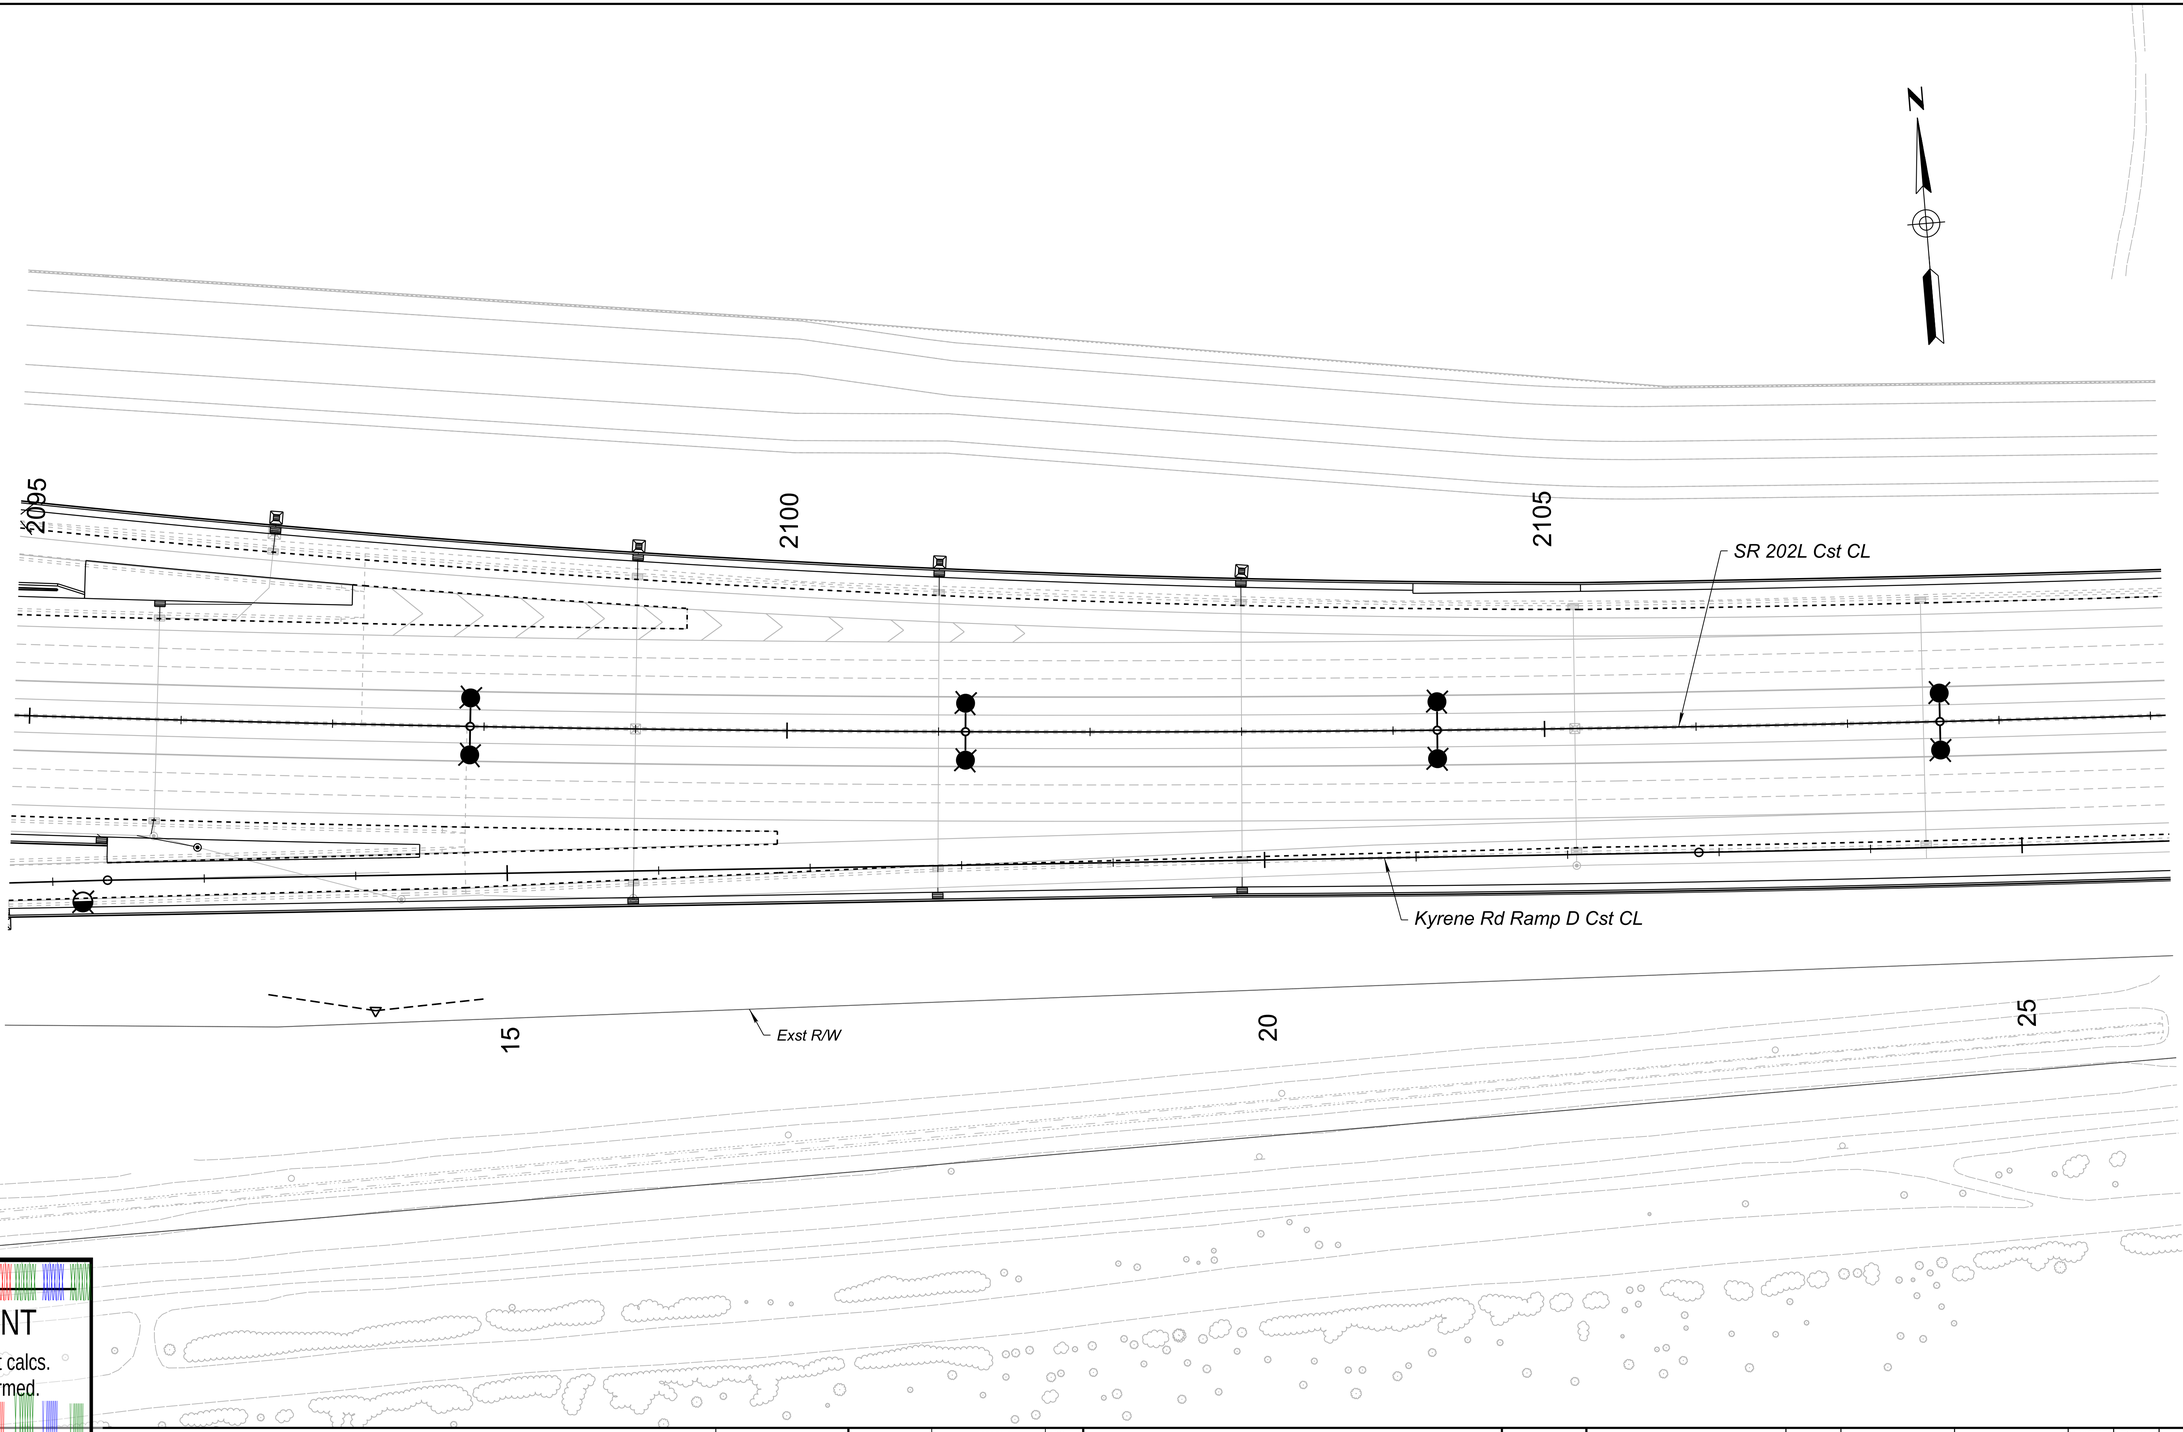


No. _____ Date _____

CHECK PRINT

Dgn. checked against calcs.
and calc. check confirmed.

By _____ Date _____

Checked _____ Date _____

Backchecked _____ Date _____

Corrected _____ Date _____

Verified _____ Date _____

Jake Flint

2/11/2026 3:00:52 PM AZDOT 2024\AZFWY1704-FD02-SR202 - I-10 to SR101\CADD\Sheets\050_D-02.10_d0847drn.dgn

PRELIMINARY

STAGE III

Review

NOT FOR CONSTRUCTION OR RECORDING

	NAME	DATE
DESIGN		
DRAWN		
CHECKED		

TYPSA
501 N 44th St, Suite 300
Phoenix, AZ 85008-4505
Tel (602) 454-0402
www.typsa.us

ARIZONA DEPARTMENT OF TRANSPORTATION
PROJECT DELIVERY AND OPERATIONS DIVISION

DRAINAGE DESIGN SECTION

SR 202L
DRAINAGE PLAN SHEET
STA 2095+00 TO 2109+00

ROUTE: SR 202L
MILEPOST:
STRUCTURE NO.:

F.H.W.A. Arizona Division | STATE: ARIZ. | PROJECT NO. | FEDERAL ID NO. | SHEET NO. | TOTAL SHEETS | RECORD DRAWING

LOCATION: SR 202L SANTAN FREEWAY - I-10 TO SR 101L

DWG No. D-02.10

TRACS NO. F0847 01D

____ OF ____