


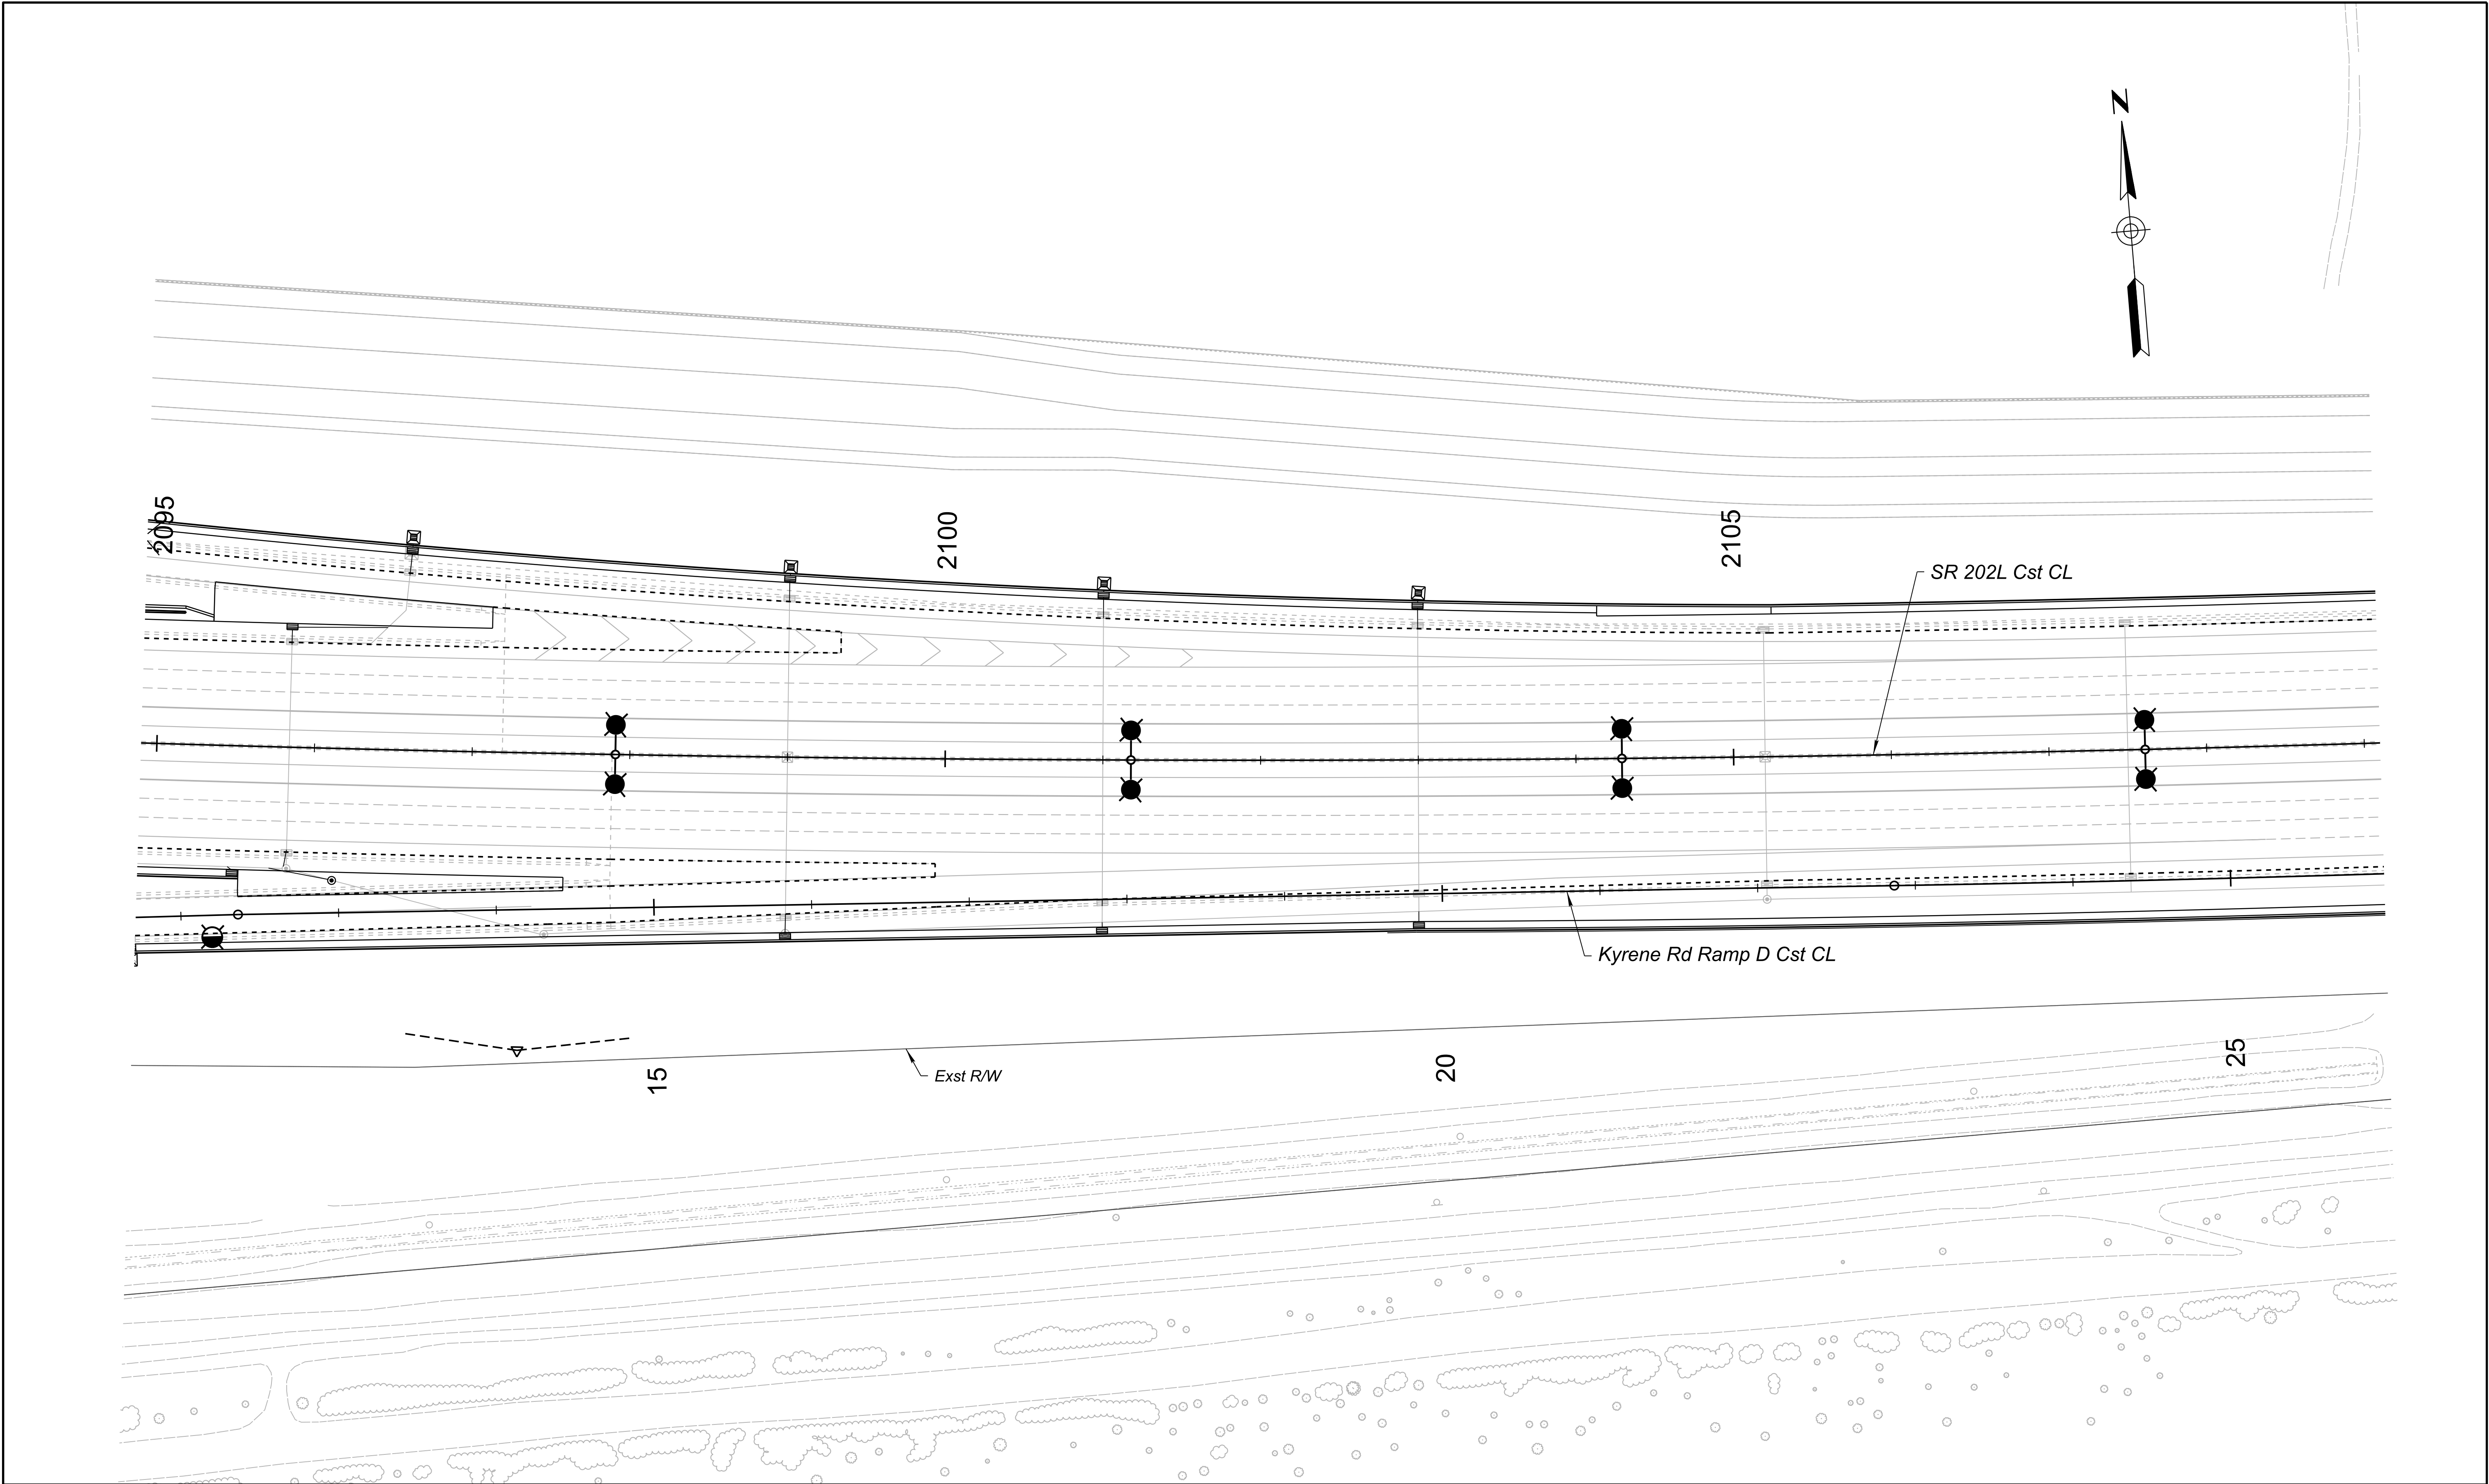

PRELIMINARY STAGE III Review NOT FOR CONSTRUCTION OR RECORDING	DESIGN	NAME	DATE	ARIZONA DEPARTMENT OF TRANSPORTATION PROJECT DELIVERY AND OPERATIONS DIVISION DRAINAGE DESIGN SECTION	ROUTE	F.H.W.A. Arizona Division	STATE	PROJECT NO.	FEDERAL ID NO.	SHEET NO.	TOTAL SHEETS	RECORD DRAWING			
	DRAWN				SR 202L		ARIZ.								
	CHECKED														
	501 N 44th St, Suite 300 Phoenix, AZ 85008-4505 Tel (602) 458-1402 www.typsaz.com TYP SA	SR 202L													
		DRAINAGE PLAN SHEET													
		STA 2095+00 TO 2109+00													
MILEPOST															
STRUCTURE NO.										LOCATION SR 202L SANTAN FREEWAY - I-10 TO SR 101L			DWG No. D-02.10		
TRACS NO. F0847 01D													___ OF ___		