


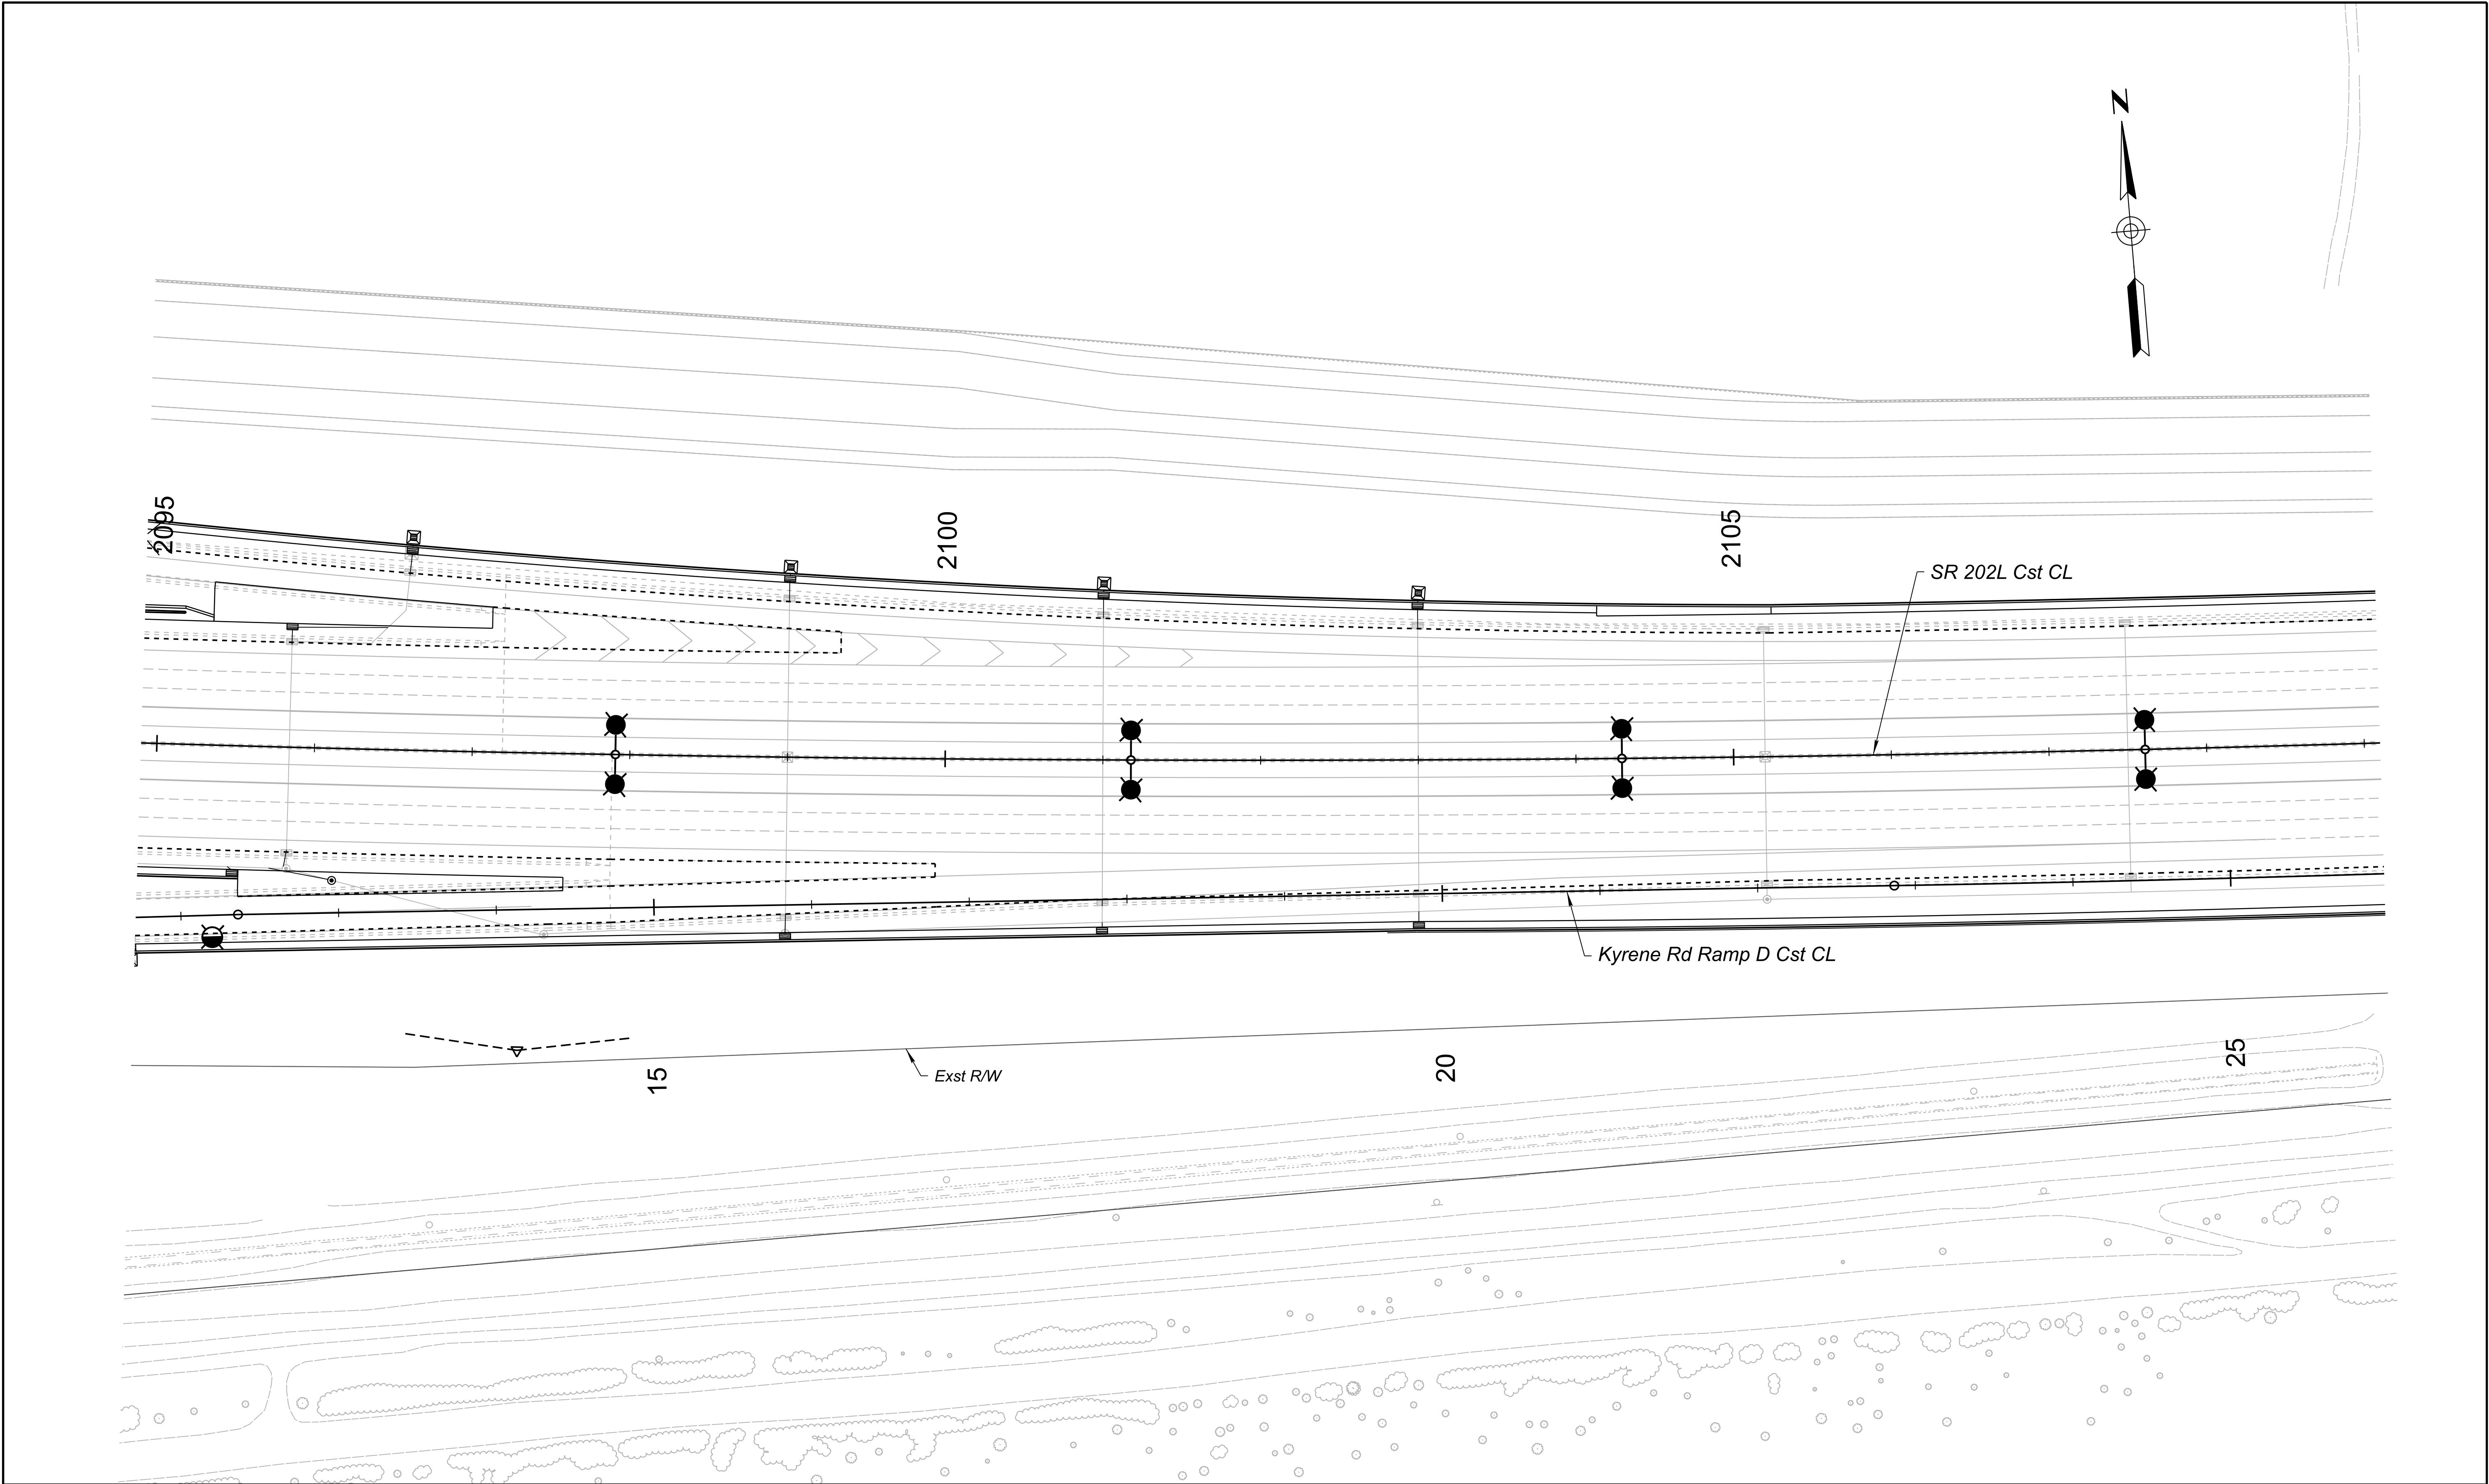

PRELIMINARY STAGE III Review NOT FOR CONSTRUCTION OR RECORDING	DESIGN	NAME	DATE	ARIZONA DEPARTMENT OF TRANSPORTATION PROJECT DELIVERY AND OPERATIONS DIVISION DRAINAGE DESIGN SECTION	ROUTE	F.H.W.A. Arizona Division	STATE	PROJECT NO.	FEDERAL ID NO.	SHEET NO.	TOTAL SHEETS	RECORD DRAWING	
	DRAWN				SR 202L								
	CHECKED					MILEPOST							
	TYPSA 501 N 44th St, Suite 300 Phoenix, AZ 85008-4505 Tel (602) 454-0402 www.typpsa.us	HELLO VIEW SR 202L DRAINAGE PLAN SHEET STA 2095+00 TO 2109+00				LOCATION SR 202L SANTAN FREEWAY - I-10 TO SR 101L						DWG No. D-02.10	
						TRACS NO. F0847 01D						___ OF ___	