


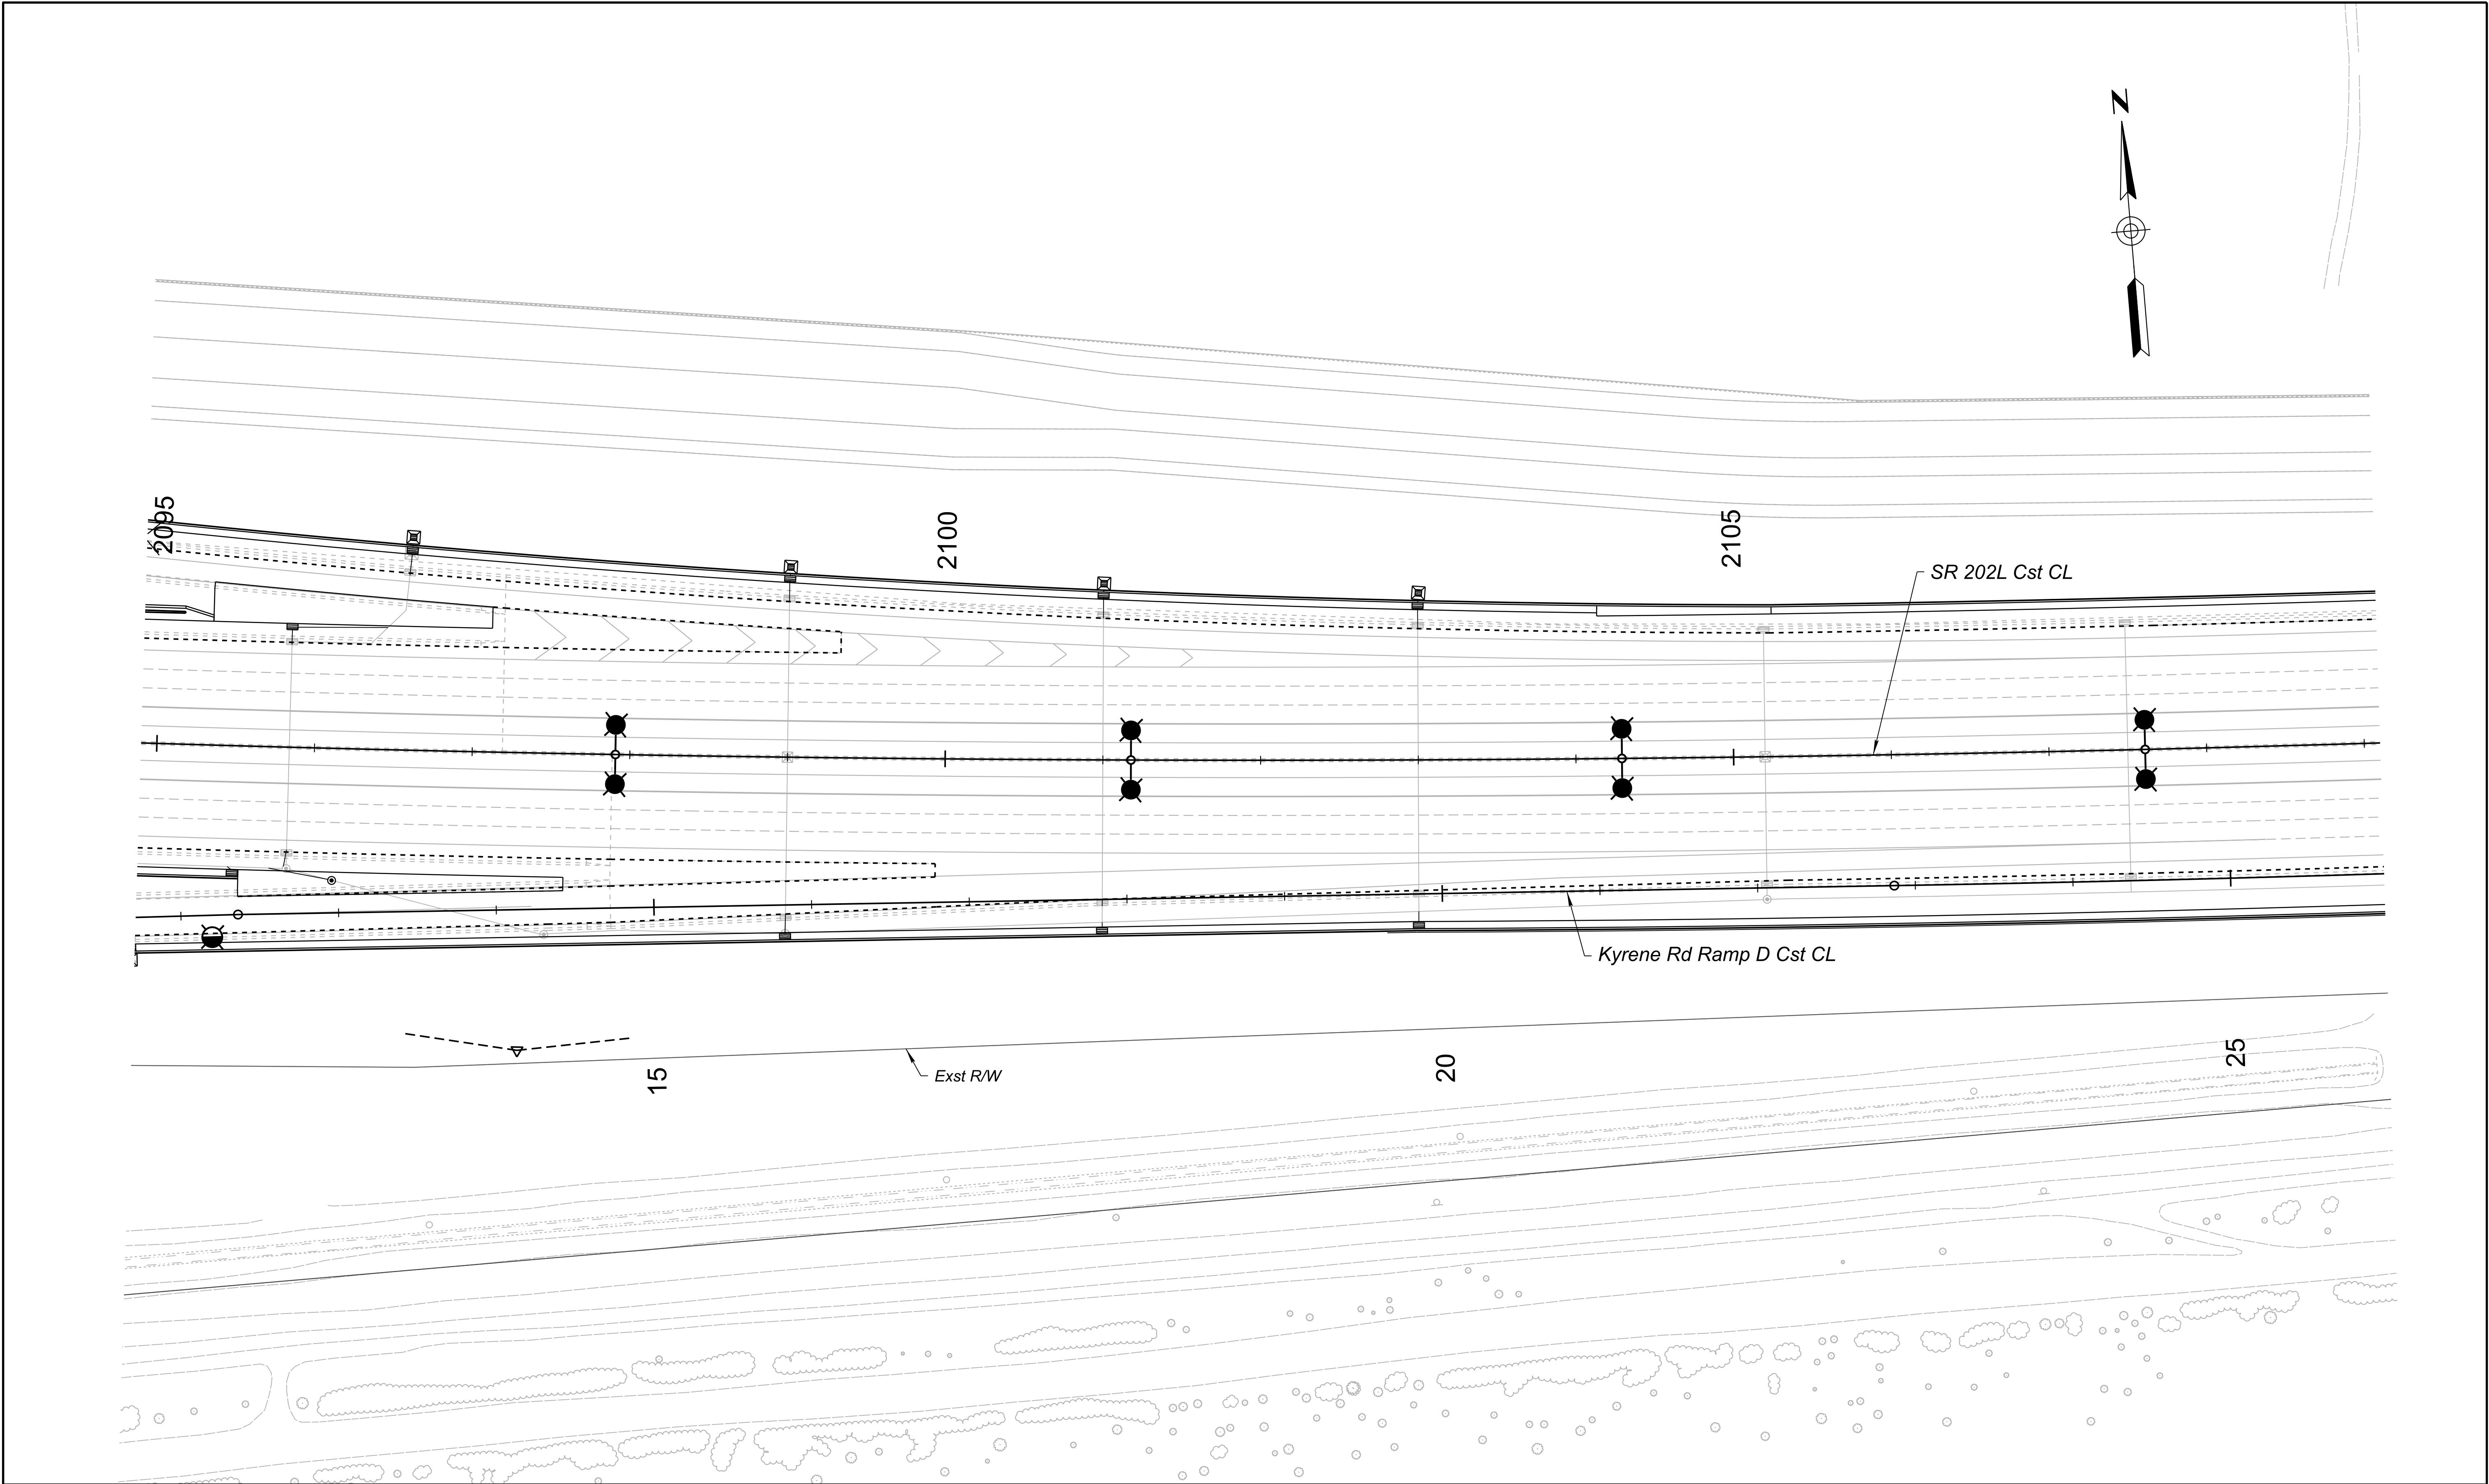

PRELIMINARY STAGE III Review NOT FOR CONSTRUCTION OR RECORDING	DESIGN	NAME	DATE	ARIZONA DEPARTMENT OF TRANSPORTATION PROJECT DELIVERY AND OPERATIONS DIVISION DRAINAGE DESIGN SECTION	ROUTE	F.H.W.A. Arizona Division	STATE ARIZ.	PROJECT NO.	FEDERAL ID NO.	SHEET NO.	TOTAL SHEETS	RECORD DRAWING
	DRAWN				MILEPOST							
	CHECKED				501 N 44th St, Suite 300 Phoenix, AZ 85008-4505 Tel (602) 454-0402 www.typpsa.us www.typpsa.us	SR 202L DRAINAGE PLAN SHEET STA 2095+00 TO 2109+00	LOCATION SR 202L SANTAN FREEWAY - I-10 TO SR 101L				DWG No. D-02.10	
			TRACS NO. F0847 01D				___ OF ___					
						STRUCTURE NO.						