


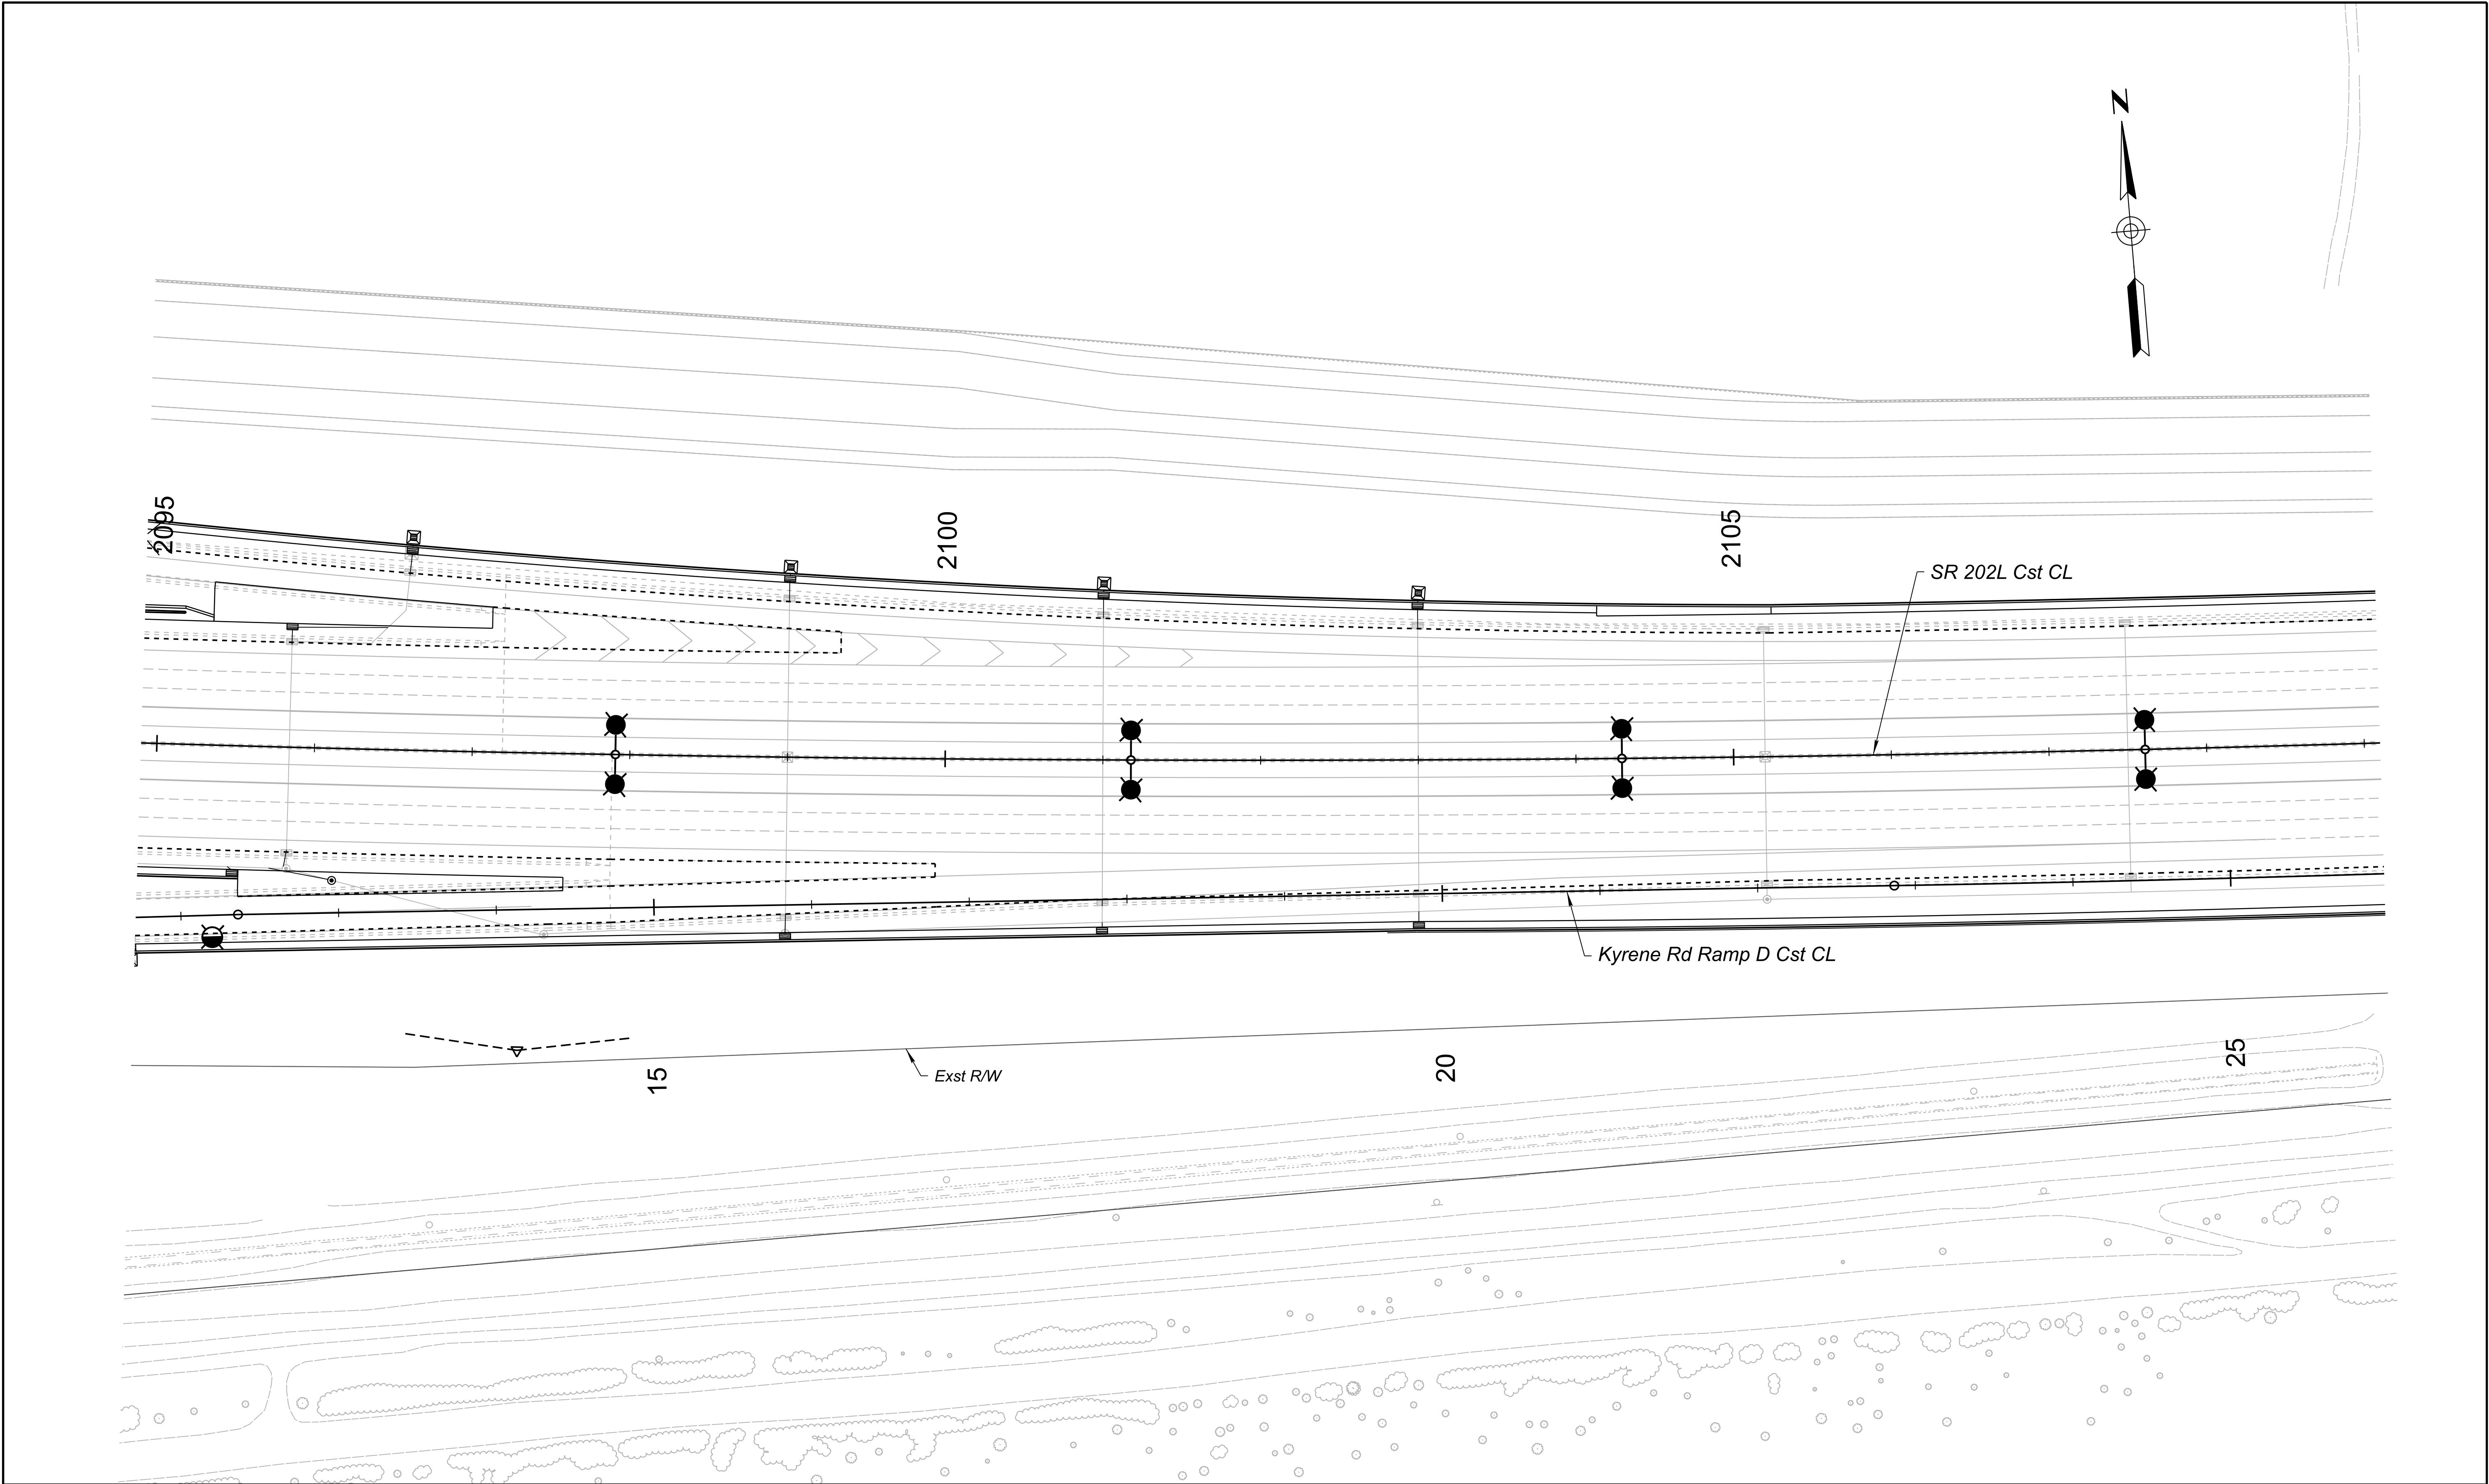

PRELIMINARY STAGE III Review NOT FOR CONSTRUCTION OR RECORDING		NAME	DATE	ARIZONA DEPARTMENT OF TRANSPORTATION PROJECT DELIVERY AND OPERATIONS DIVISION DRAINAGE DESIGN SECTION	ROUTE	F.H.W.A. Arizona Division	STATE ARIZ.	PROJECT NO.	FEDERAL ID NO.	SHEET NO.	TOTAL SHEETS	RECORD DRAWING
	DESIGN											
	DRAWN											
	CHECKED											
		501 N 44th St, Suite 300 Phoenix, AZ 85008-4505 Tel (602) 454-0402 www.typsas.us			SR 202L DRAINAGE PLAN SHEET STA 2095+00 TO 2109+00	MILEPOST	LOCATION SR 202L SANTAN FREEWAY - I-10 TO SR 101L					
					STRUCTURE NO.	TRACS NO. F0847 01D					___ OF ___	