


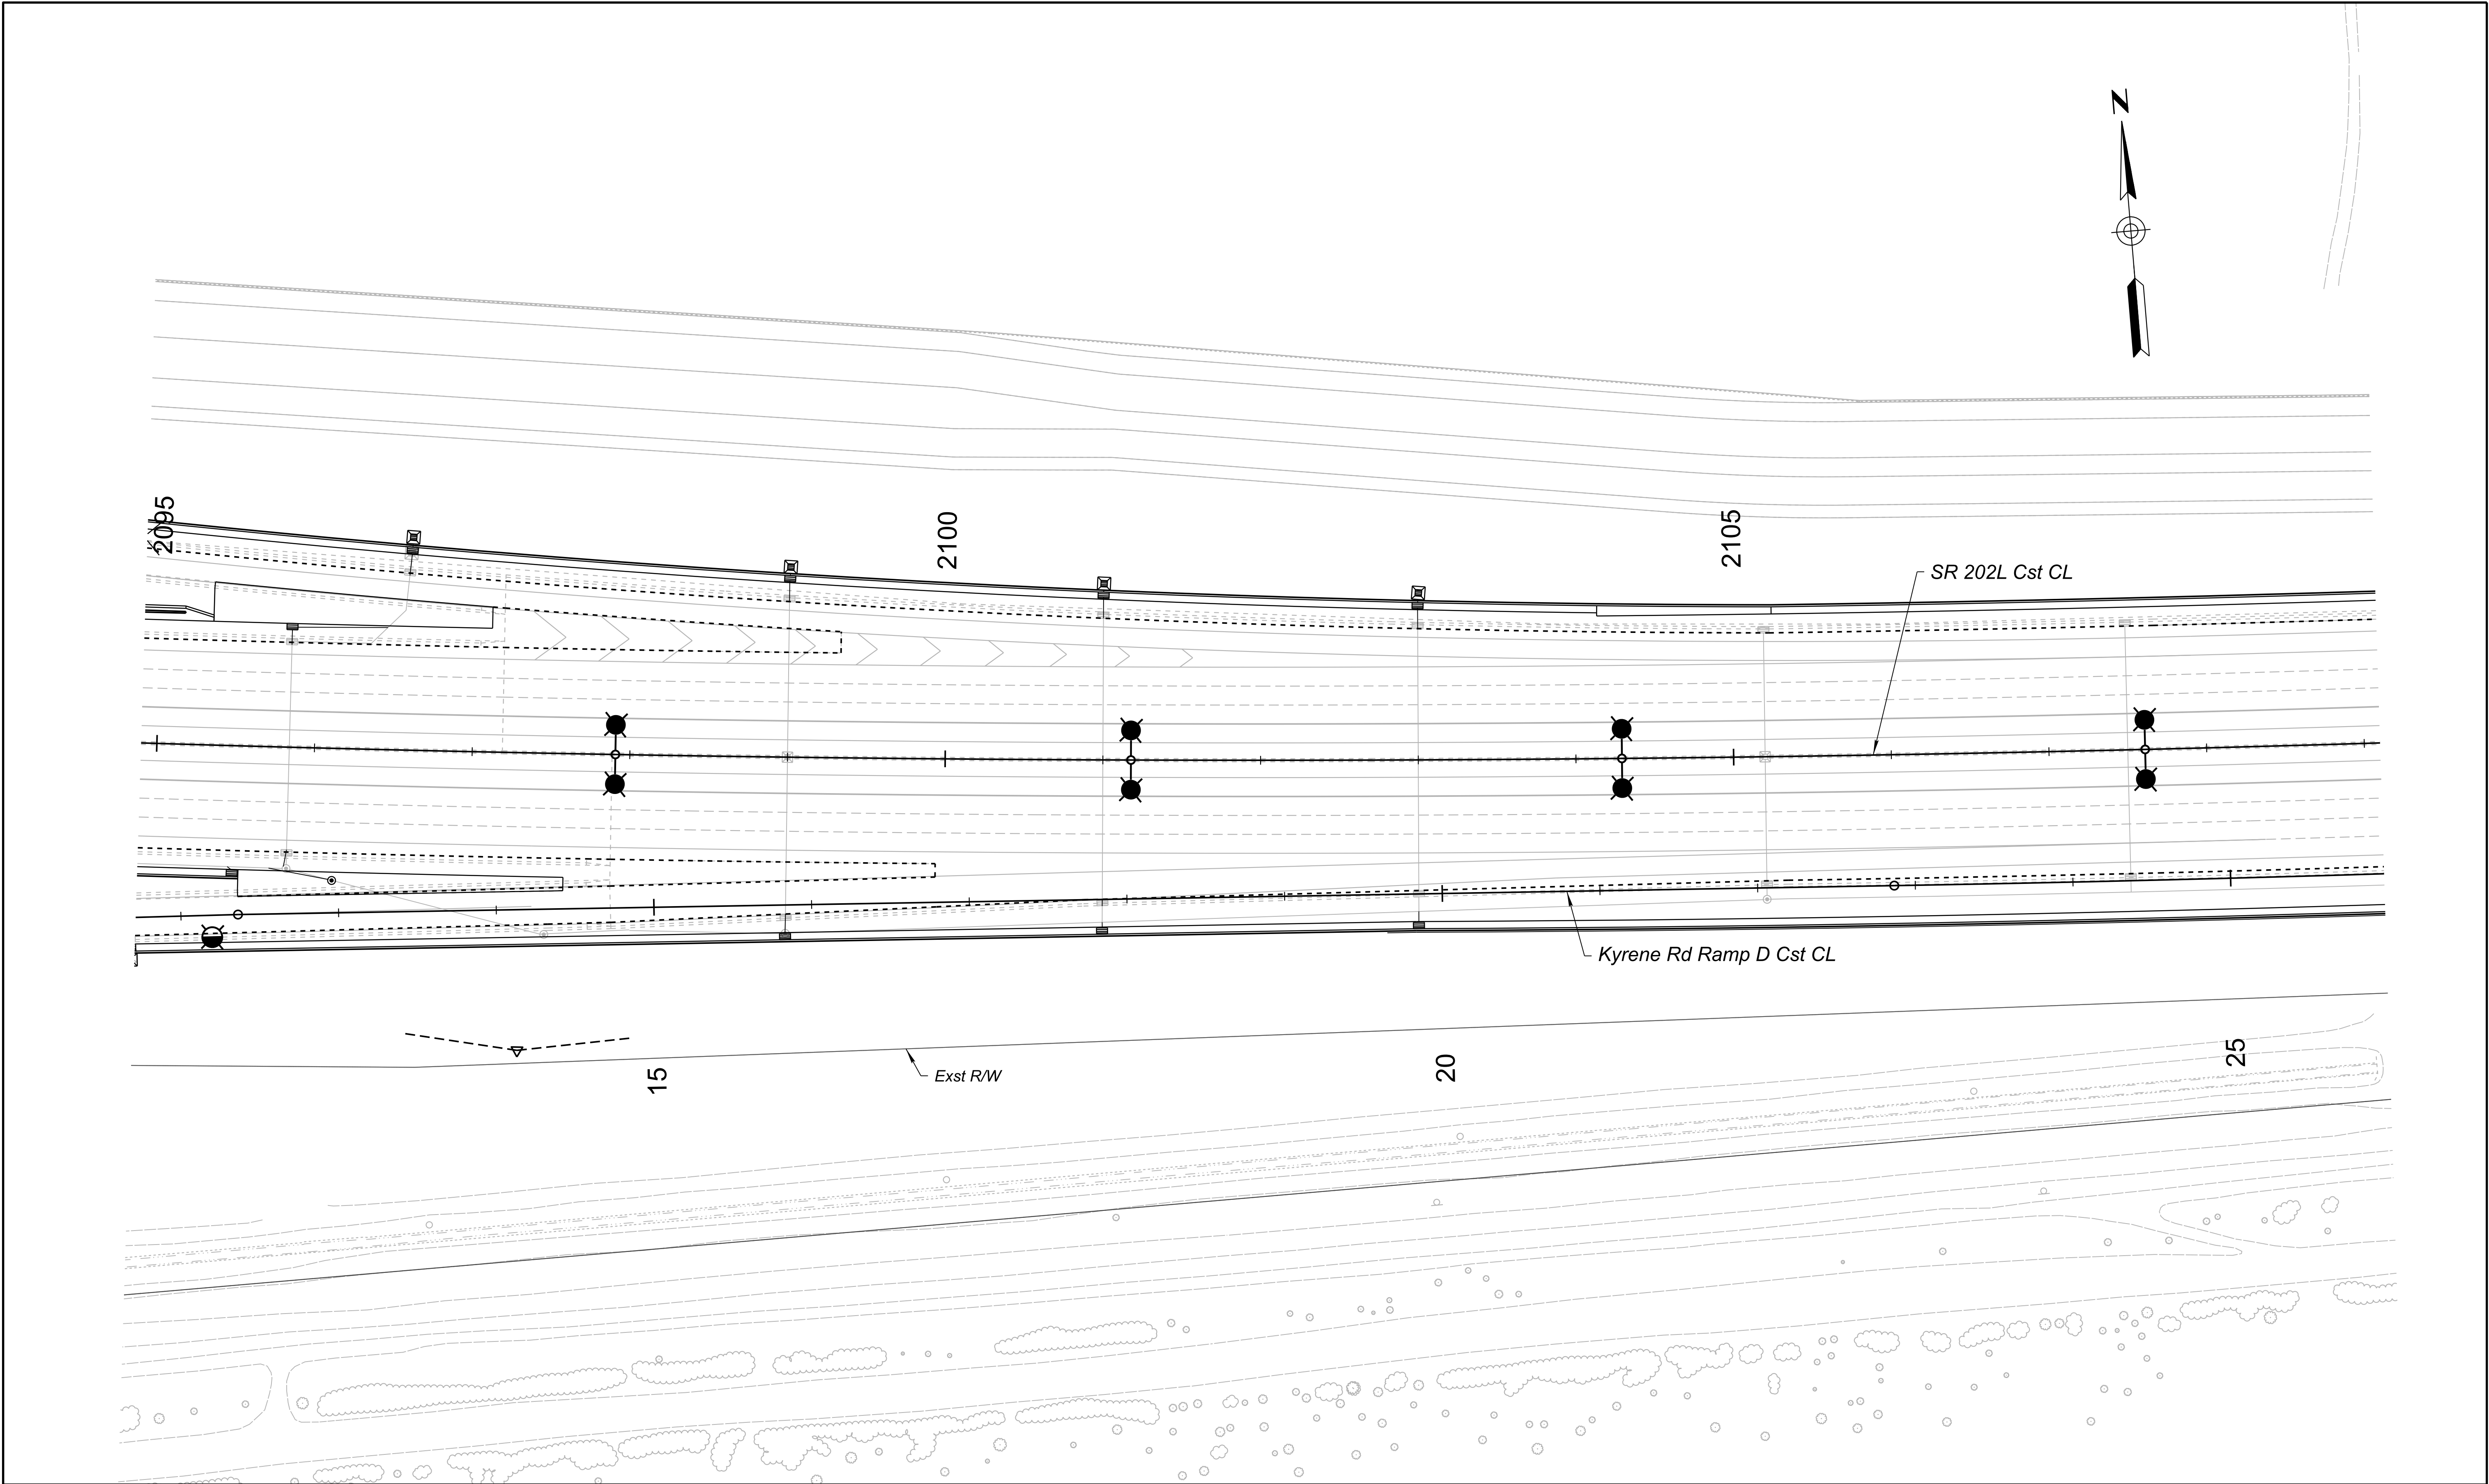

PRELIMINARY STAGE III Review NOT FOR CONSTRUCTION OR RECORDING			NAME		DATE	ARIZONA DEPARTMENT OF TRANSPORTATION PROJECT DELIVERY AND OPERATIONS DIVISION DRAINAGE DESIGN SECTION	ROUTE	F.H.W.A. Arizona Division	STATE ARIZ.	PROJECT NO.	FEDERAL ID NO.	SHEET NO.	TOTAL SHEETS	RECORD DRAWING		
	DESIGN						SR 202L									
	DRAWN							MILEPOST	LOCATION SR 202L SANTAN FREEWAY - I-10 TO SR 101L							DWG No.
	CHECKED						STRUCTURE NO.	TRACS NO. F0847 01D							___ OF ___	
				501 N 44th St, Suite 300 Phoenix, AZ 85008-4505 Tel (602) 454-0402 www.typpsa.us		SR 202L DRAINAGE PLAN SHEET STA 2095+00 TO 2109+00										