


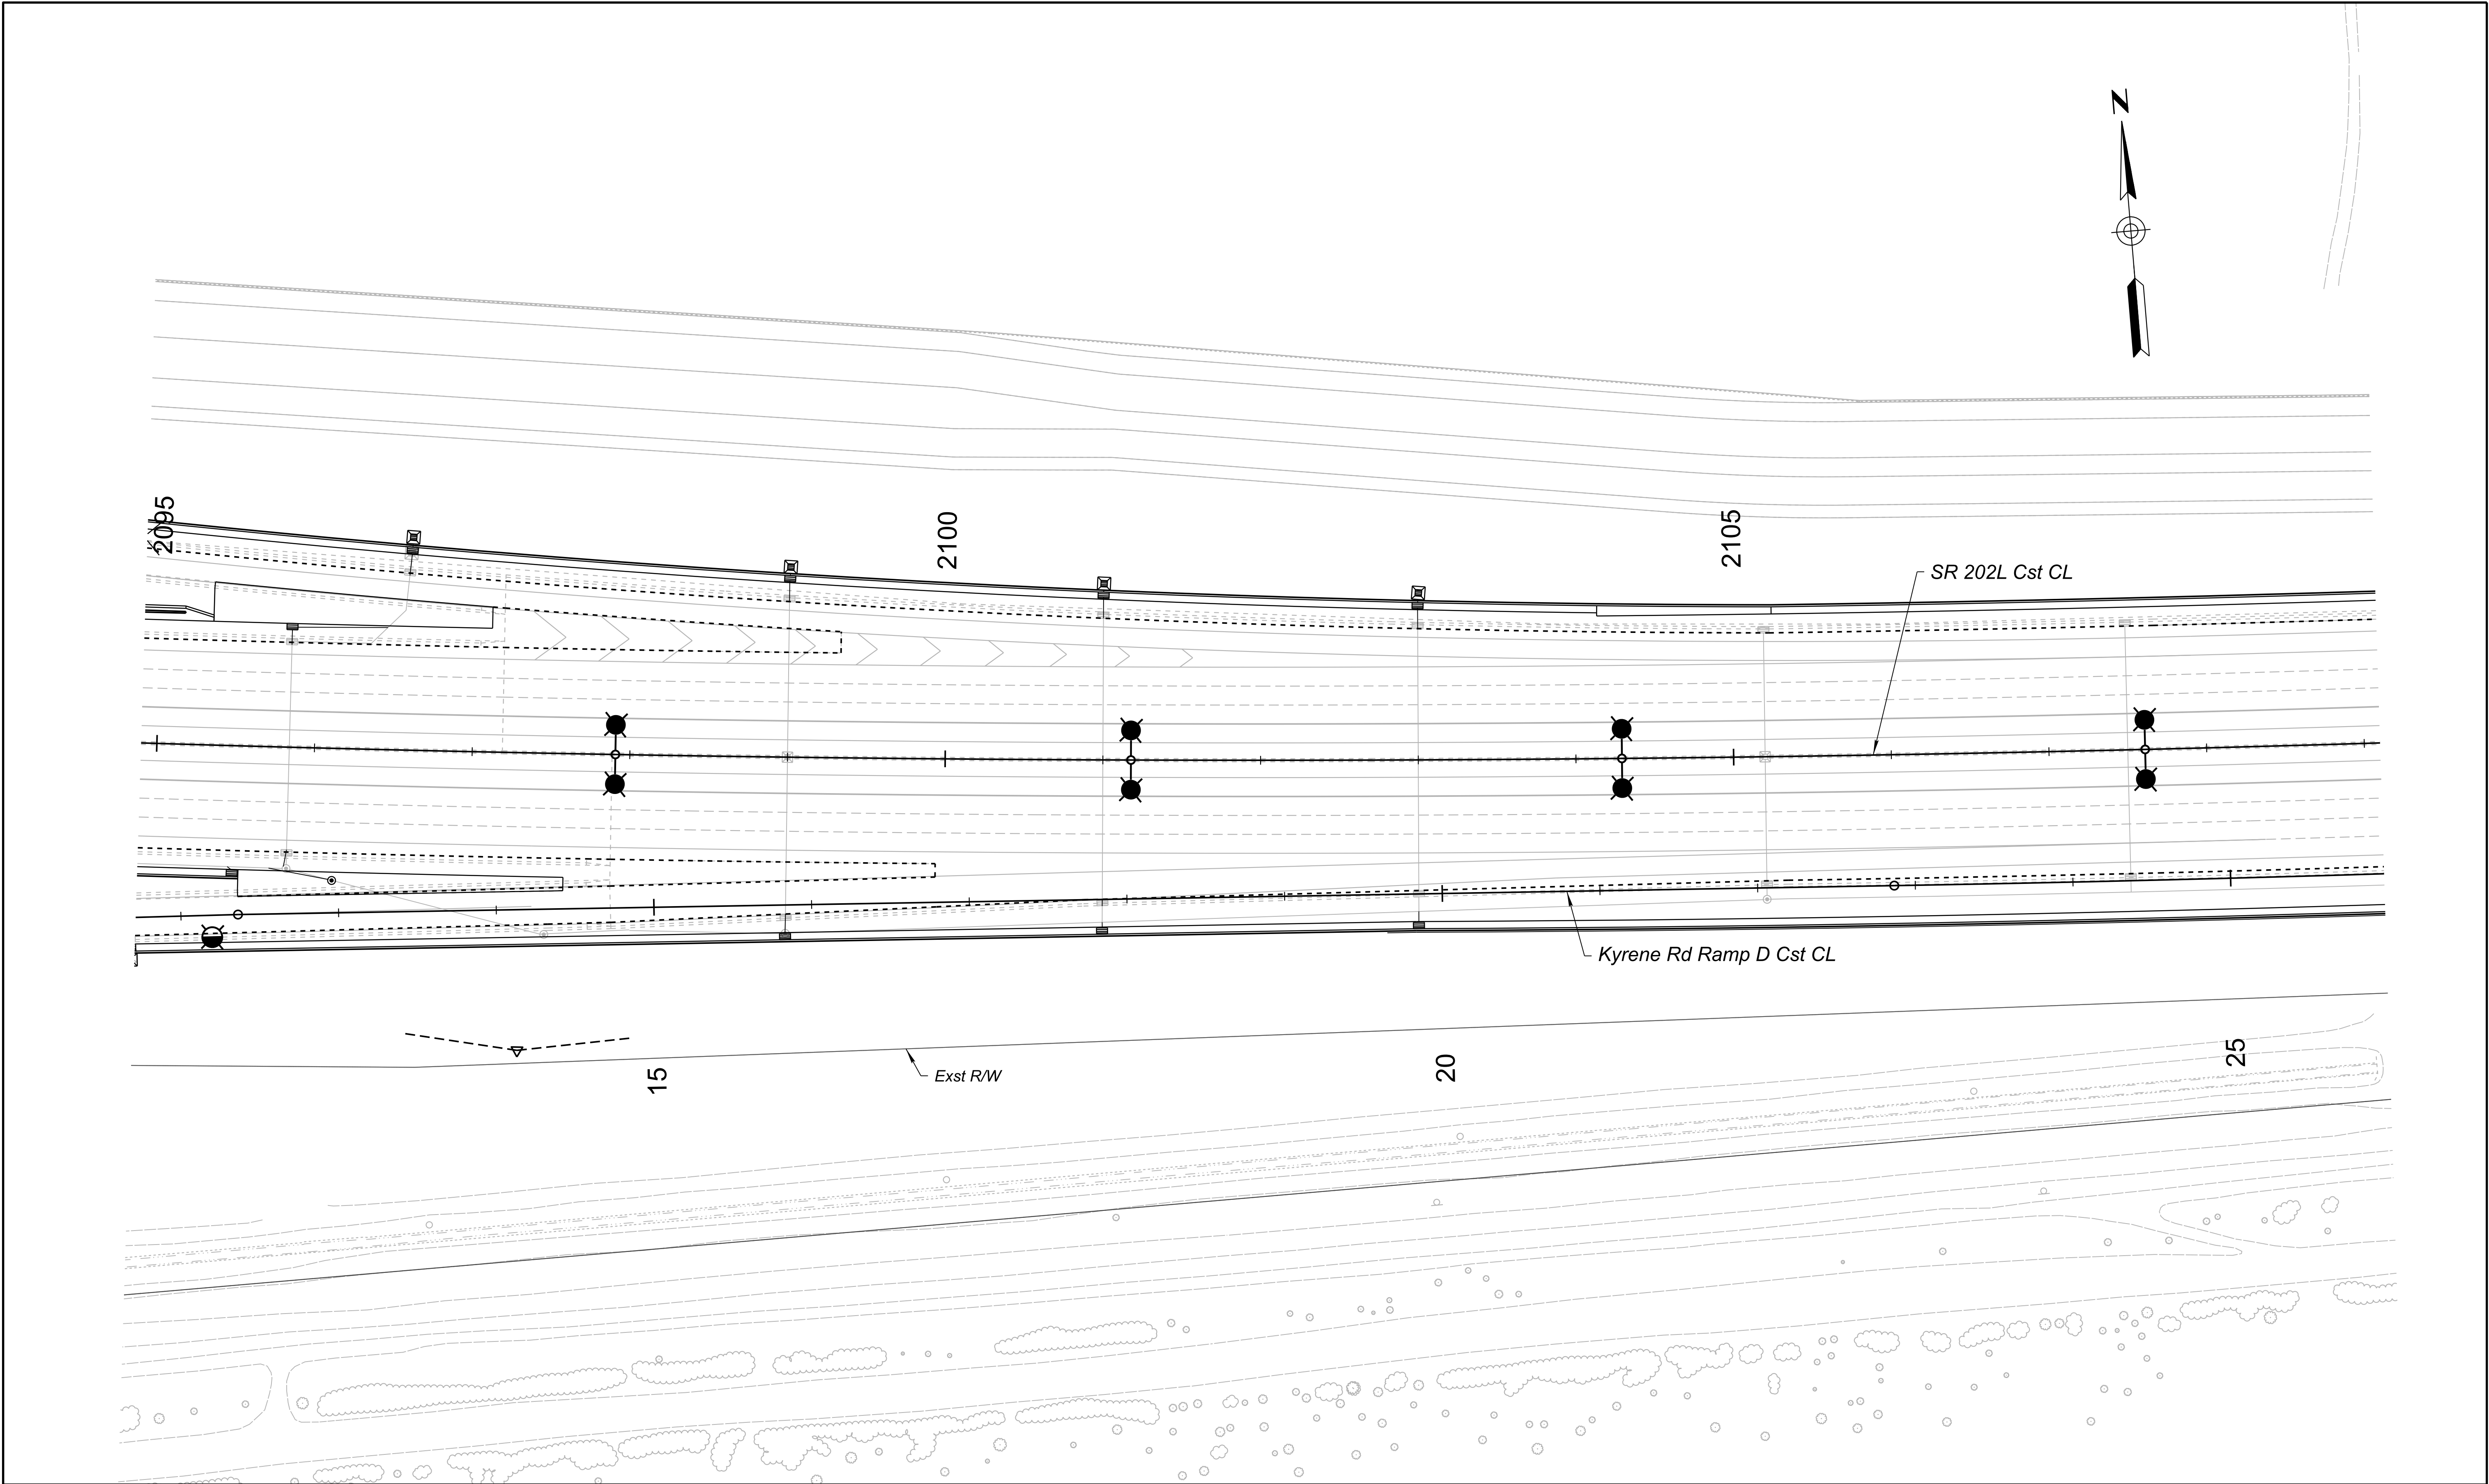

|   |   |      |      |   |                                                          |                                                   |                     |             |                |           |                 |                |
|---|---|------|------|---|----------------------------------------------------------|---------------------------------------------------|---------------------|-------------|----------------|-----------|-----------------|----------------|
| <div>PRELIMINARY</div> <div>STAGE III</div> <div>Review</div> <div>NOT FOR CONSTRUCTION OR RECORDING</div> | DESIGN   | NAME | DATE | ARIZONA DEPARTMENT OF TRANSPORTATION<br>PROJECT DELIVERY AND OPERATIONS DIVISION<br>DRAINAGE DESIGN SECTION | ROUTE                                                    | F.H.W.A. Arizona Division                         | STATE<br>ARIZ.      | PROJECT NO. | FEDERAL ID NO. | SHEET NO. | TOTAL SHEETS    | RECORD DRAWING |
|   | DRAWN   |      |      |   | MILEPOST                                                 |                                                   |                     |             |                |           |                 |                |
|   | CHECKED   |      |      |   | STRUCTURE NO.                                            | LOCATION SR 202L SANTAN FREEWAY - I-10 TO SR 101L |                     |             |                |           | DWG No. D-02.10 |                |
|   | <div><div></div><div>501 N 44th St, Suite 300<br/>Phoenix, AZ 85008-4505<br/>Tel (602) 454-0402<br/>www.typpsa.us</div></div> |      |      |   | SR 202L<br>DRAINAGE PLAN SHEET<br>STA 2095+00 TO 2109+00 |                                                   | TRACS NO. F0847 01D |             | ____ OF ____   |           |                 |                |
|   | <div><div>TYP</div><div>SA</div></div>                                                                                        |      |      |   |                                                          |                                                   |                     |             |                |           |                 |                |