


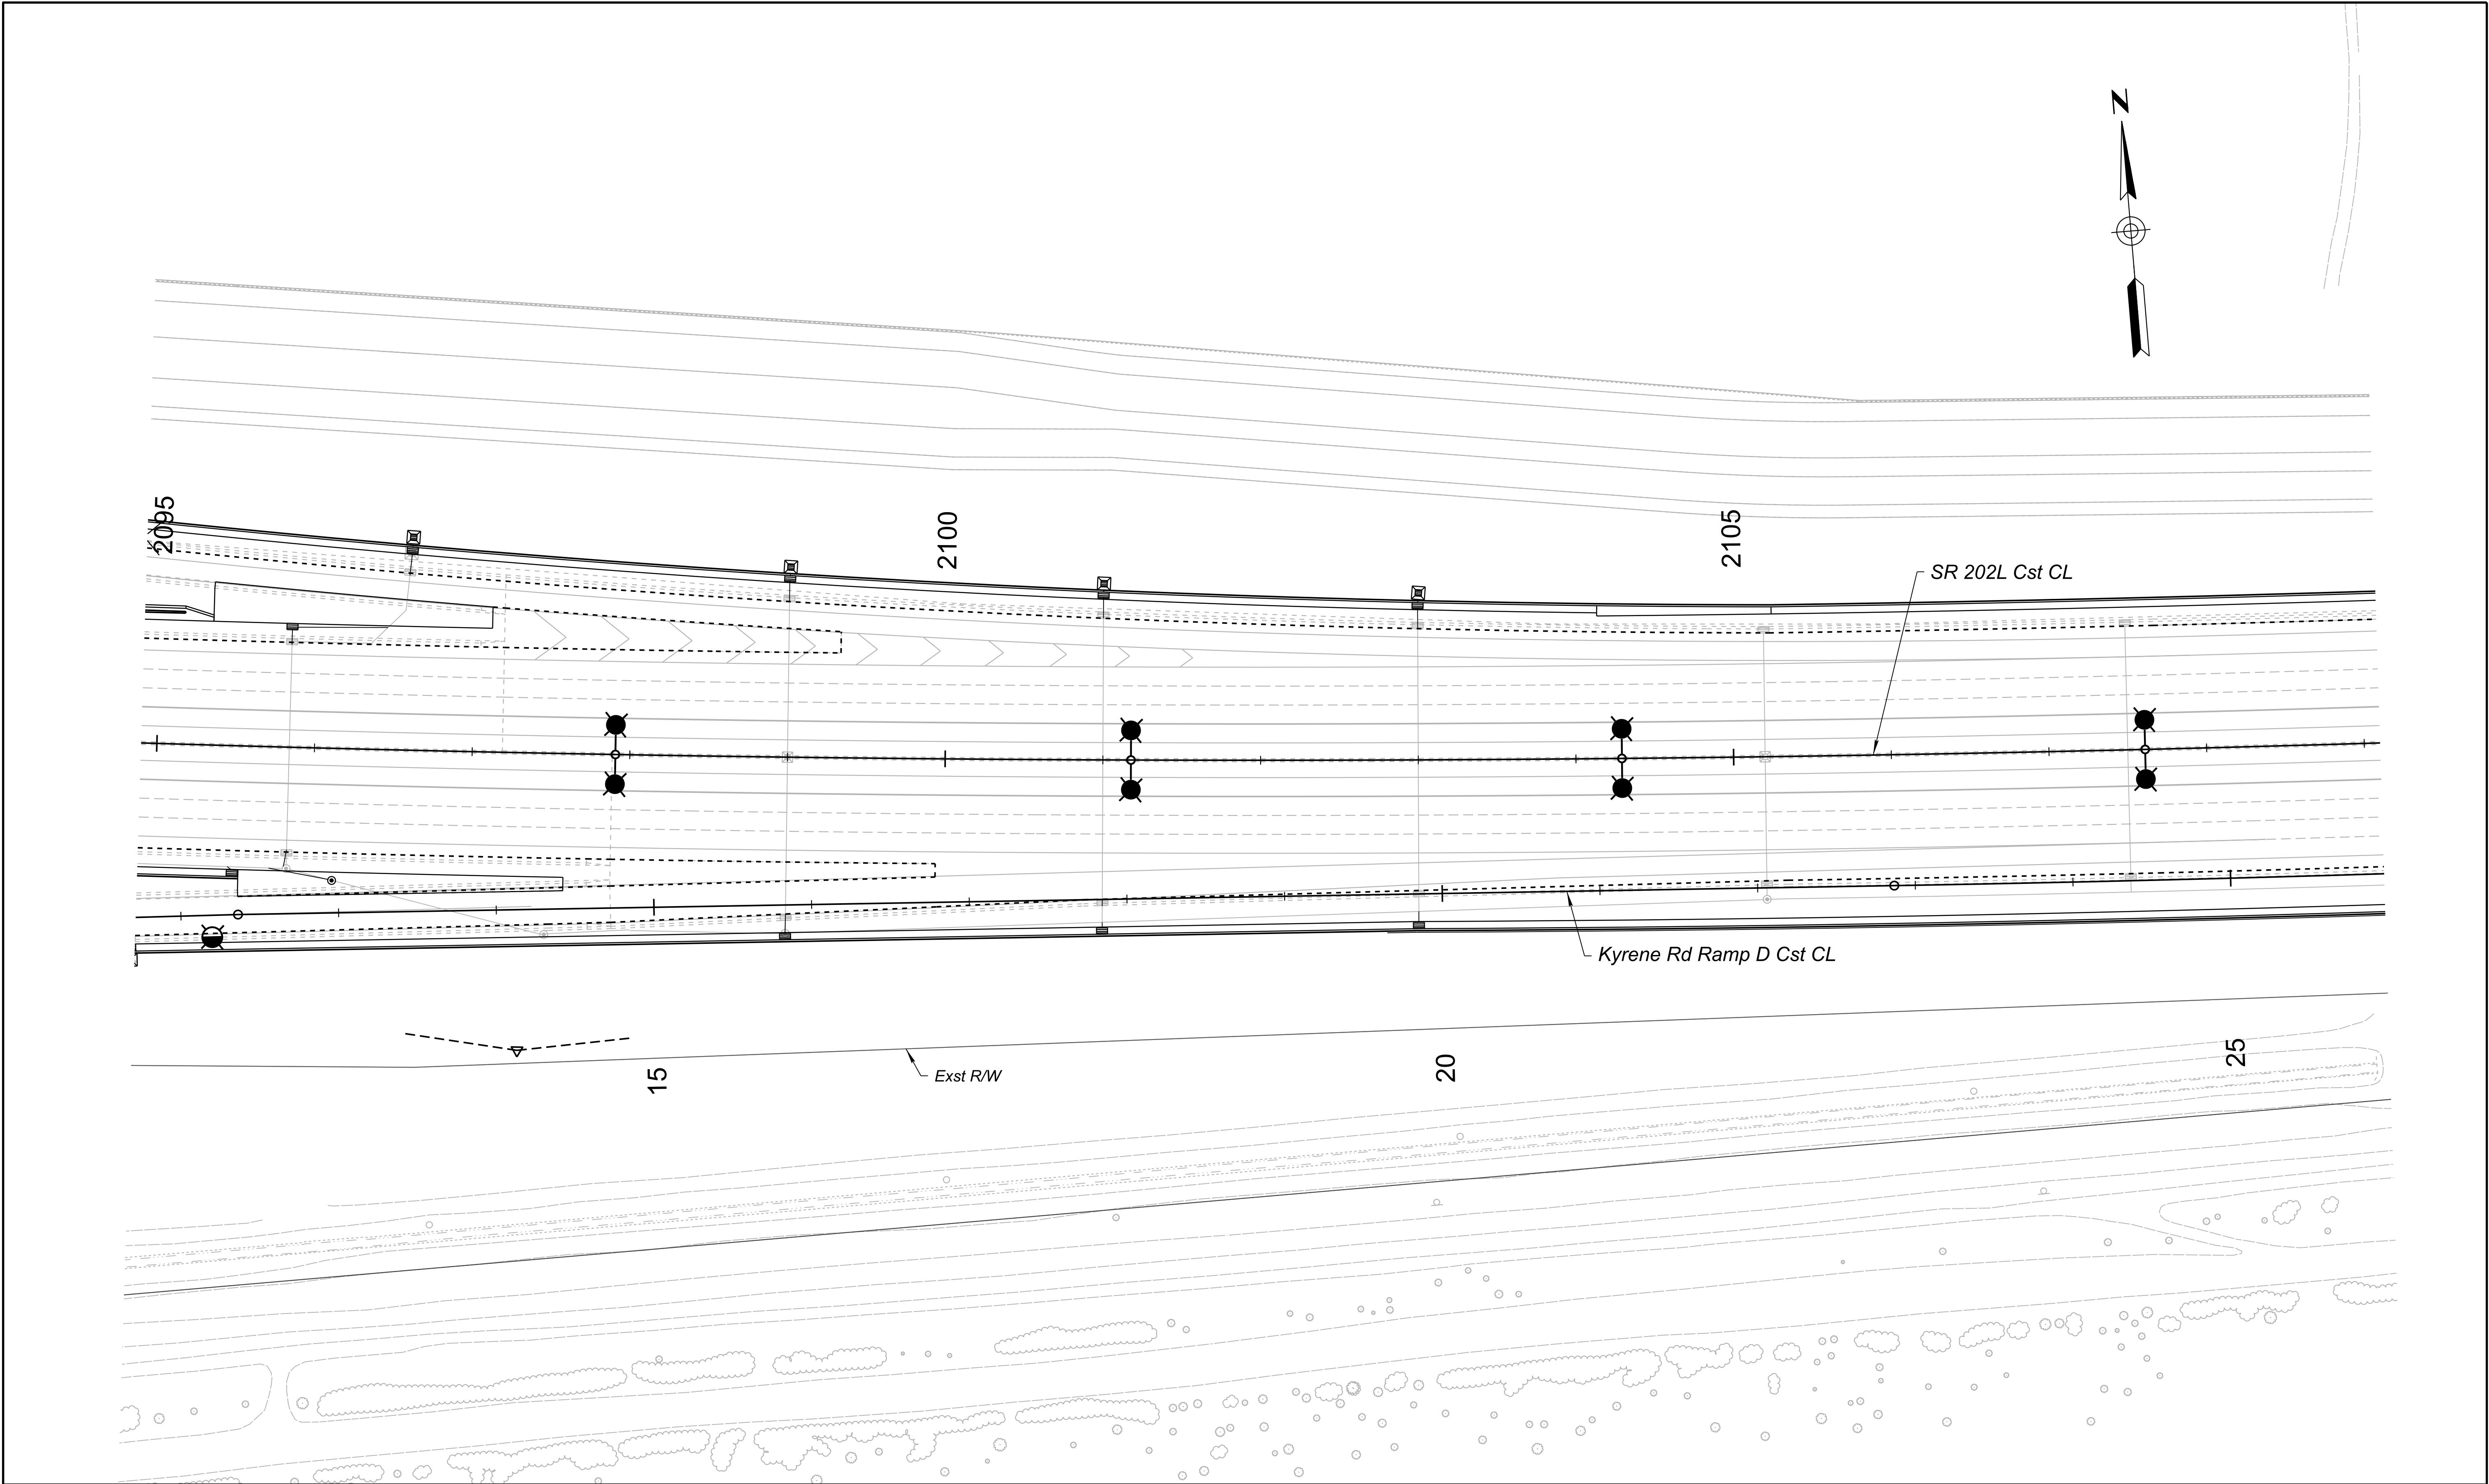

PRELIMINARY STAGE III Review NOT FOR CONSTRUCTION OR RECORDING	DESIGN	NAME	DATE	ARIZONA DEPARTMENT OF TRANSPORTATION PROJECT DELIVERY AND OPERATIONS DIVISION DRAINAGE DESIGN SECTION	ROUTE	F.H.W.A. Arizona Division	STATE ARIZ.	PROJECT NO.	FEDERAL ID NO.	SHEET NO.	TOTAL SHEETS	RECORD DRAWING		
	DRAWN				MILEPOST									
	CHECKED				 501 N 44th St, Suite 300 Phoenix, AZ 85008-4505 Tel (602) 454-0402 www.typsas.us			SR 202L DRAINAGE PLAN SHEET STA 2095+00 TO 2109+00						
								STRUCTURE NO.	LOCATION SR 202L SANTAN FREEWAY - I-10 TO SR 101L DWG No. D-02.10					
					TRACS NO. F0847 01D		OF							