
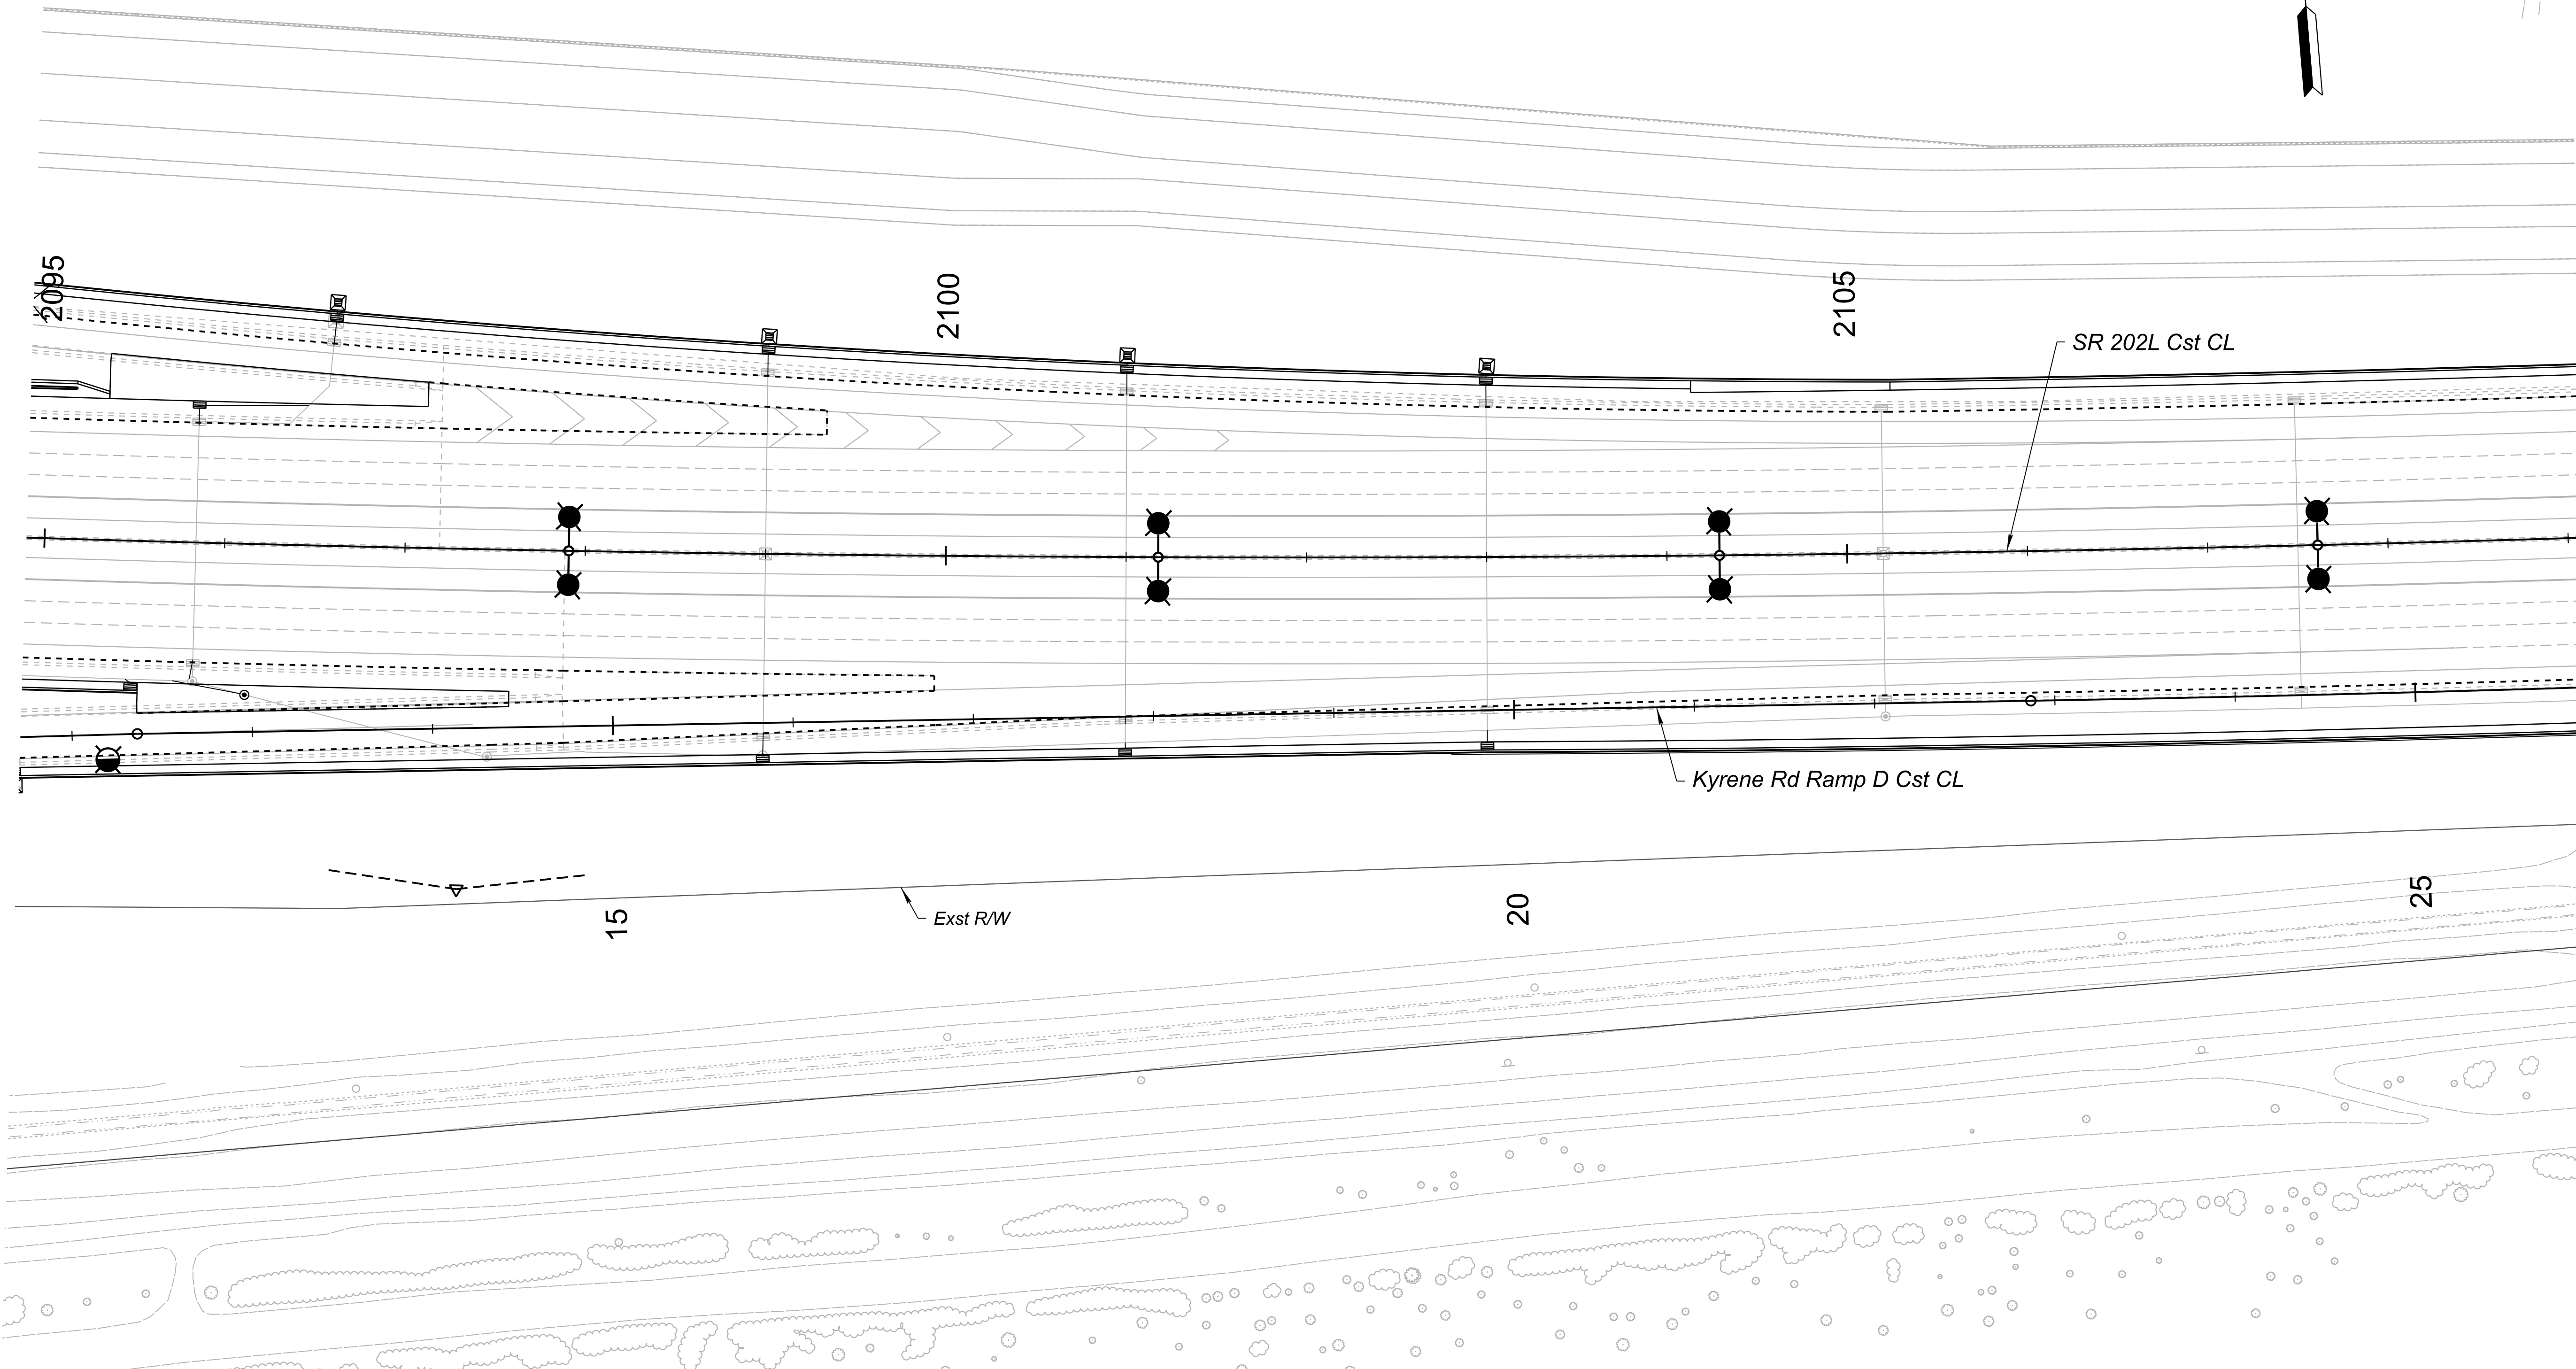


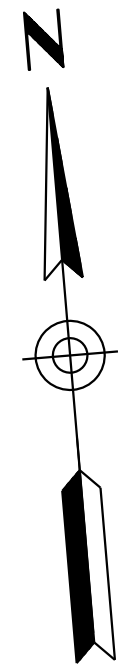

APPROVED

PRELIMINARY STAGE III Review NOT FOR CONSTRUCTION OR RECORDING	NAME		DATE	ARIZONA DEPARTMENT OF TRANSPORTATION PROJECT DELIVERY AND OPERATIONS DIVISION DRAINAGE DESIGN SECTION SR 202L DRAINAGE PLAN SHEET STA 2095+00 TO 2109+00	ROUTE SR 202L	F.H.W.A. Arizona Division	STATE ARIZ.	PROJECT NO.	FEDERAL ID NO.	SHEET NO.	TOTAL SHEETS	RECORD DRAWING	
	DESIGN				MILEPOST								
	DRAWN				501 N 44th St, Suite 300 Phoenix, AZ 85008-4505 Tel (602) 454-0402 www.typpsa.us	STRUCTURE NO.	SR 202L SANTAN FREEWAY - I-10 TO SR 101L						DWG No. D-02.10
	CHECKED						TRACS NO. F0847 01D						____ OF ____
	 501 N 44th St, Suite 300 Phoenix, AZ 85008-4505 Tel (602) 454-0402 www.typpsa.us												