


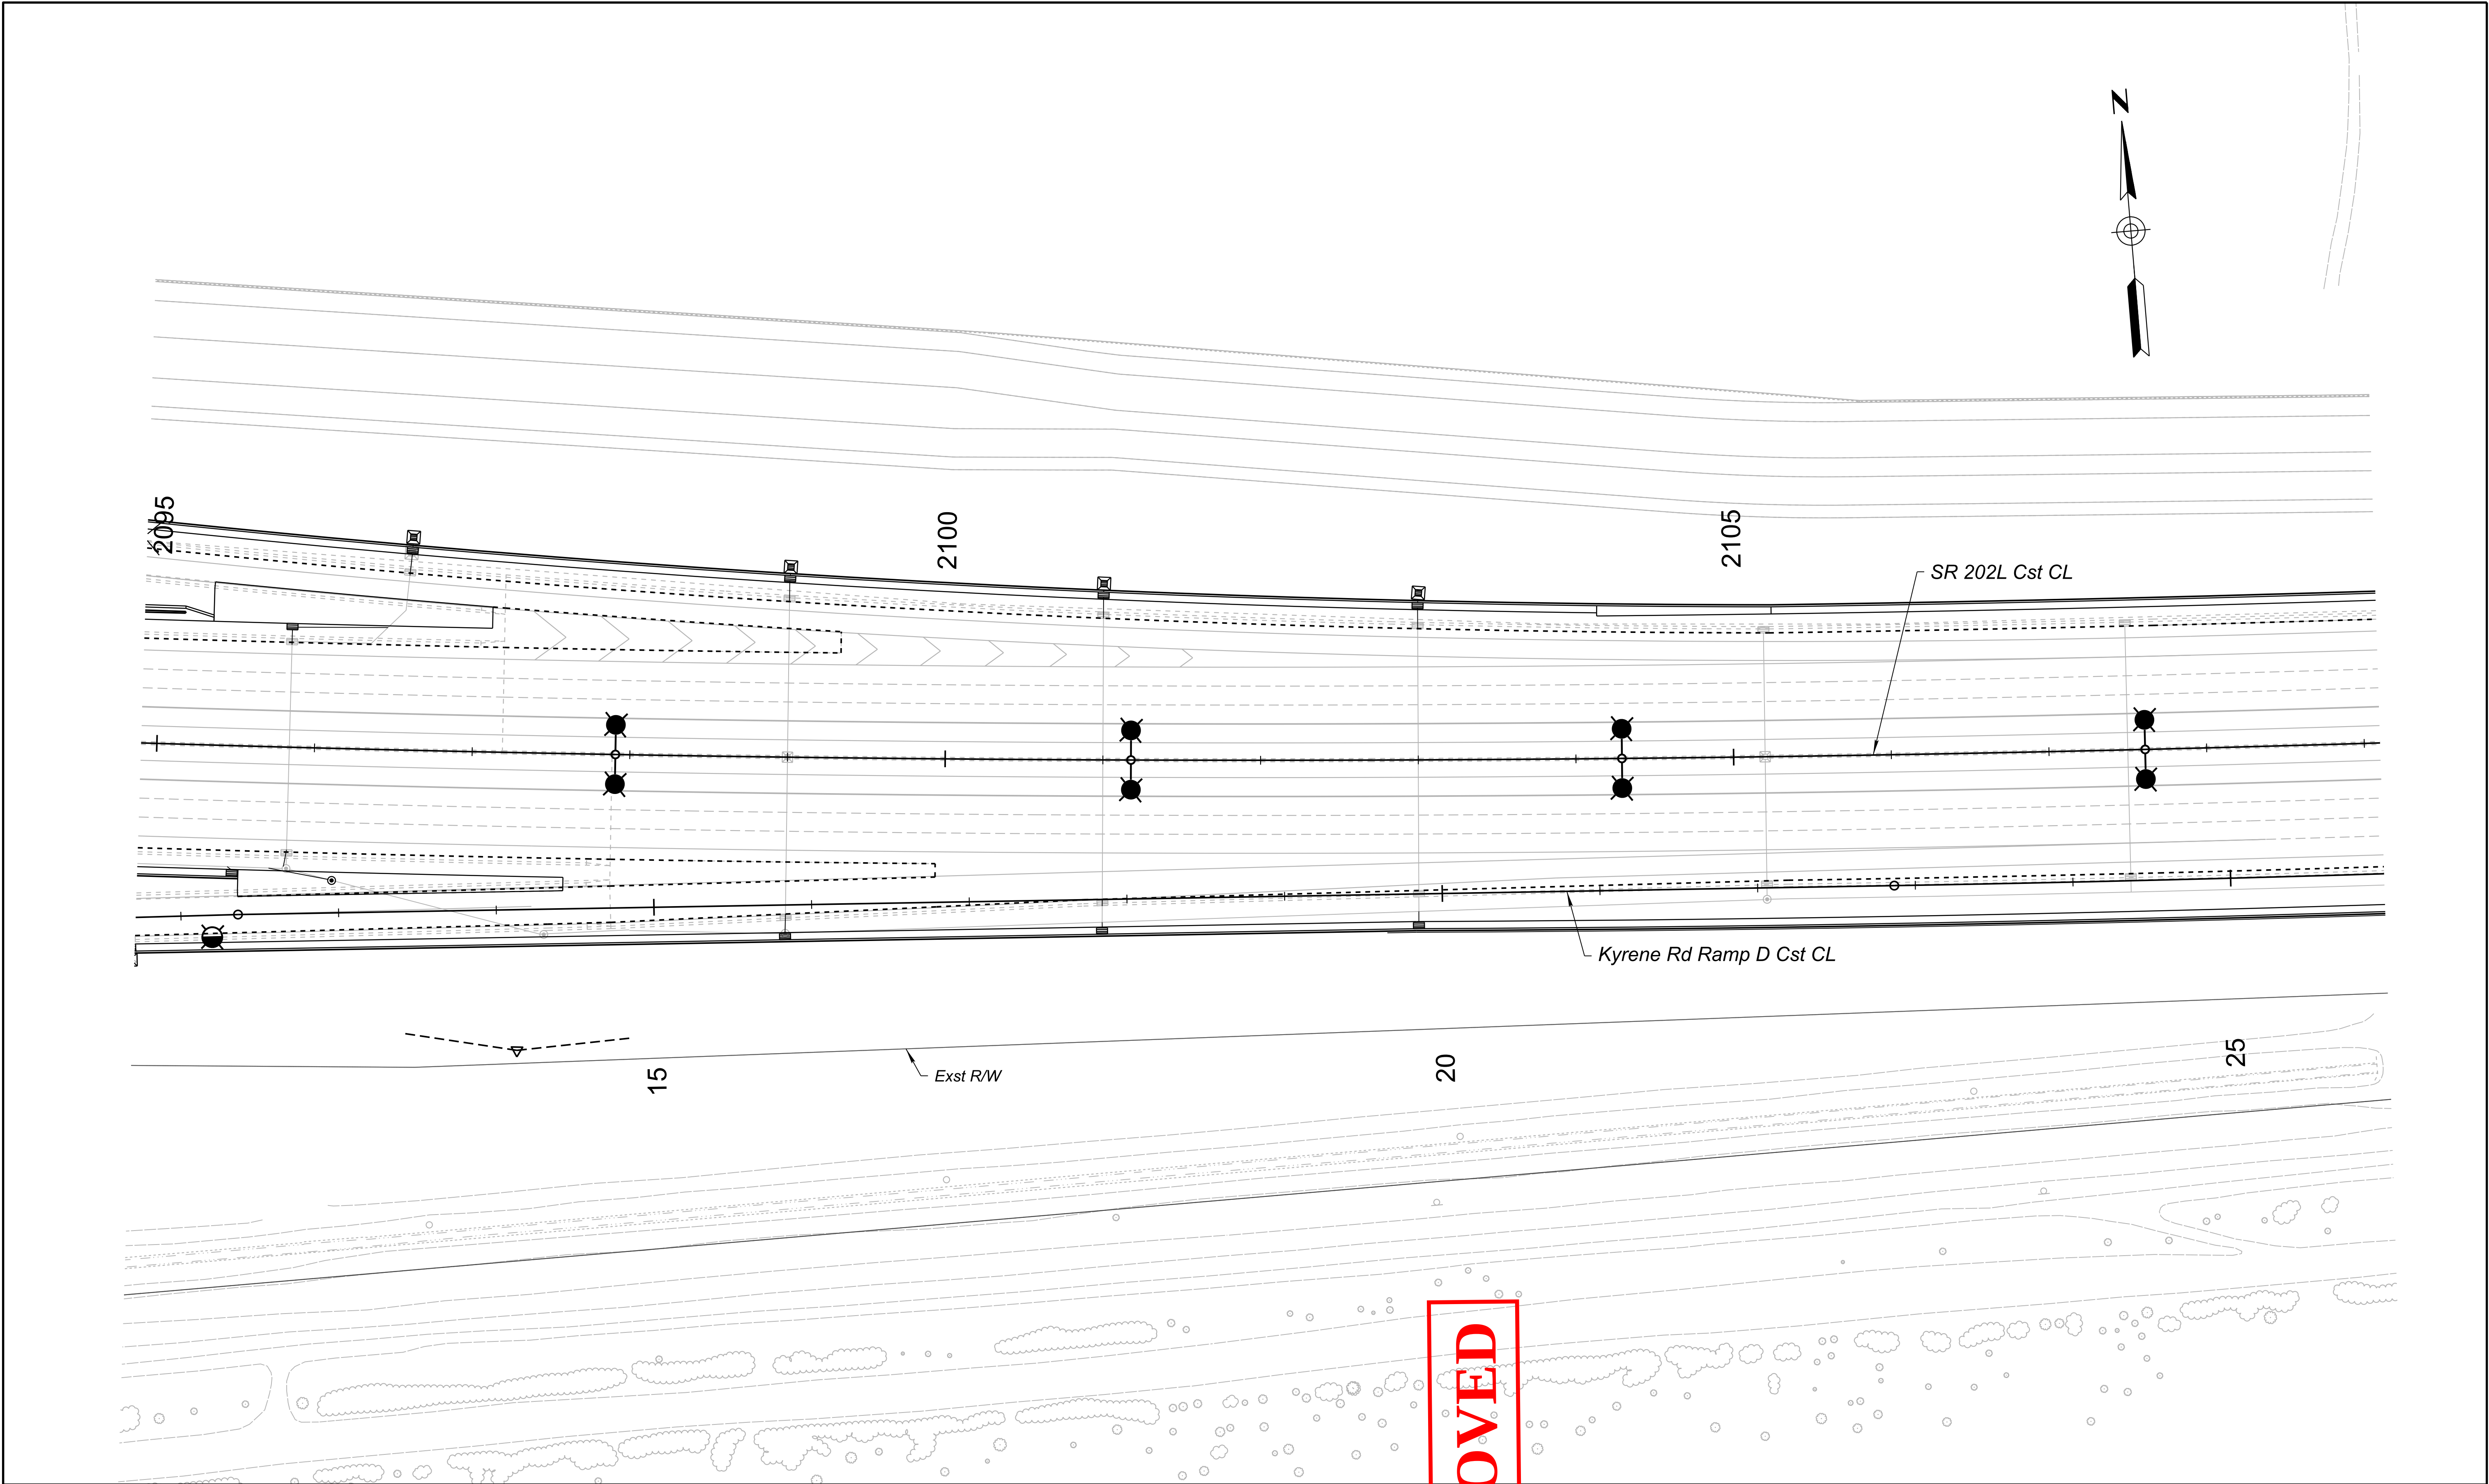

PRELIMINARY STAGE III Review NOT FOR CONSTRUCTION OR RECORDING	DESIGN		NAME	DATE	ARIZONA DEPARTMENT OF TRANSPORTATION PROJECT DELIVERY AND OPERATIONS DIVISION DRAINAGE DESIGN SECTION	ROUTE	F.H.W.A. Arizona Division	STATE ARIZ.	PROJECT NO.	FEDERAL ID NO.	SHEET NO.	TOTAL SHEETS	RECORD DRAWING	
	DRAWN					MILEPOST								
	CHECKED													
			501 N 44th St, Suite 300 Phoenix, AZ 85008-4505 Tel (602) 454-0402 www.typpsa.us			SR 202L DRAINAGE PLAN SHEET STA 2095+00 TO 2109+00	SR 202L SANTAN FREEWAY - I-10 TO SR 101L							DWG No. D-02.10
							TRACS NO. F0847 01D							___ OF ___